


REVISIONS / ISSUED TO

NO.	DATE	BY
1	ISSUED FOR CLIENT REVIEW 2024-09-26	RY

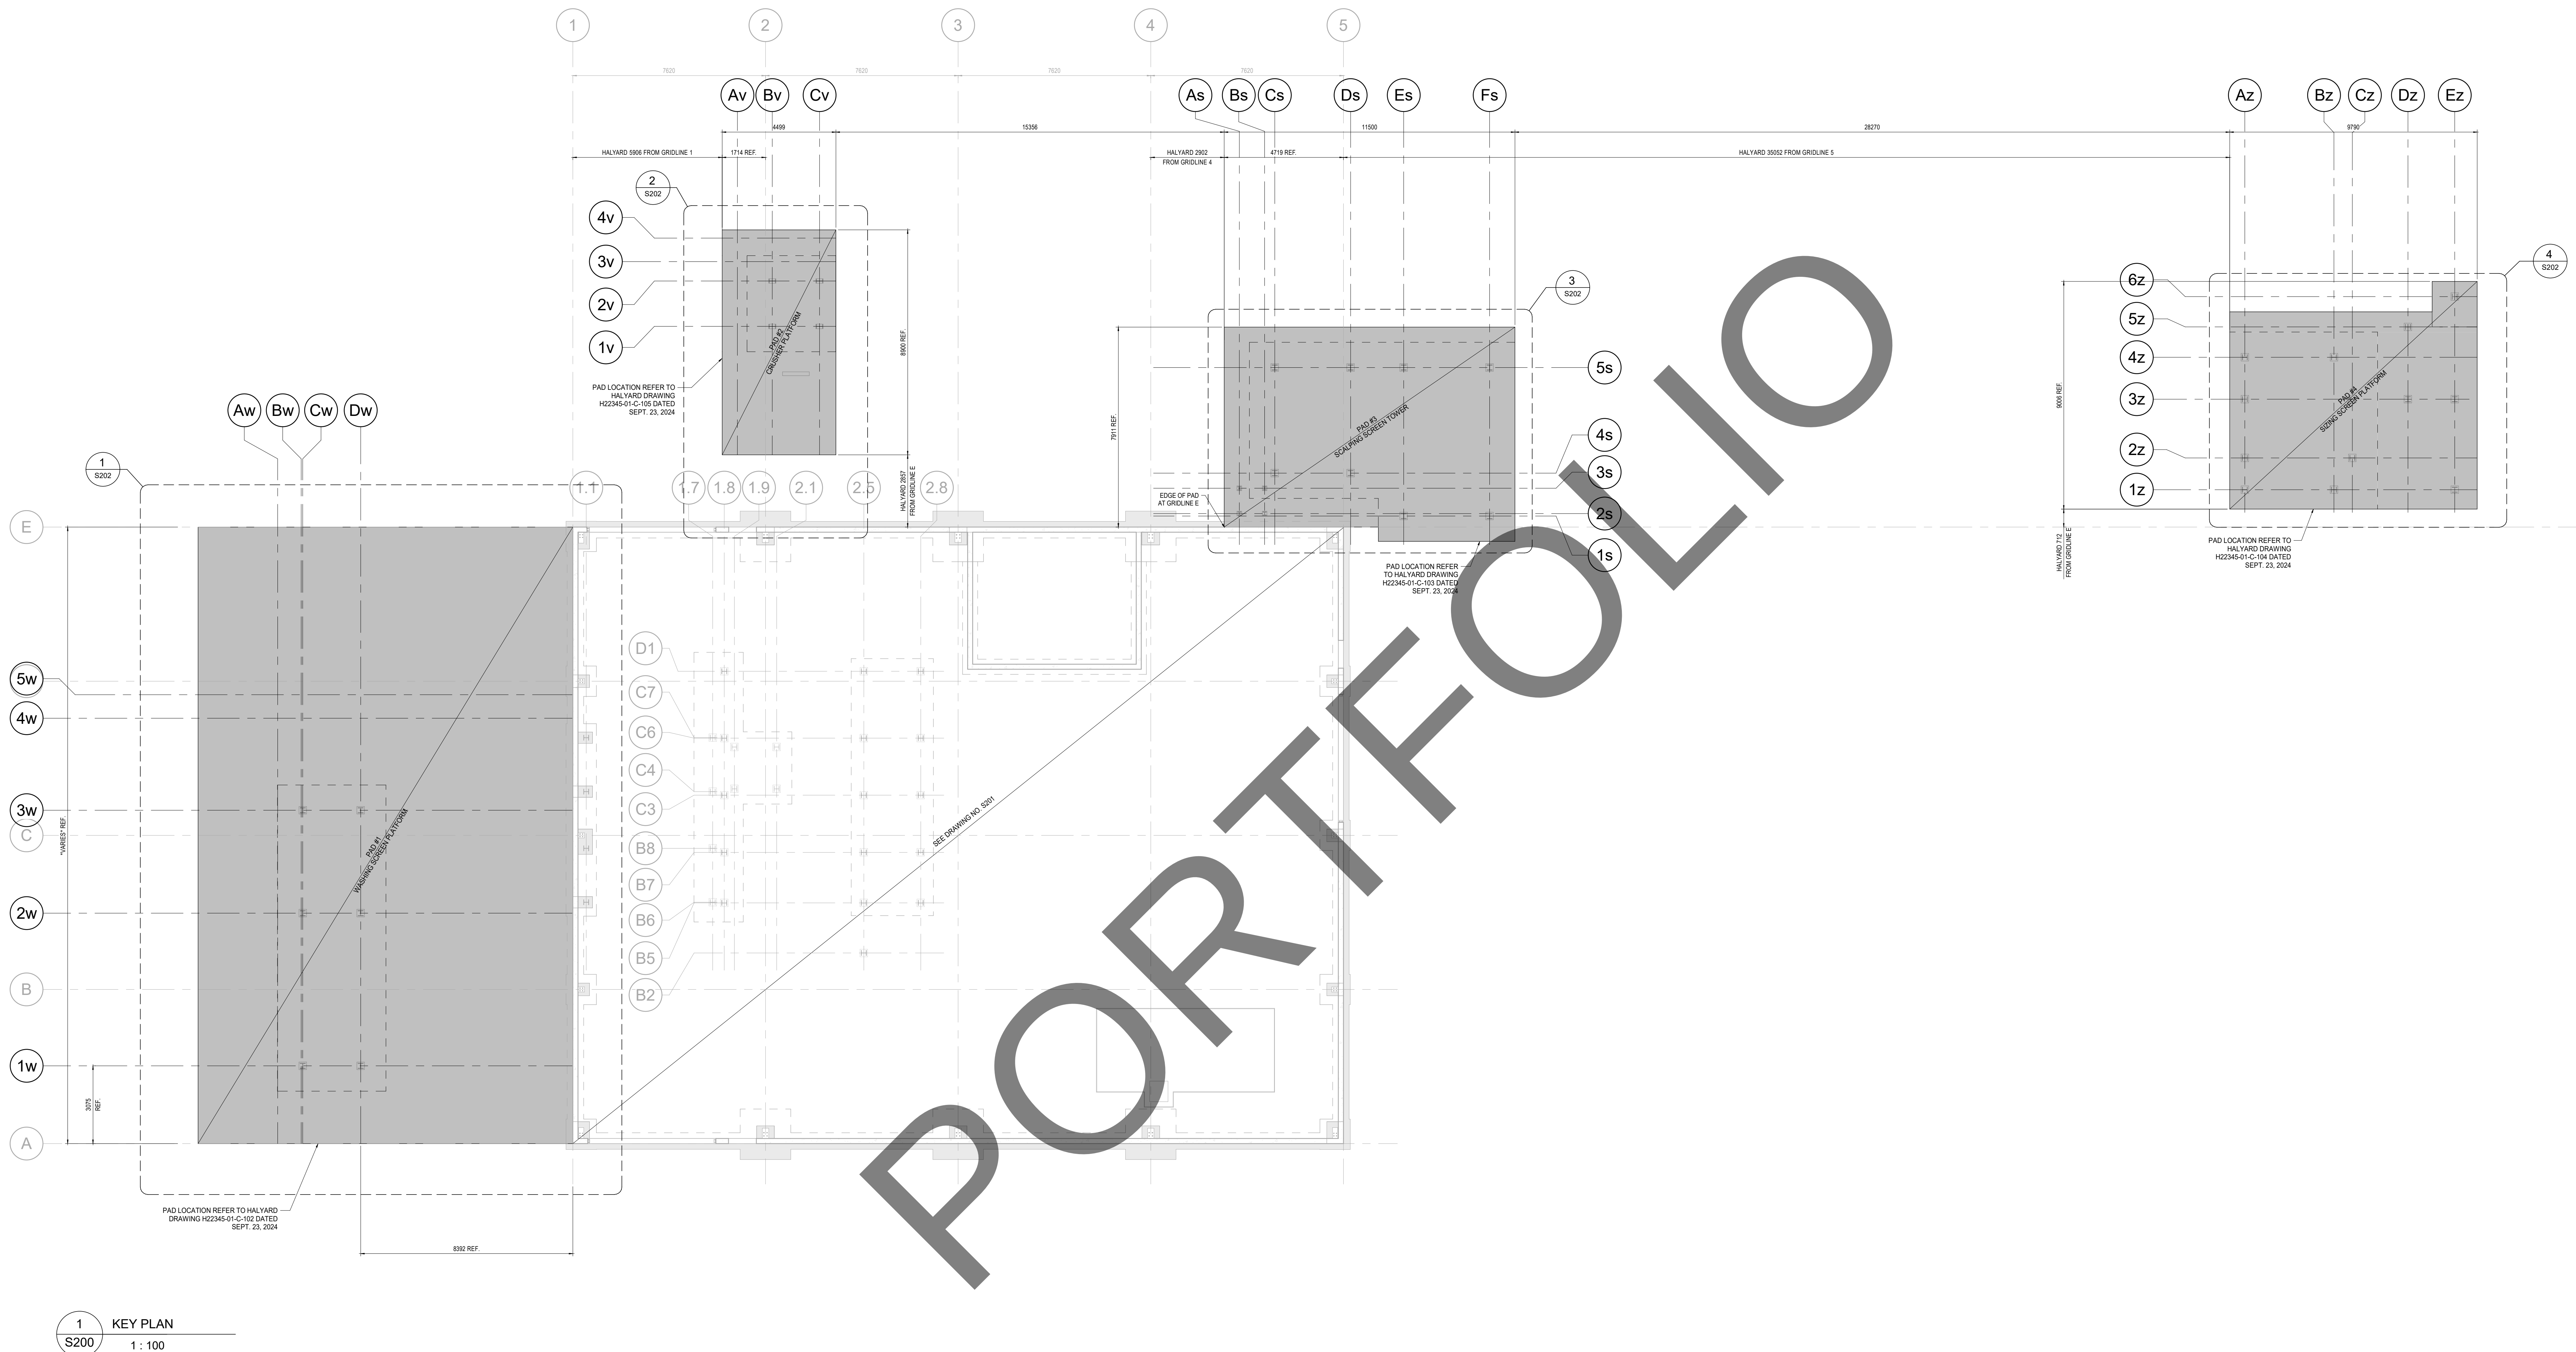

1 KEY PLAN
S200 1 : 100

ARCHITECT / CONSULTANTS

CONTRACTOR SHALL CHECK ALL DIMENSIONS ON THE WORK AND REPORT ANY DISCREPANCY TO THE CONSULTANT BEFORE PROCEEDING. THIS DRAWING IS NOT TO BE USED FOR CONSTRUCTION UNLESS AUTHORIZED IN WRITING BY CONSULTANT.

SEAL / SIGNATURE

ISSUED FOR CONSTRUCTION DATE

CLIENT NAME

ALOCON CONCRETE
FLOOR FINISHING
LTD.

DRAWING TITLE
AGGREGATES
PROCESS BUILDING
FOUNDATION

KEY PLAN

DESIGNED BY / DRAWN BY RY/FB


SCALE 1 : 100

DRAWING NUMBER S200


PROJECT NUMBER 24-060

REVISIONS / ISSUED TO


NO.	DATE	BY
1	ISSUED FOR CLIENT REVIEW 2024-09-17	RY

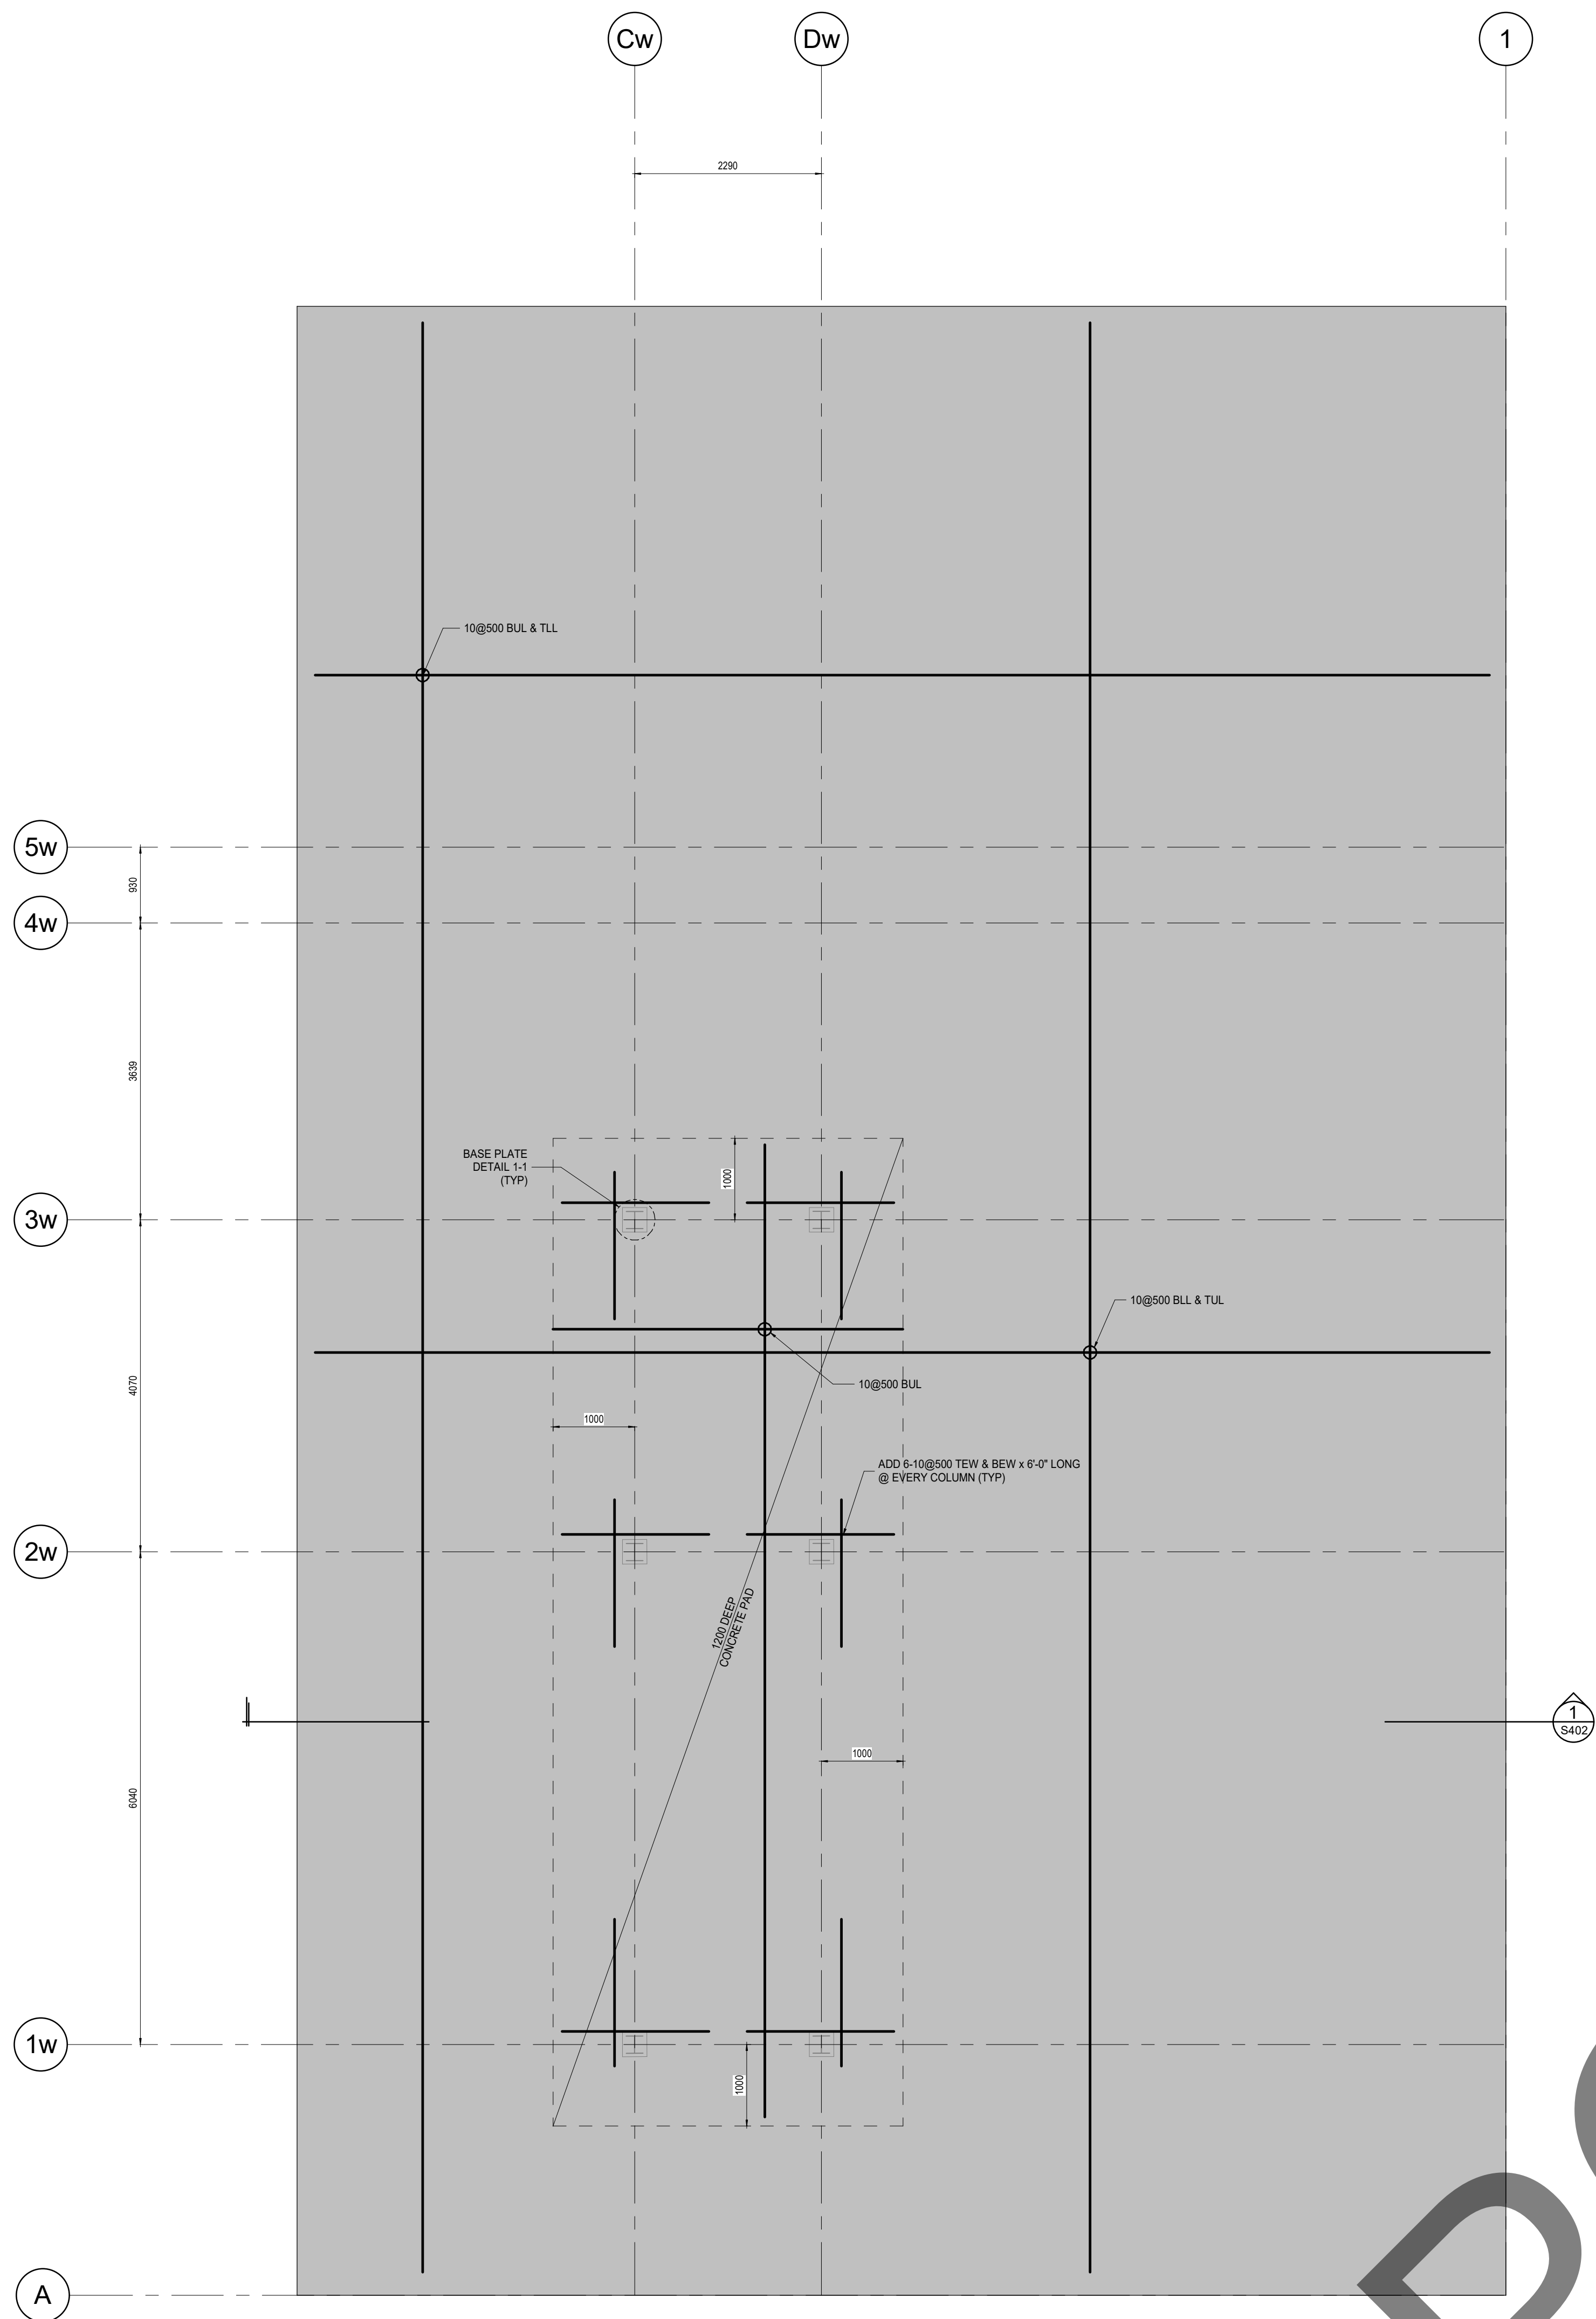


1 PAD #1 WASHING SCREEN PLATFORM
S202 1 : 50 $f_c = 35 \text{ MPa}$

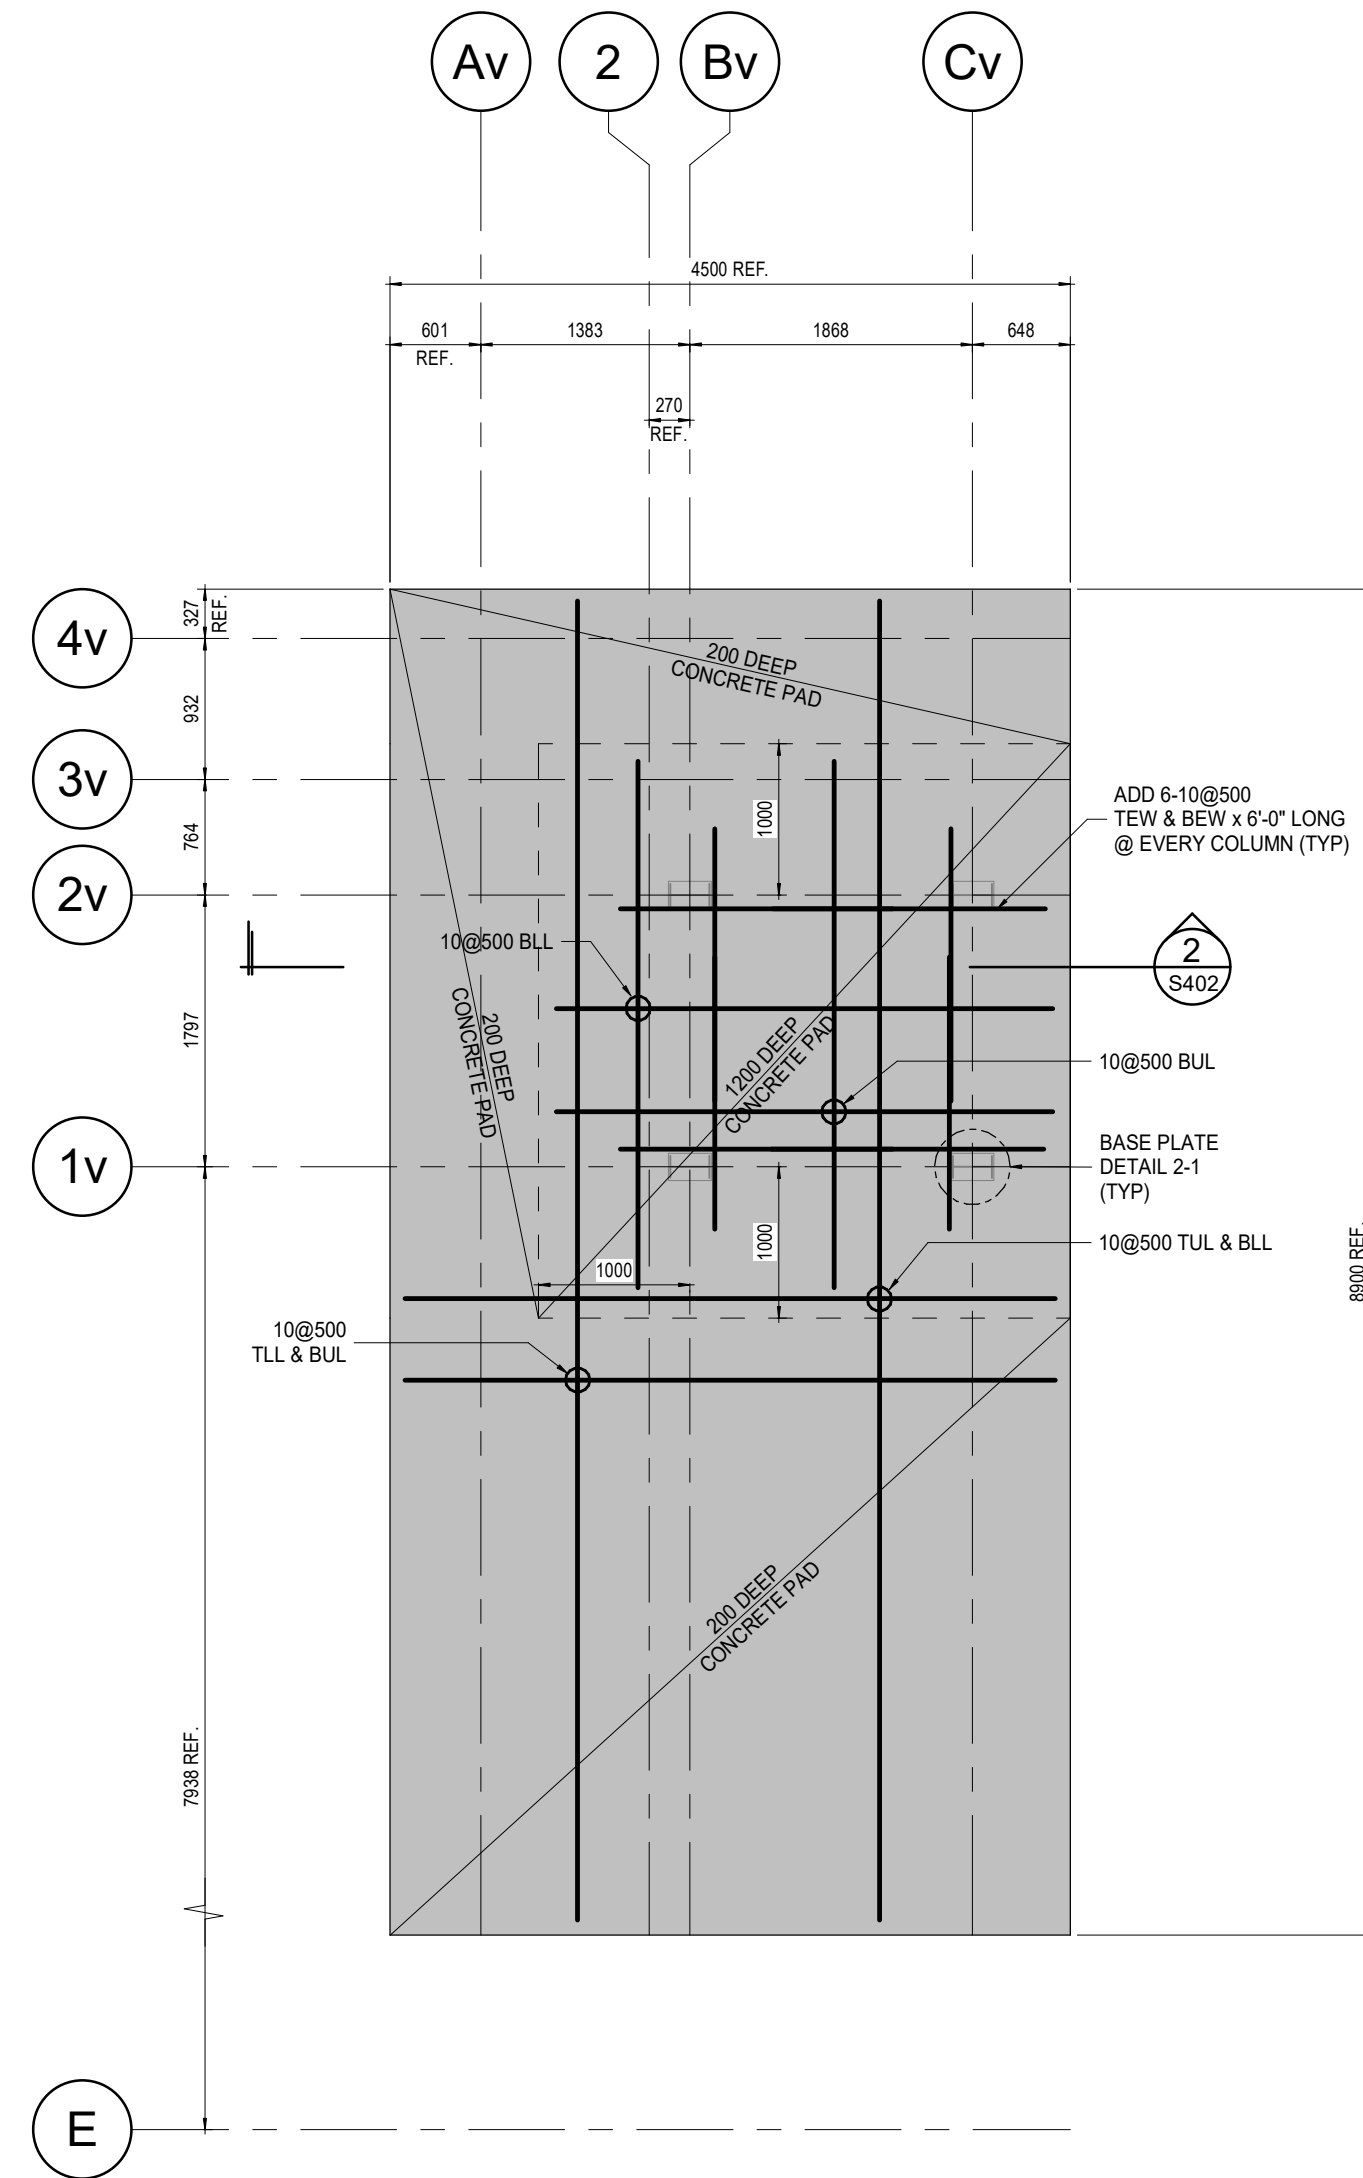


2 PAD #2 CRUSHER PLATFORM
S202 1 : 50 $f_c = 35 \text{ MPa}$

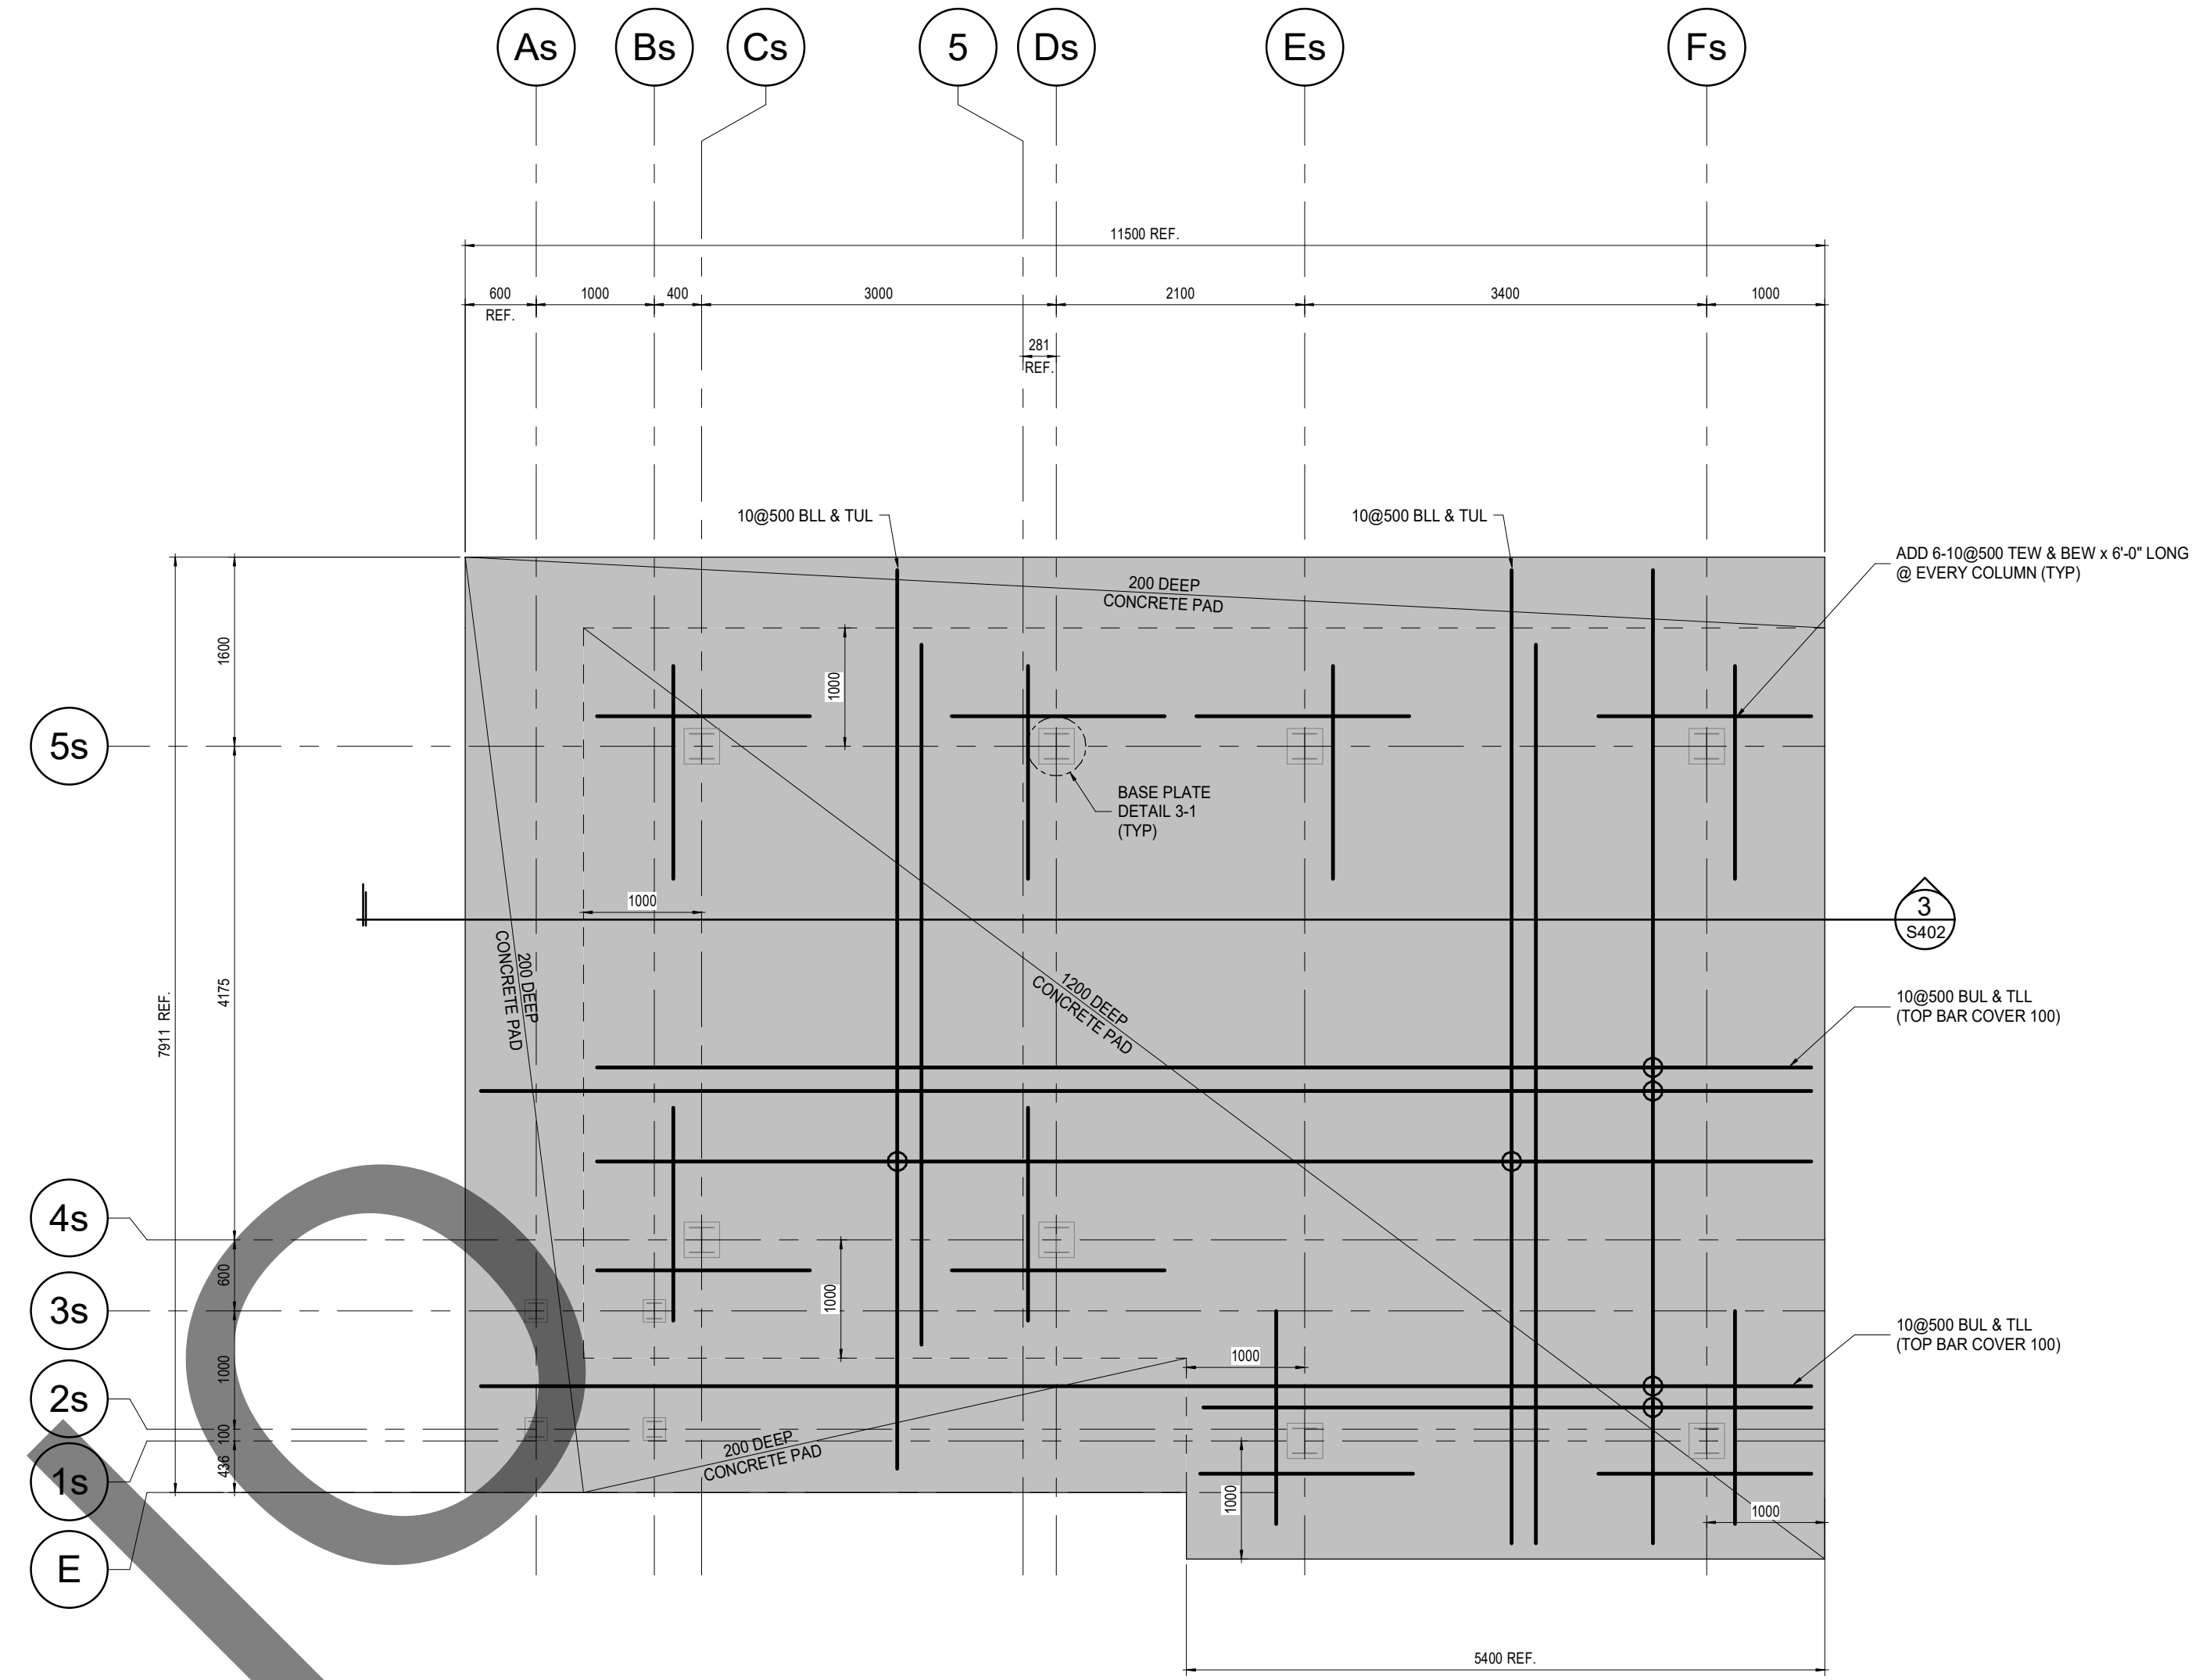


3 PAD #3 SCALPING SCREEN TOWER
S202 1 : 50 $f_c = 35 \text{ MPa}$

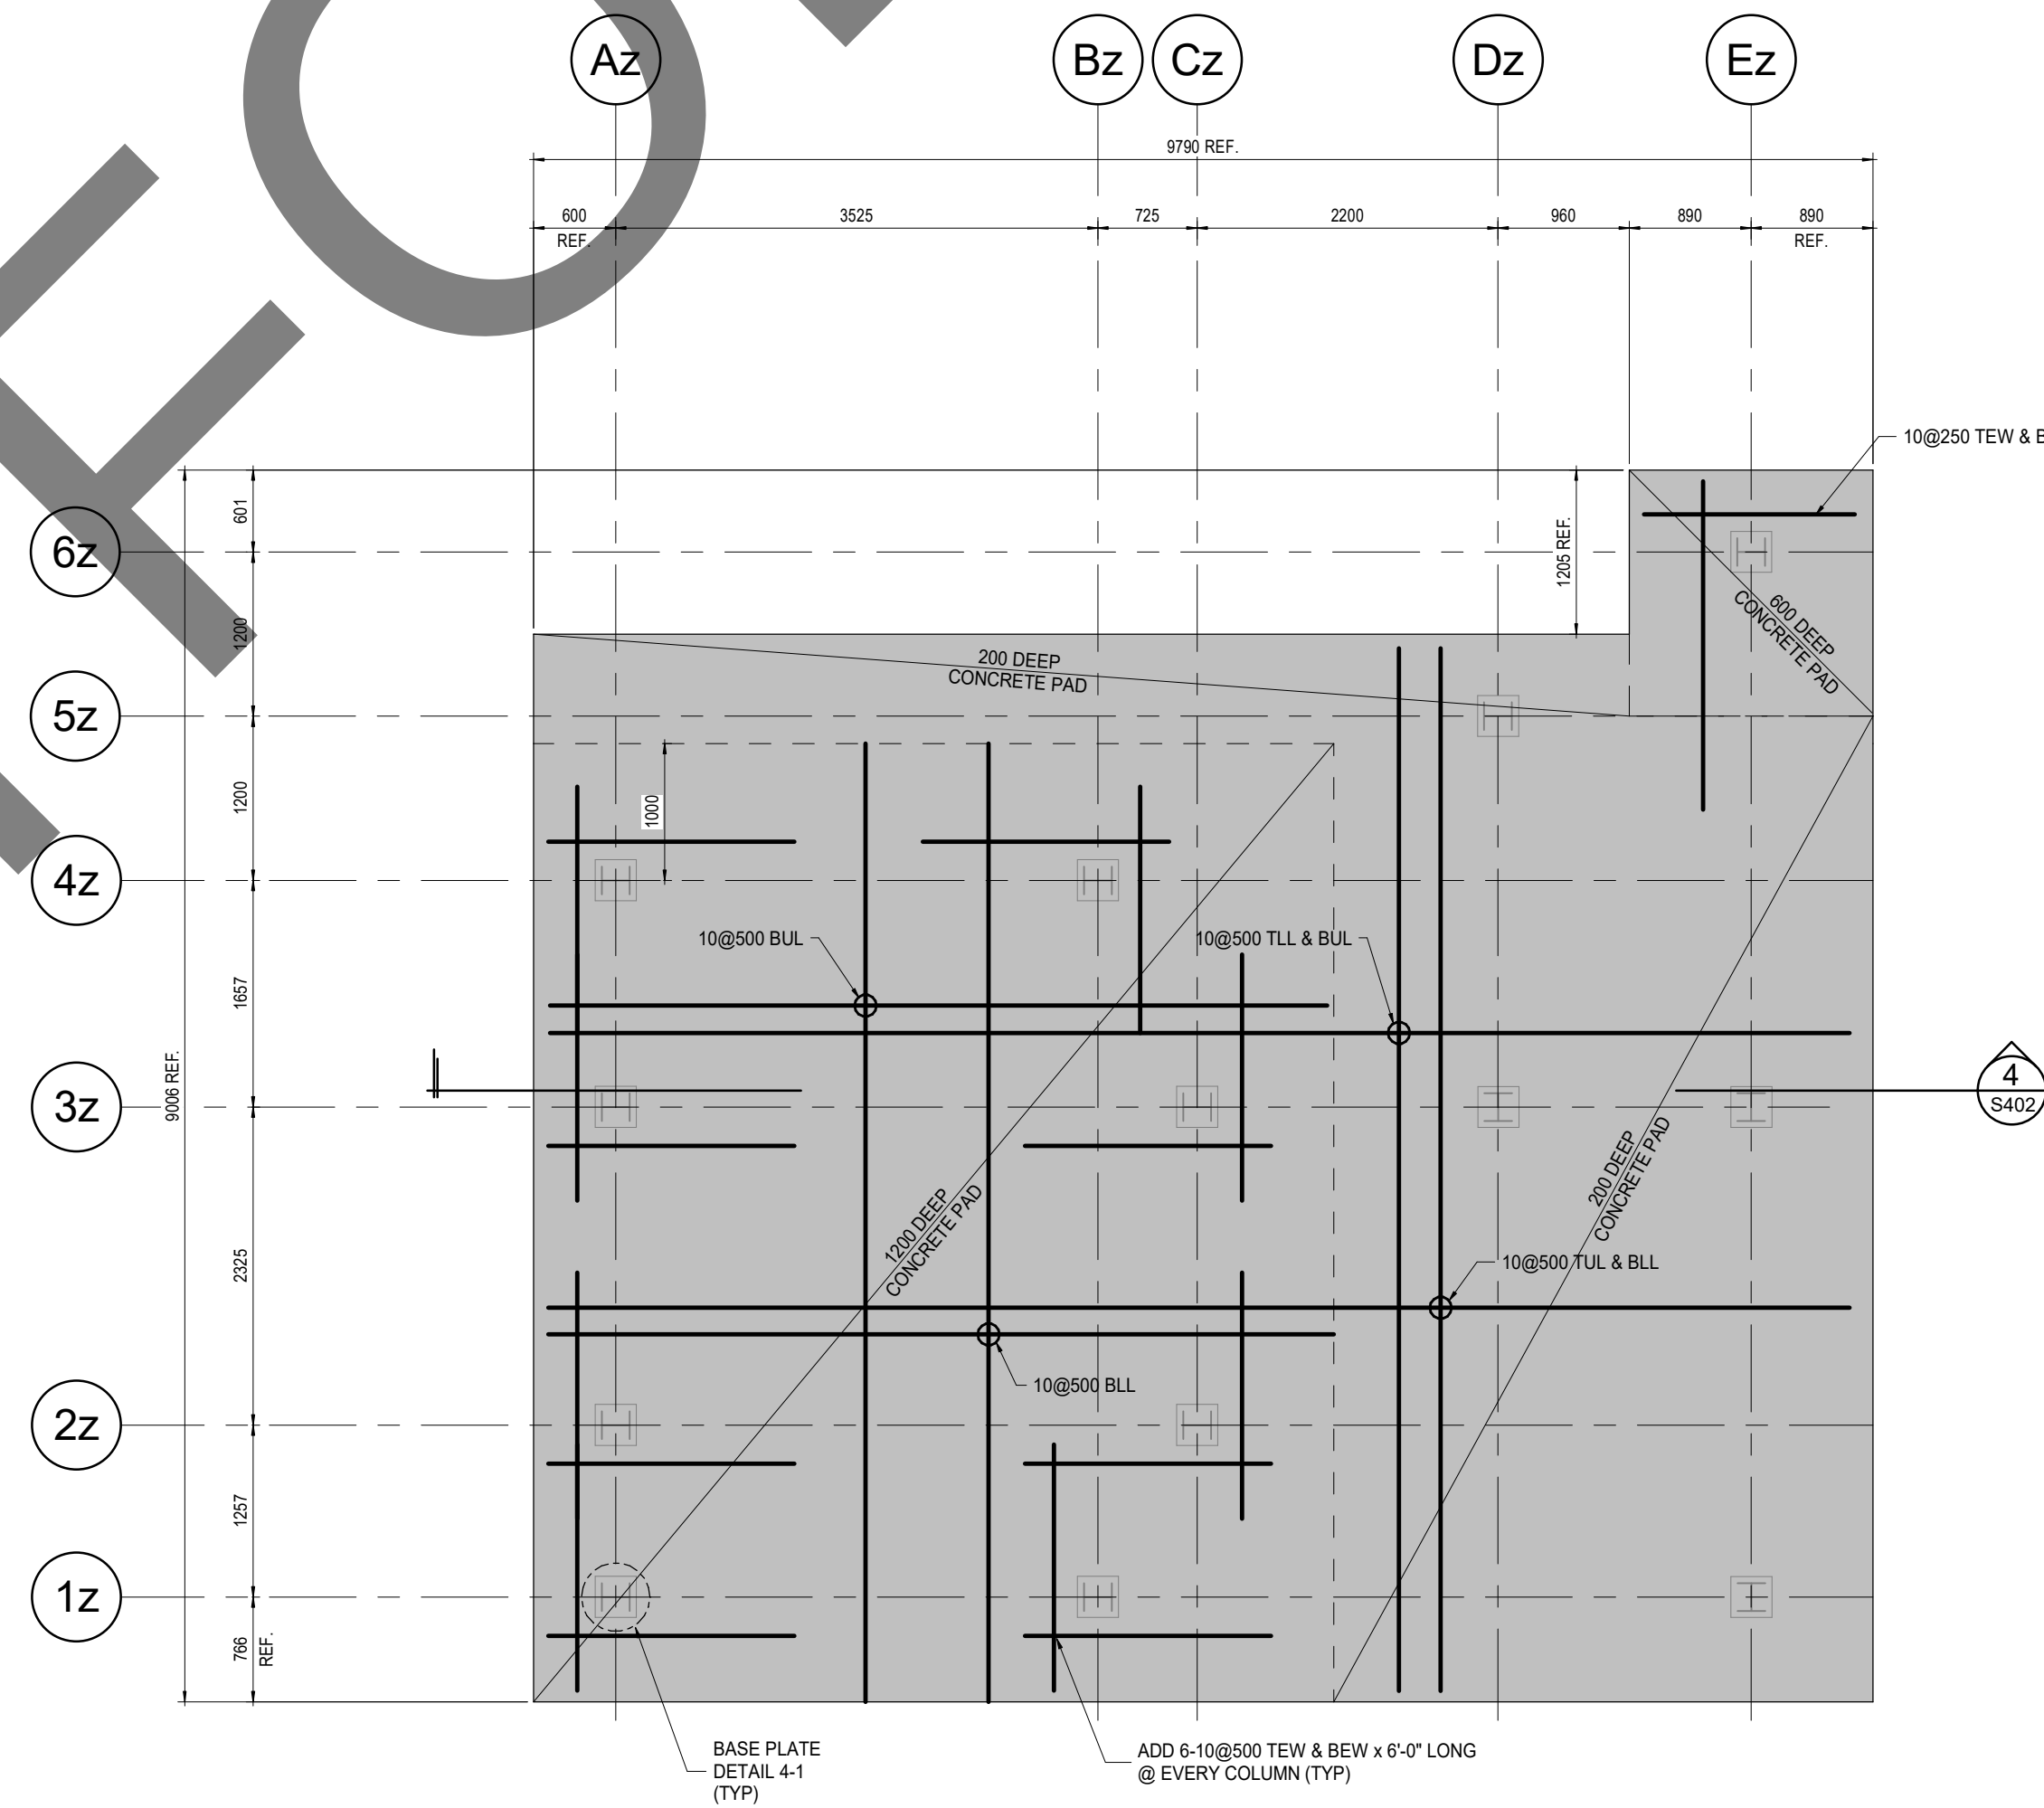


4 PAD #4 SIZING SCREEN TOWER
S202 1 : 50 $f_c = 35 \text{ MPa}$

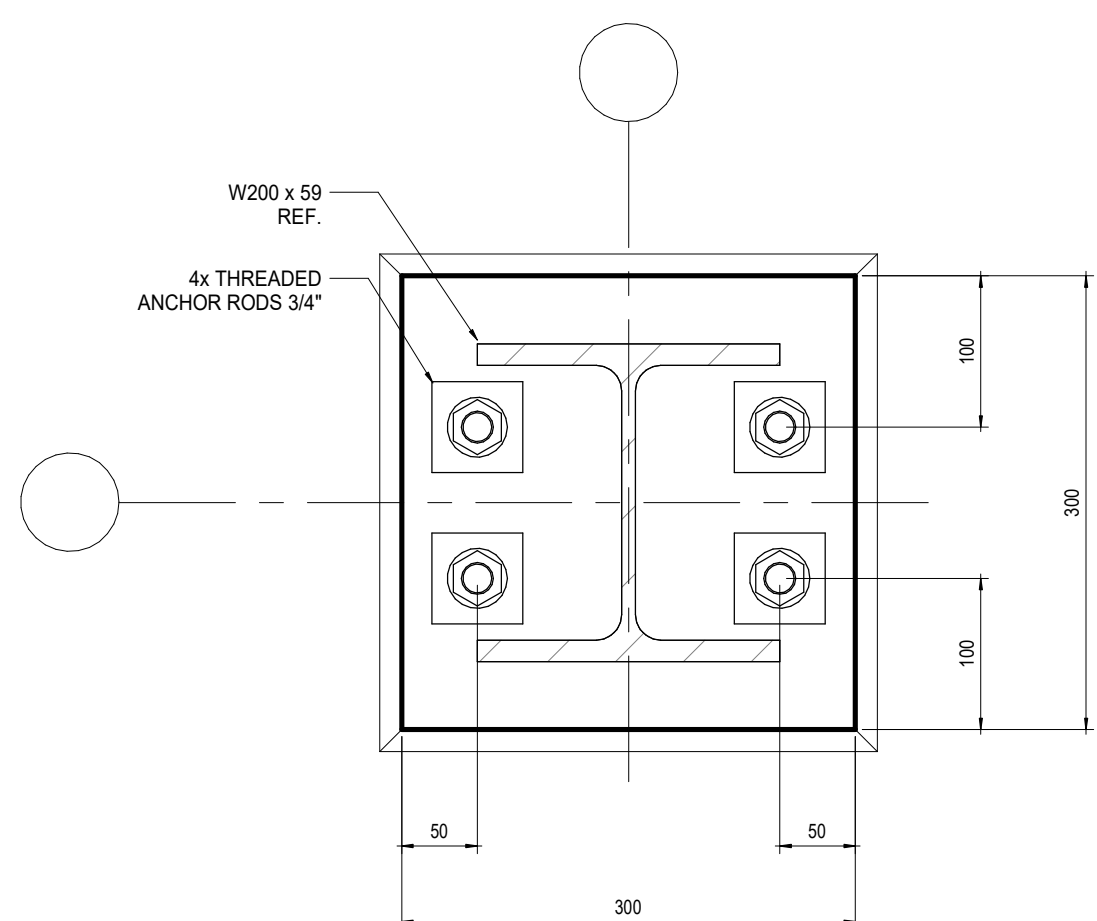


BASE PLATE DETAIL 1-1
1 : 5

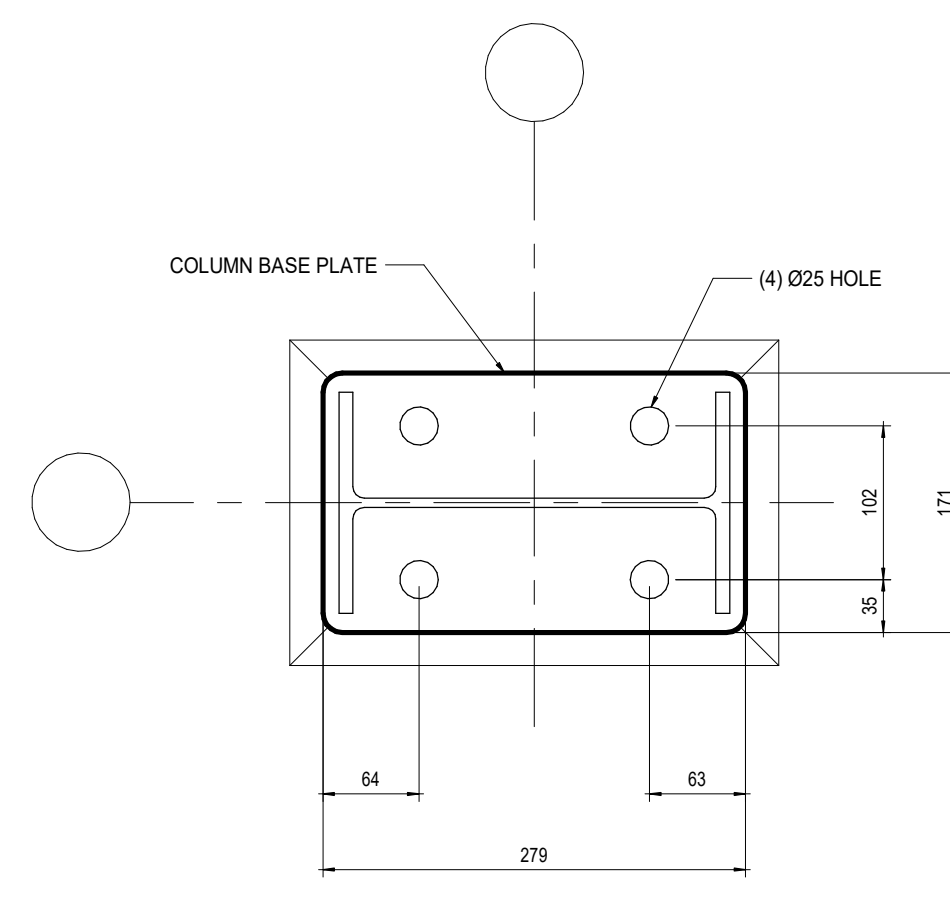

BASE PLATE DETAIL 2-1
1 : 5

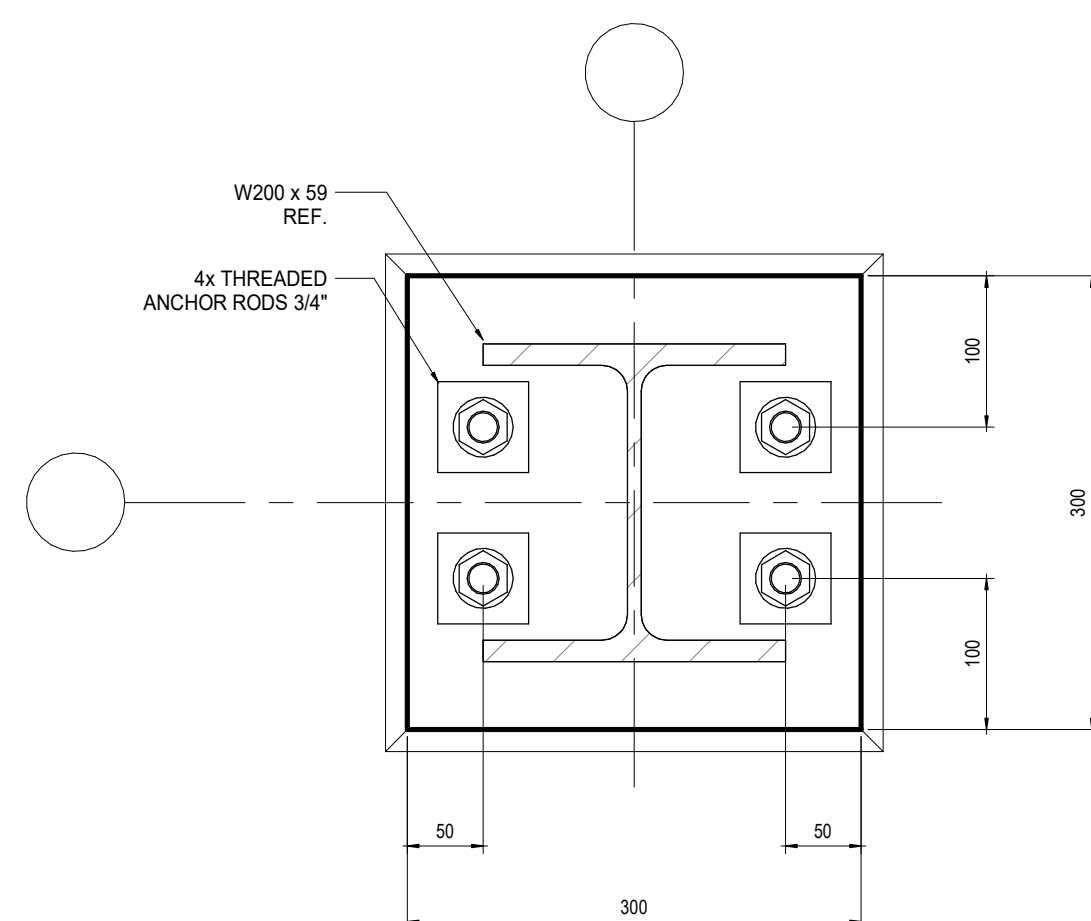

BASE PLATE DETAIL 3-1
1 : 5

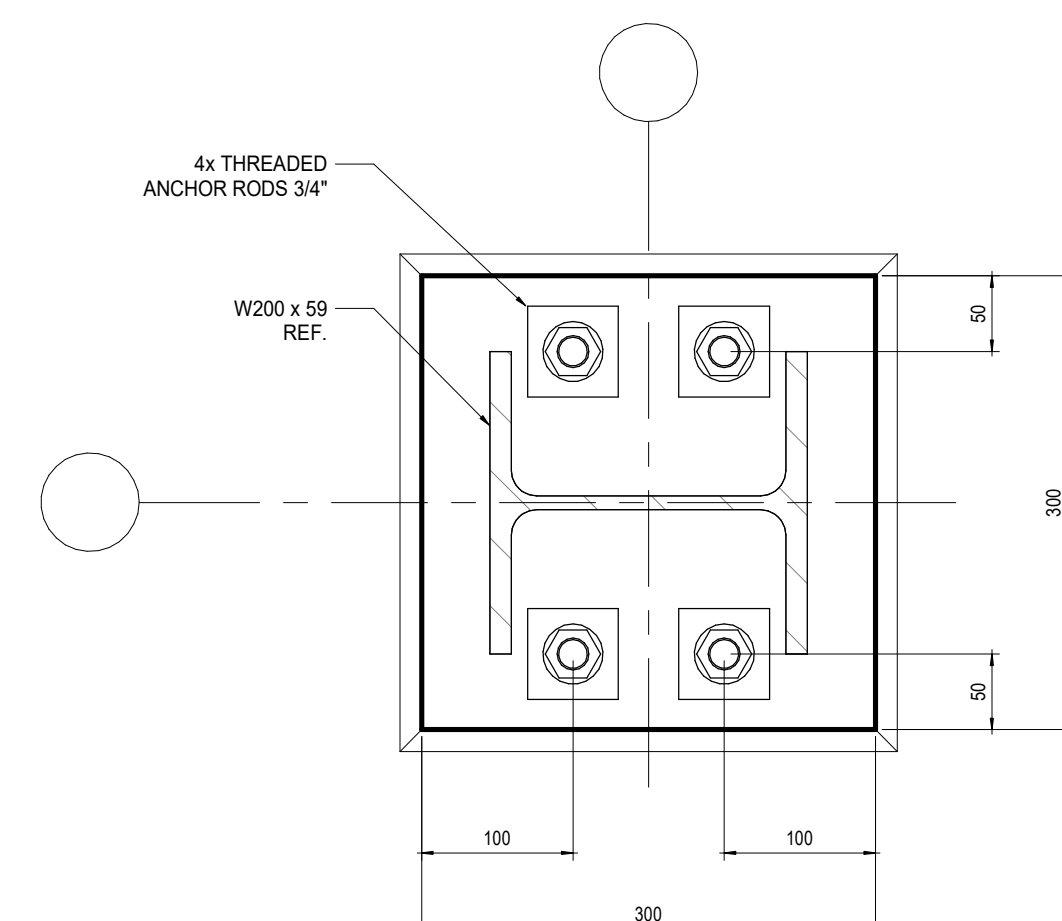

BASE PLATE DETAIL 4-1
1 : 5

ARCHITECT / CONSULTANTS

CONTRACTOR SHALL CHECK ALL DIMENSIONS ON THE WORK AND REPORT ANY DISCREPANCY TO THE CONSULTANT BEFORE PROCEEDING. THIS DRAWING IS NOT TO BE USED FOR CONSTRUCTION UNLESS AUTHORIZED IN WRITING BY CONSULTANT.

SEAL / SIGNATURE

ISSUED FOR CONSTRUCTION DATE

CLIENT NAME

ALOCON CONCRETE FLOOR FINISHING LTD.

DRAWING TITLE
AGGREGATES PROCESS BUILDING FOUNDATION

EXTERIOR STRUCTURE FOUNDATION PLAN

DESIGNED BY / DRAWN BY RY/FB

SCALE As indicated





DRAWING NUMBER

S202

PROJECT NUMBER 24-060

REVISIONS / ISSUED TO

NO.	DATE	BY
1	ISSUED FOR CLIENT REVIEW 2024-09-17	RY

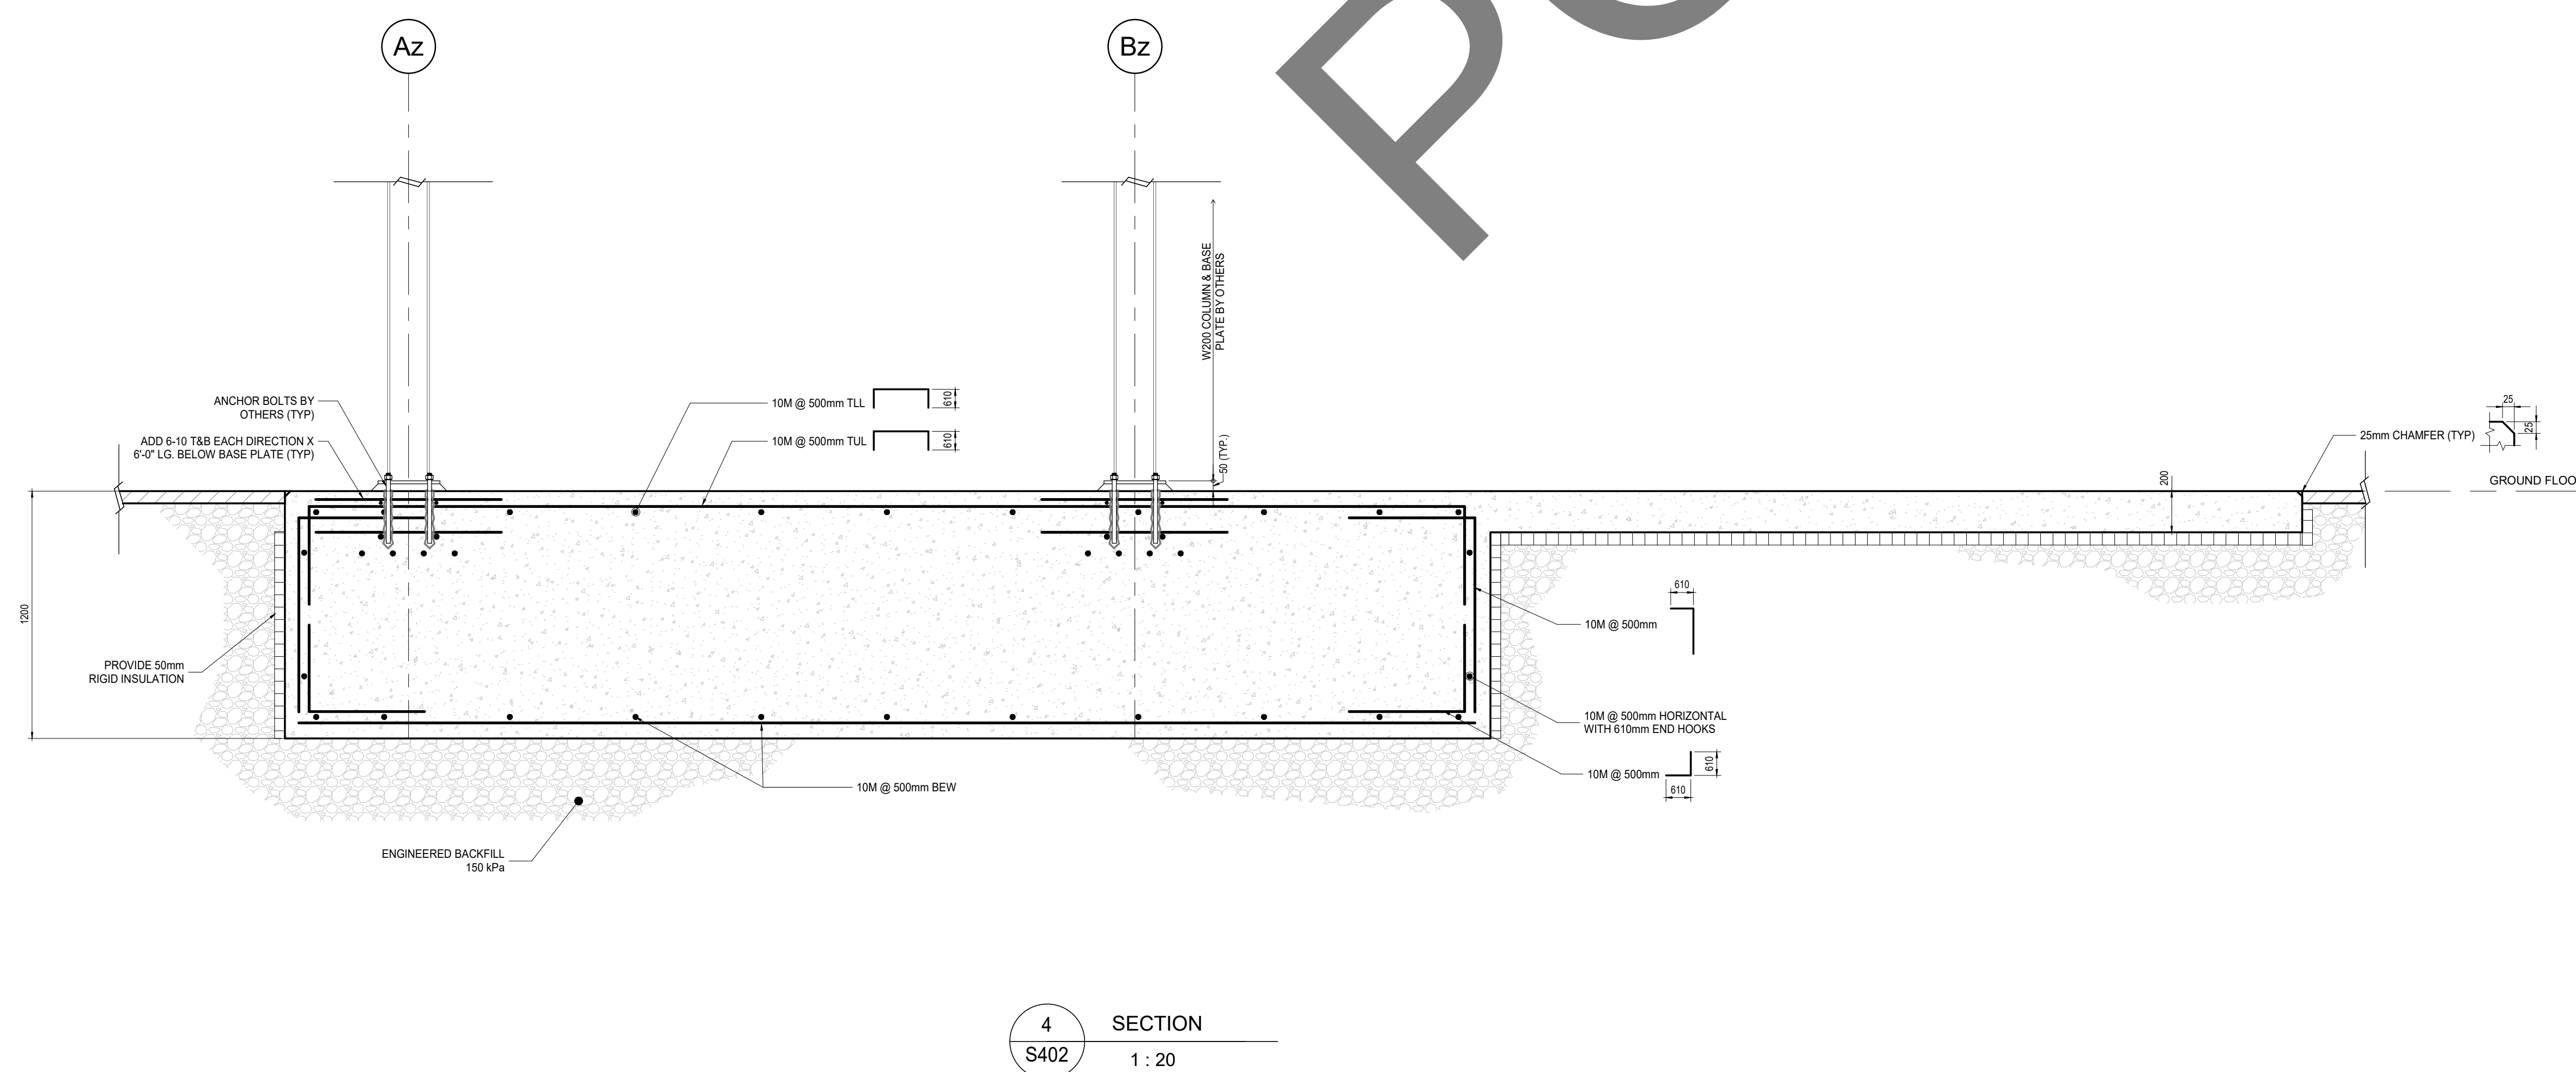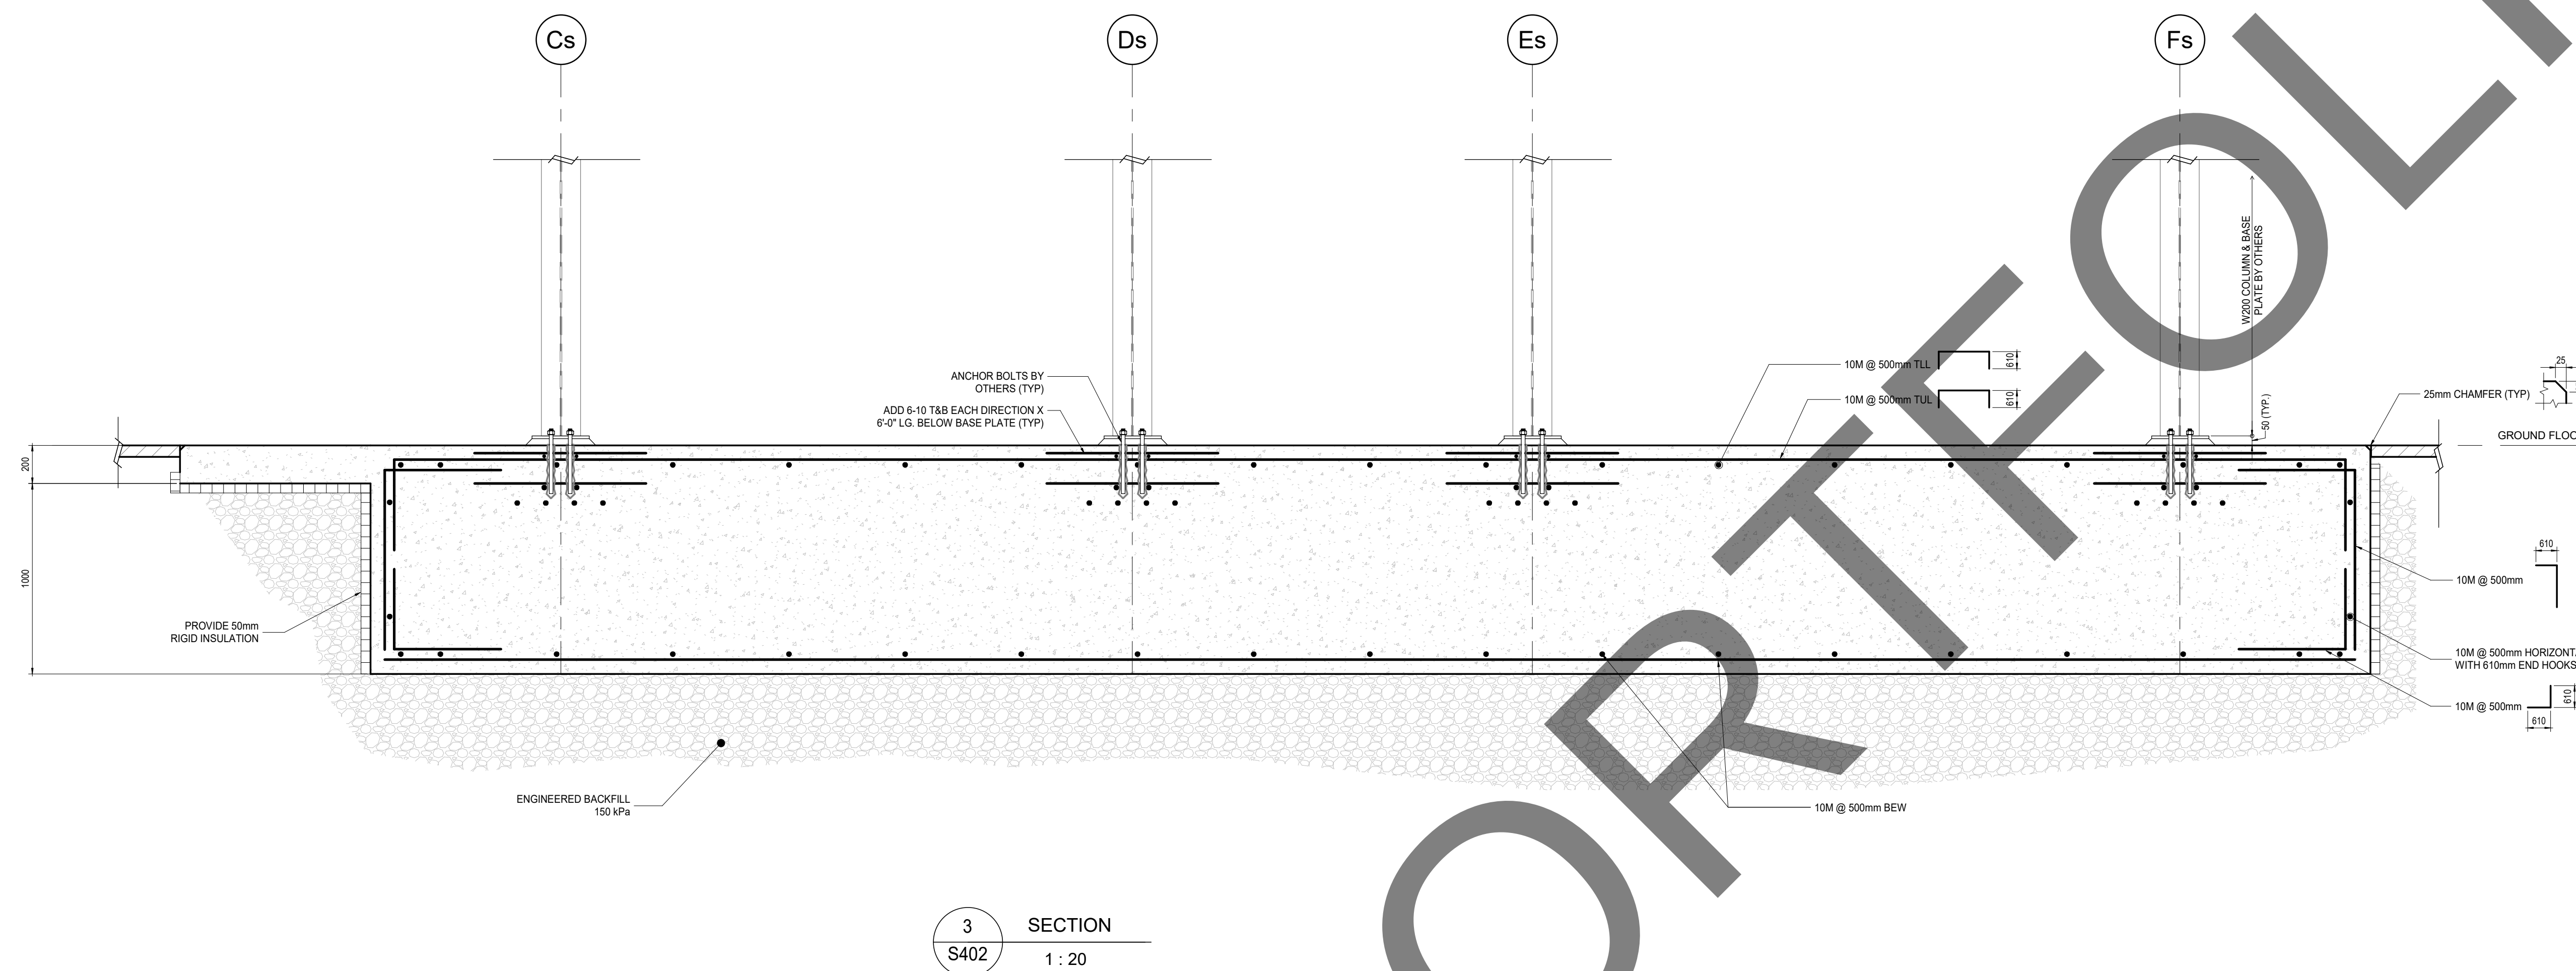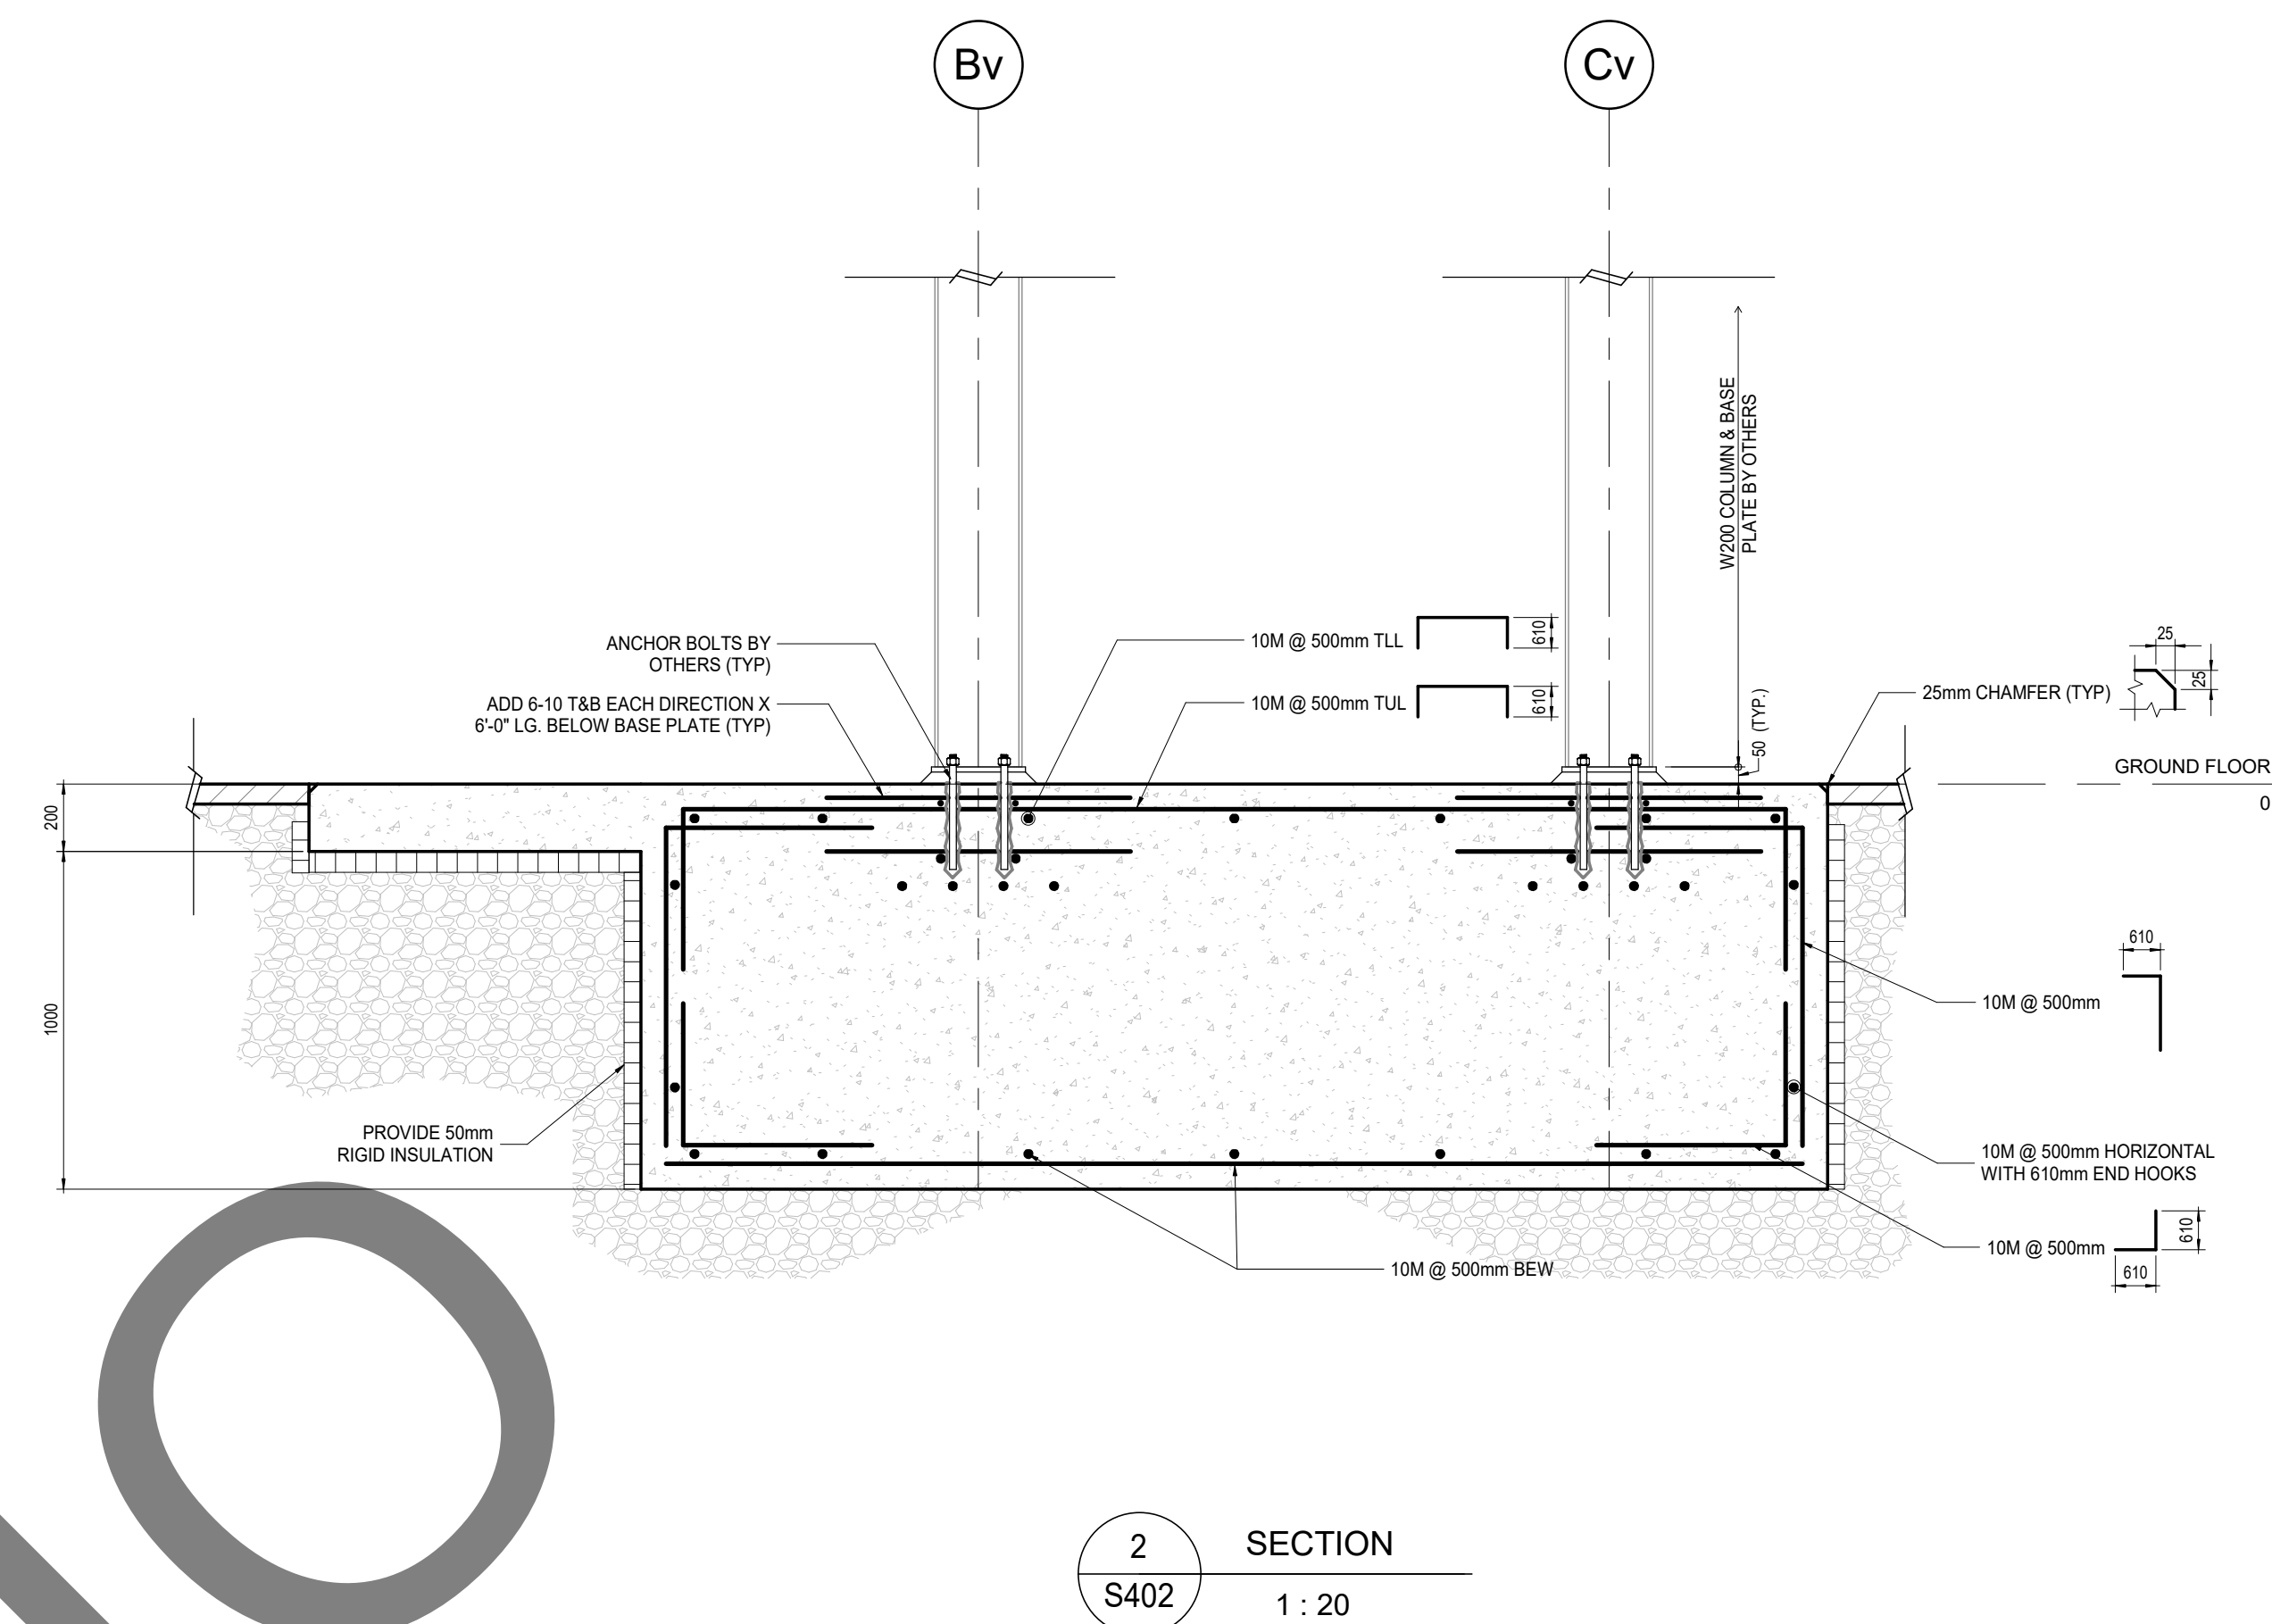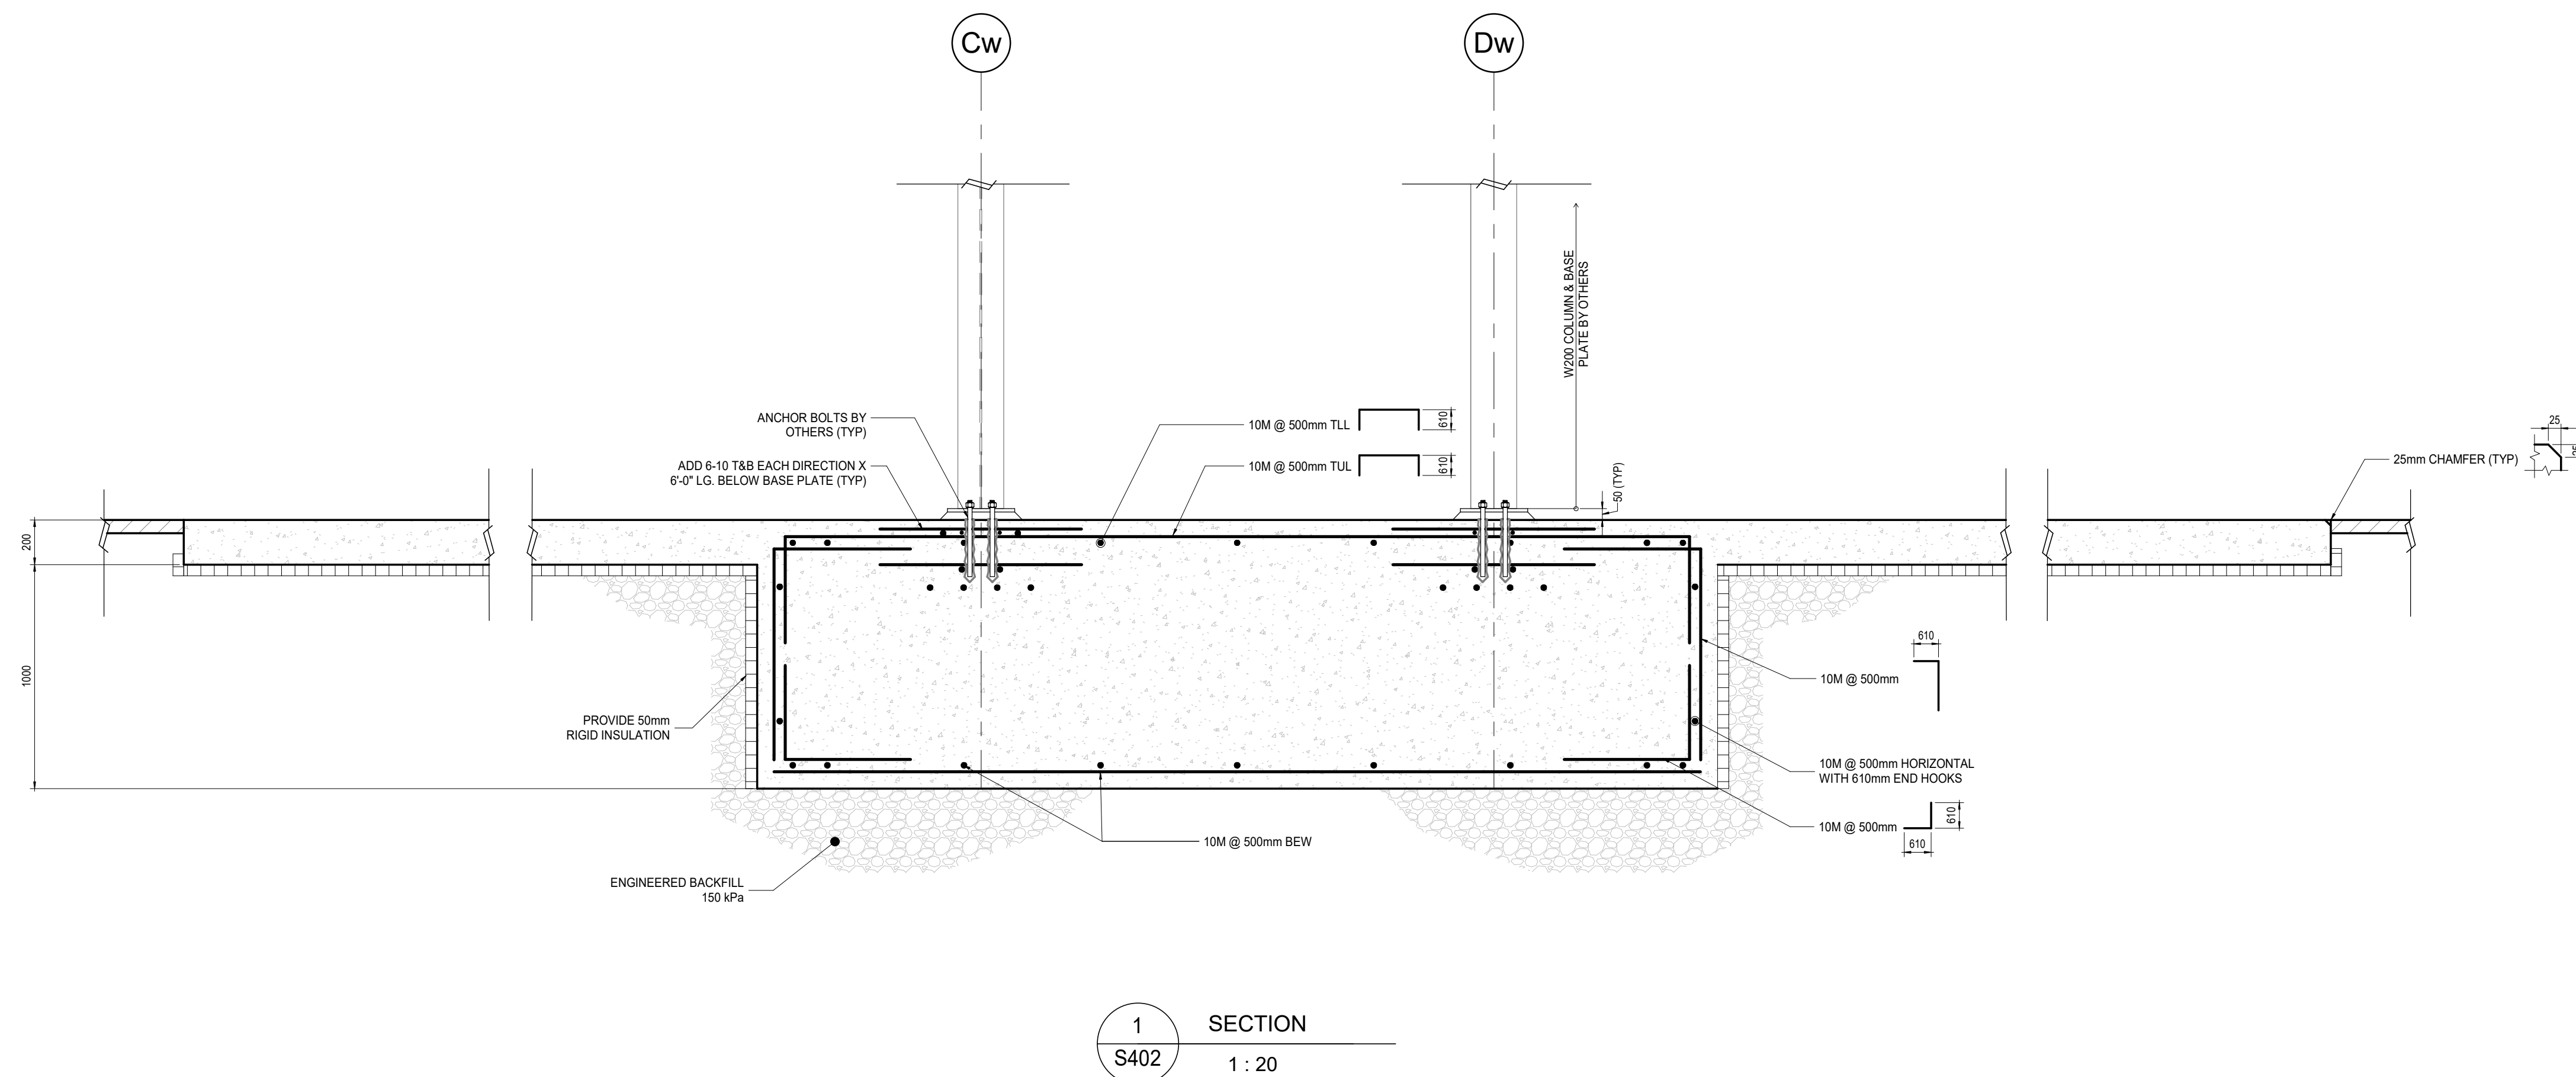

ARCHITECT / CONSULTANTS

CONTRACTOR SHALL CHECK ALL DIMENSIONS ON THE WORK AND REPORT ANY DISCREPANCY TO THE CONSULTANT BEFORE PROCEEDING. THIS DRAWING IS NOT TO BE USED FOR CONSTRUCTION UNLESS AUTHORIZED IN WRITING BY CONSULTANT.

SEAL / SIGNATURE

ISSUED FOR CONSTRUCTION

DATE

CLIENT NAME

ALOCON CONCRETE
FLOOR FINISHING
LTD.

DRAWING TITLE
AGGREGATES
PROCESS BUILDING
FOUNDATION

EXTERIOR STRUCTURE
FOUNDATION SECTIONS

DESIGNED BY / DRAWN BY

RY/FB

SCALE

1 : 20

DRAWING NUMBER

S402

PROJECT NUMBER

24-060