


G:\shared_drives\Project Drafting\24-49450 ODA Drafting 23-229 Dunkirk Self Storage\Working File\Bldg A\23-229 Dunkirk Self Storage R23_Structure bldg A 20260106 JC23-229 Dunkirk Self Storage R25_Building A.rvt

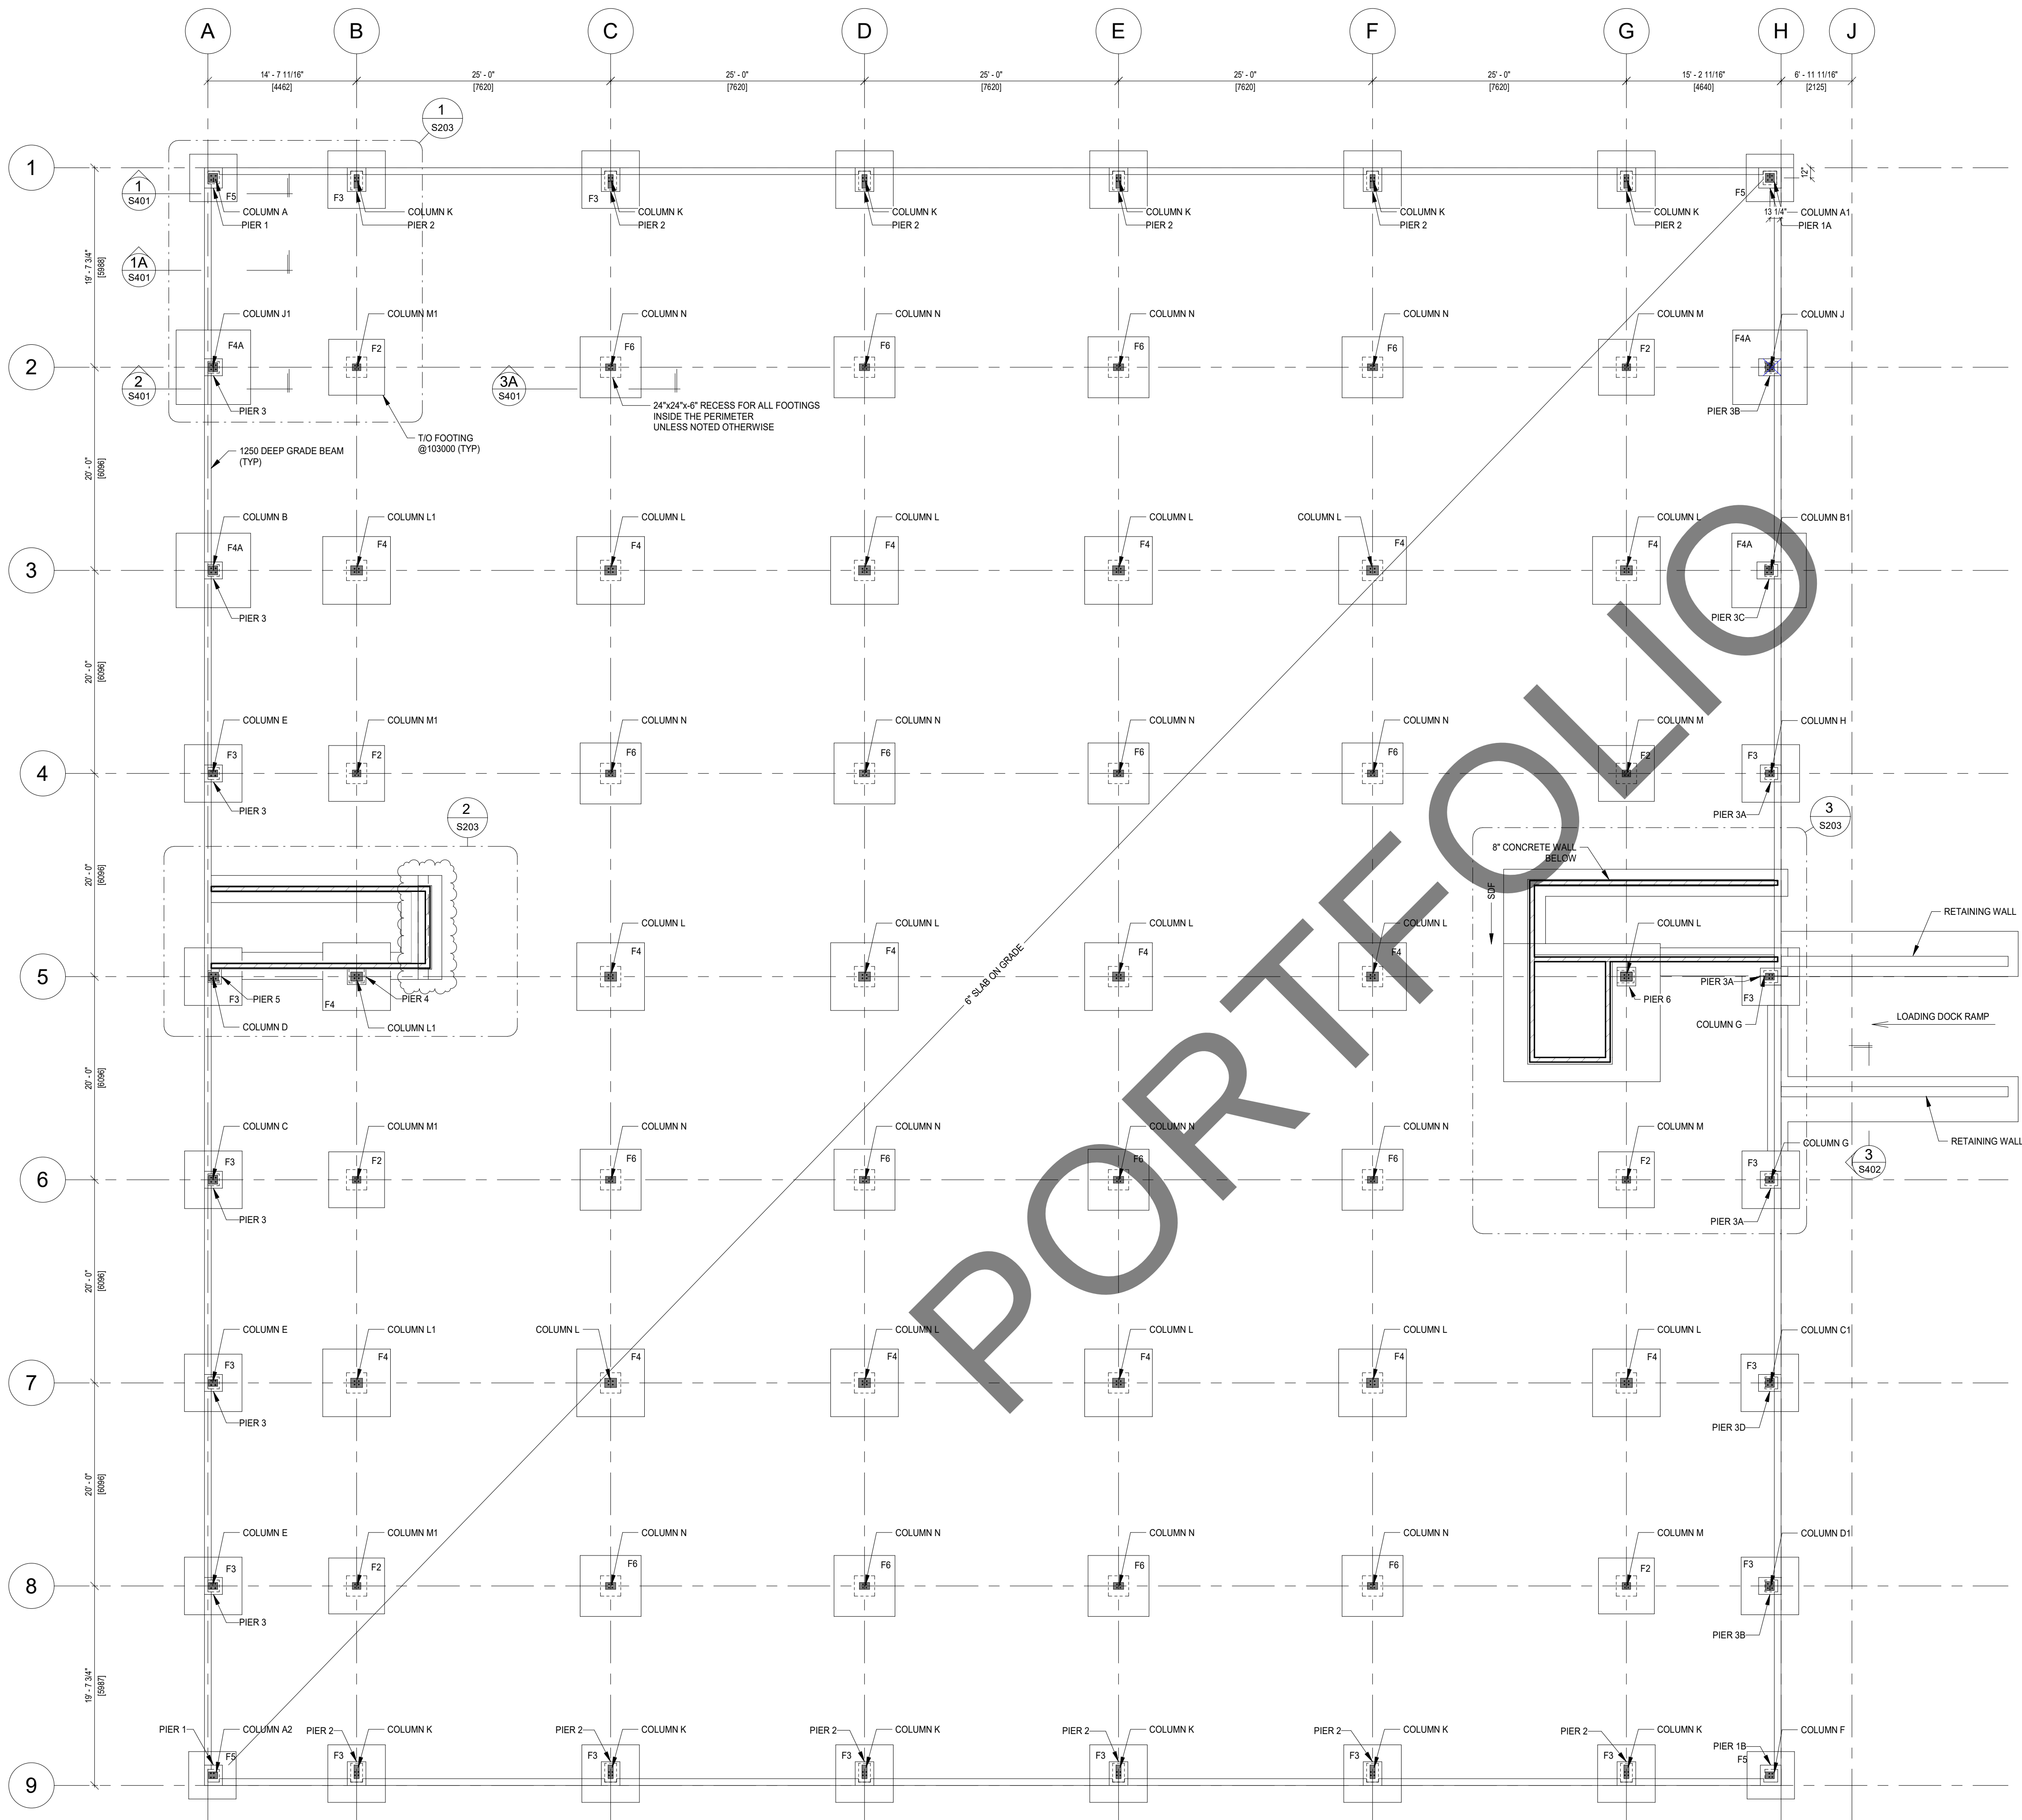

1 1ST FLOOR LEVEL
S201A/ 1 : 100

- NOTES:
- SLAB ON GRADE ELEVATION IS 0.0 ± (DATUM). PLACE SLAB ON GRADE ON MATERIAL CAPABLE OF SUSTAINING 50 kN/m² WITHOUT SETTLEMENT RELATIVE TO THE BUILDING FOUNDATIONS. UNLESS NOTED OTHERWISE, PROVIDE A MINIMUM OF WELDED WIRE FABRIC REINFORCING 15X152MMW16.7/MW16.7.
 - PRE-ENG BUILDING DESIGNED BY METALCOR DATED DECEMBER 13, 2024.
 - FOR ALL PRE-ENG COLUMNS DESIGNED BY METALCOR, BOTTOM OF BASE PLATE IS -5' FROM 0.0 (SLAB ON GRADE).
 - CONCRETE STRENGTH: $f_c = 35$ MPa CLASS F-2 FOR FOOTINGS, PIERS & CURB ALONG GRIDLINES A, H, 1 AND 9. $f_c = 30$ MPa CLASS N FOR ALL OTHER INTERIOR CONCRETE INCLUDING CONCRETE FOOTINGS AND SLAB ON GRADE. U-FILL CONCRETE $f_c = 5$ MPa.
 - ALL REINFORCING STEEL TO CONFORM TO CSA G30.18-21 WITH MIN. YIELD STRENGTH $f_y = 400$ MPa.
 - ALL FOOTINGS TO BE FOUNDED ON THE UNDISRUPTED SOIL WITH CAPACITY OF 200 kPa (SL). REFER TO GEOTECHNICAL REPORT (NT22241) BY NTL DATED NOVEMBER 22, 2022. THE SOIL CAPACITY SHALL BE INSPECTED AND CERTIFIED IN WRITING BY A QUALIFIED GEOTECHNICAL ENGINEER BEFORE ANY CONCRETE IS POURED. FOOTINGS TO BE FOUNDED ON UNDISTURBED SOIL AND INSPECTED BY THE GEOTECHNICAL ENGINEER PRIOR TO CASTING CONCRETE.
 - REMOVE ALL BACKFILL AND ENSURE ALL FOOTINGS ARE FOUNDED ON UNDISTURBED SOIL WITH A MIN. 200 kPa (SL) CAPACITY. THE GEOTECHNICAL ENGINEER MUST VERIFY THIS ON SITE PRIOR TO CONCRETE POURING. U-FILL CONCRETE CAN BE USED IF THE UNDISTURBED SOIL ELEVATION IS LOWER THAN THE BOTTOM OF THE CONCRETE FOOTING.
 - PLACE SLAB ON GRADE ON MINIMUM 6" THICK GRANULAR A MATERIAL AND COMPACTED TO 100% OF ITS STANDARD PROCTOR MAXIMUM DRY DENSITY.
 - ALL SUBGRADE MUST BE INSPECTED BY A GEOTECHNICAL ENGINEER PRIOR TO POURING CONCRETE.

1	Issued for Permit	2024-11-14
2	Issued for Update	2025-01-26
3	Re-Issued for Permit	2025-01-29
4	Issued for Construction	2025-03-21
5	Issued for Update	2025-06-11
6	Issued for Update	2025-06-26
7	Issued for Stairwell Remedial Work	2026-01-07
NO.	REVISIONS	DATE



Quinn Dressel
ASSOCIATES
CONSULTING STRUCTURAL ENGINEERS

RAIMONDO
+ ASSOCIATES
ARCHITECTS INC.



4687 Queen Street Suite 2,
Niagara Falls, ON, L2E 2L9
T | 905-357-4441
F | 905-357-9203
W | www.raimondooarchitects.com
E | mail@raimondooarchitects.com

CLIENT NAME

1000115729 Ontario Limited

PROJECT NAME

Stanley Self Storage

PROJECT ADDRESS

228 Dunkirk Rd, St. Catharines, ON L2R 7K6

SHEET NAME

1ST FLOOR LEVEL -
BUILDING 'A'

DRAWN BY:

LS

DATE:

2026-01-07 11:03:54 AM

SCALE:

1 : 100

PROJECT NO.:

23-229

CHECKED:

RY


DRAWINGS ARE NOT VALID FOR CONSTRUCTION UNTIL SEALED AND SIGNED BY THE ARCHITECT.
DO NOT SCALE DRAWINGS. REPORT ALL DISCREPANCIES TO THE ARCHITECT BEFORE PROCEEDING. ALL DRAWINGS AND DESIGNS REMAIN THE PROPERTY OF THE ARCHITECT, AND ARE PROTECTED UNDER COPYRIGHT.
THESE DESIGN DOCUMENTS ARE PREPARED SOLELY FOR THE USE OF THE PARTY WITH WHOM THE DESIGN PROFESSIONAL HAS ENTERED INTO A CONTRACT AND THERE ARE NO REPRESENTATIONS OF ANY KIND MADE BY THE DESIGN PROFESSIONAL TO ANY PARTY WITH WHOM THE DESIGN PROFESSIONAL HAS NOT ENTERED INTO A CONTRACT.

SHEET #


S201A

REV. #


G:\shand drives\Project Drafting\24-4949D ODA Drafting 23-229 Dunkirk Self Storage\Working File\Bldg A\23-229 Dunkirk Self Storage R23_Structure bldg A 2026\105 JC23-229 Dunkirk Self Storage R25_Building A.rvt

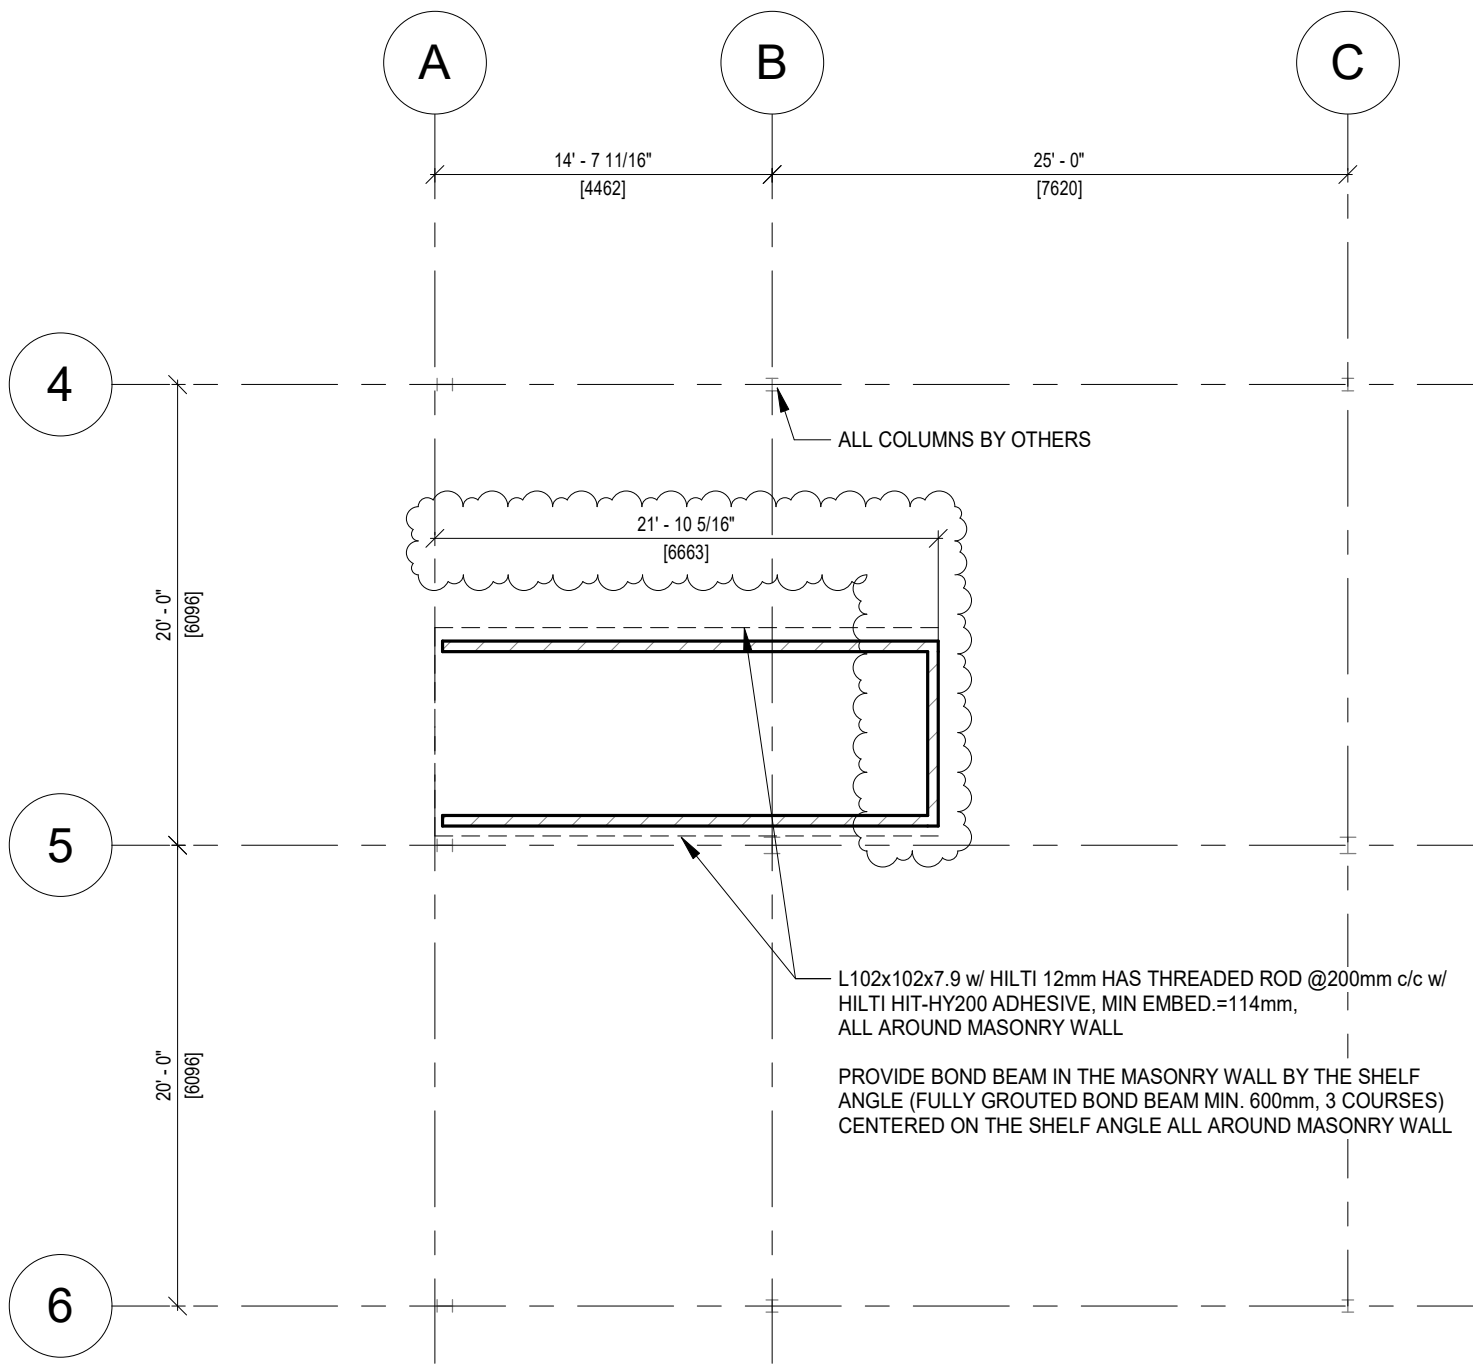


1 2ND FLOOR LEVEL - STAIRWELL B
S202 1 : 100

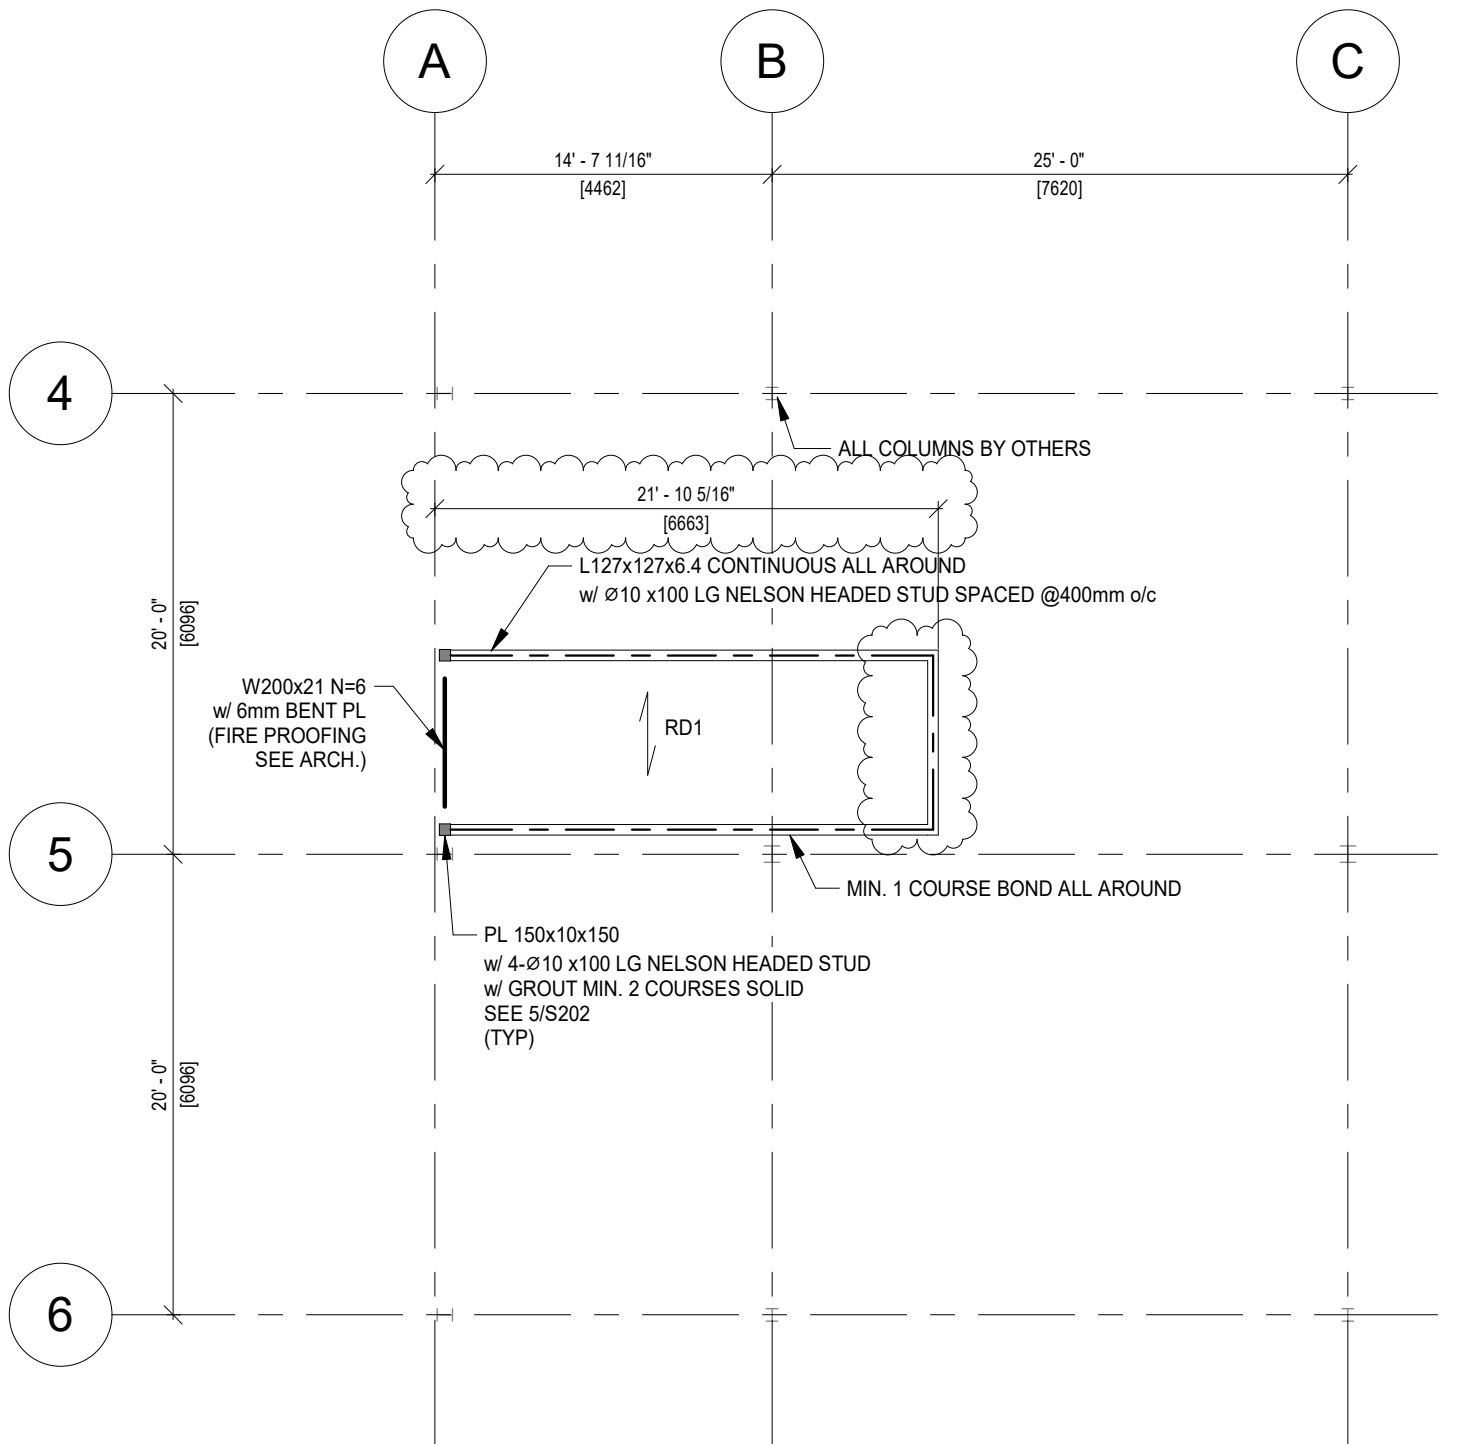





3 ROOF OF STAIRWELL B
S202 1 : 100
NOTE: SEE ARCH. DRAWING FOR TOP ELEVATION

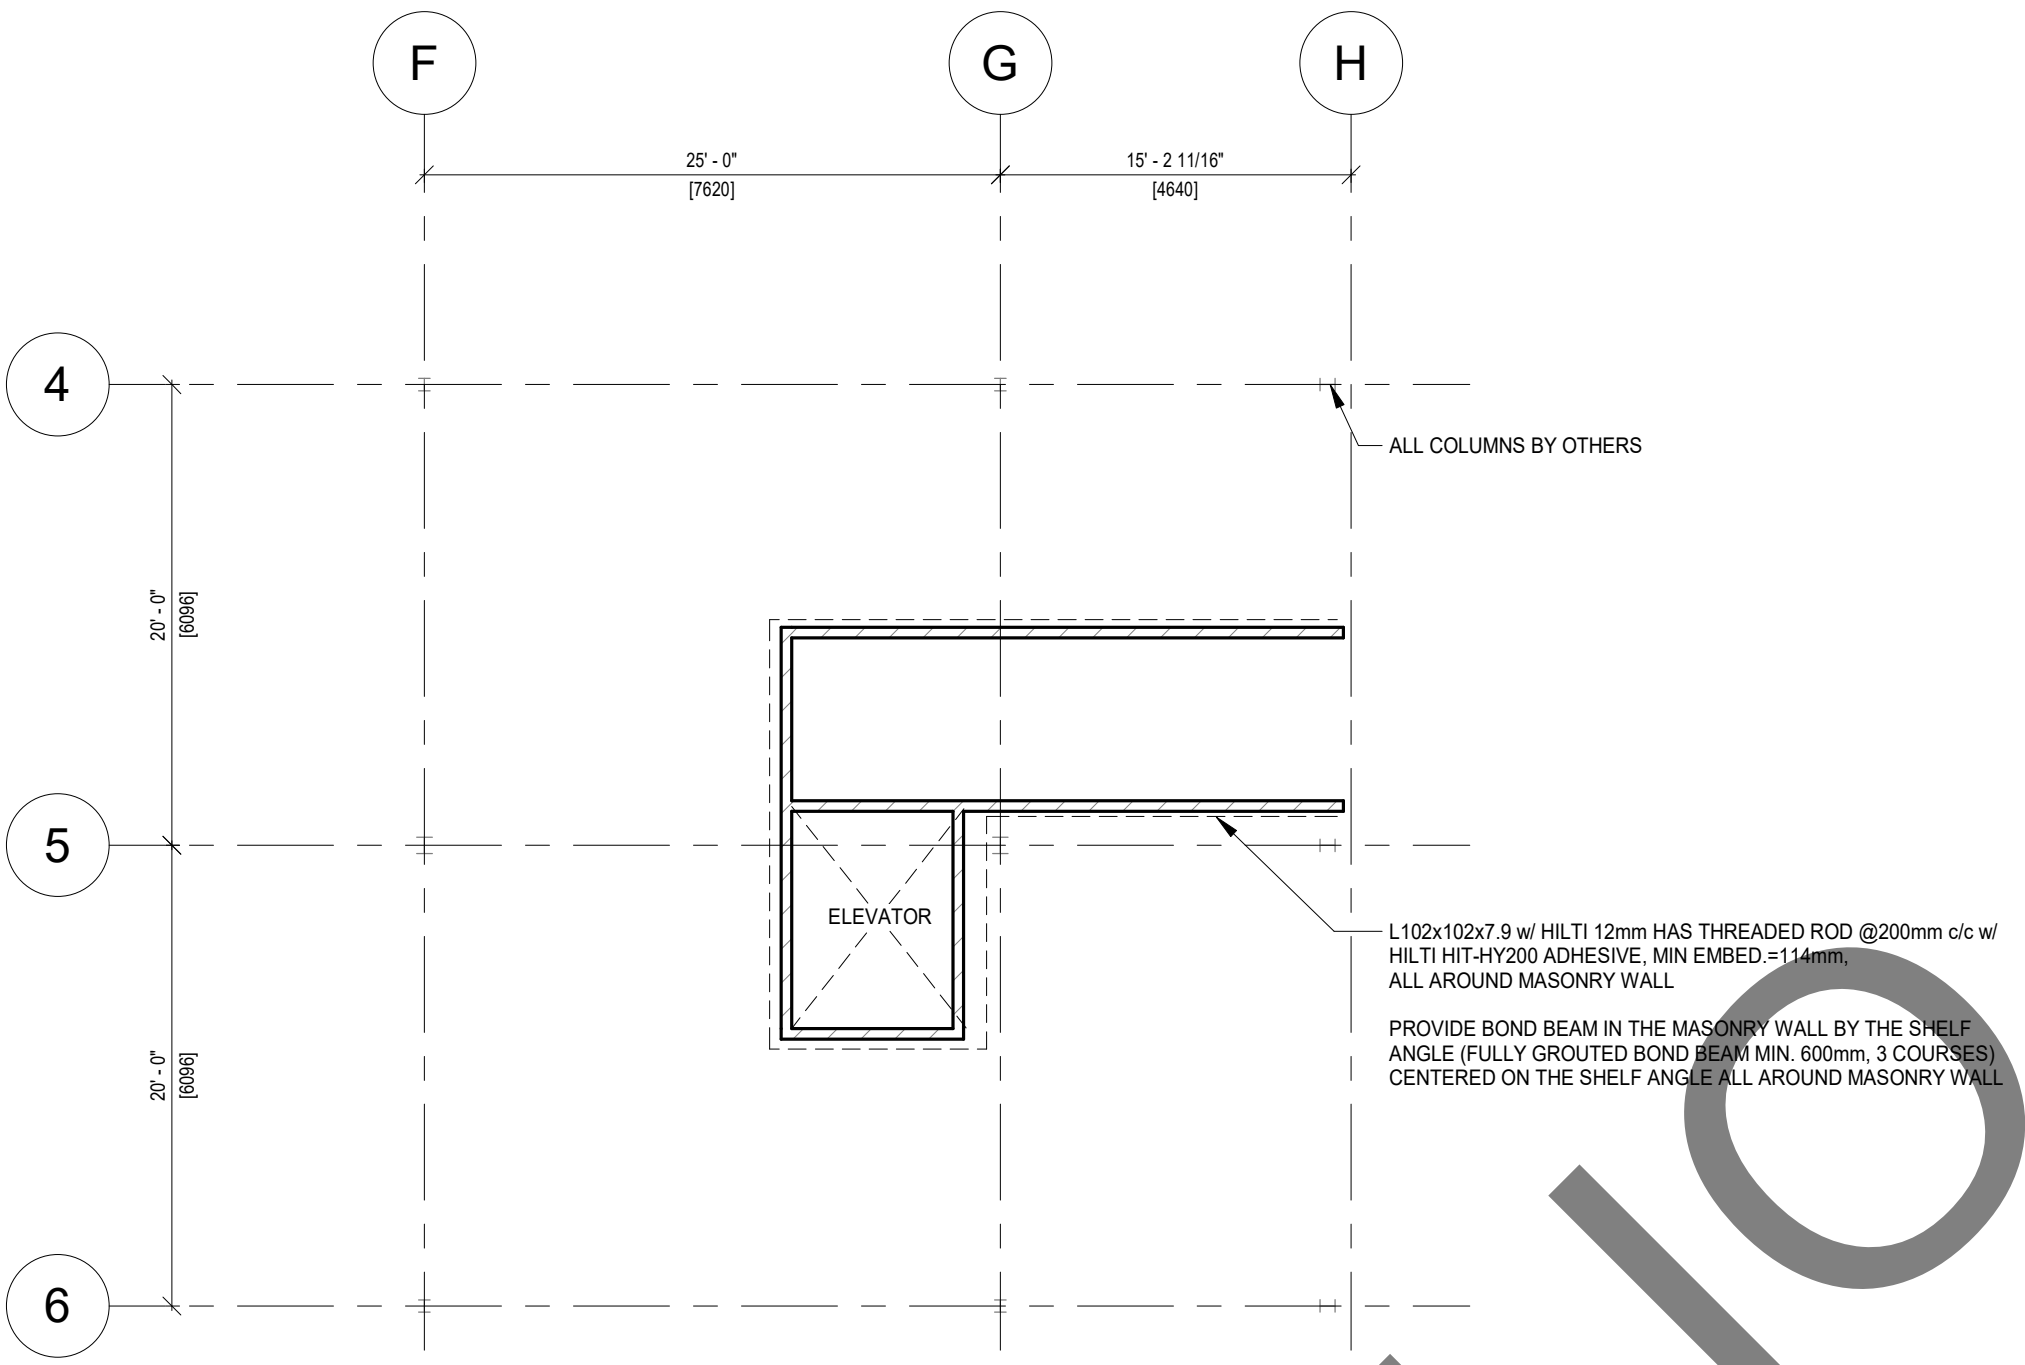

2 2ND FLOOR LEVEL - STAIRWELL A AND ELEVATOR
S202 1 : 100

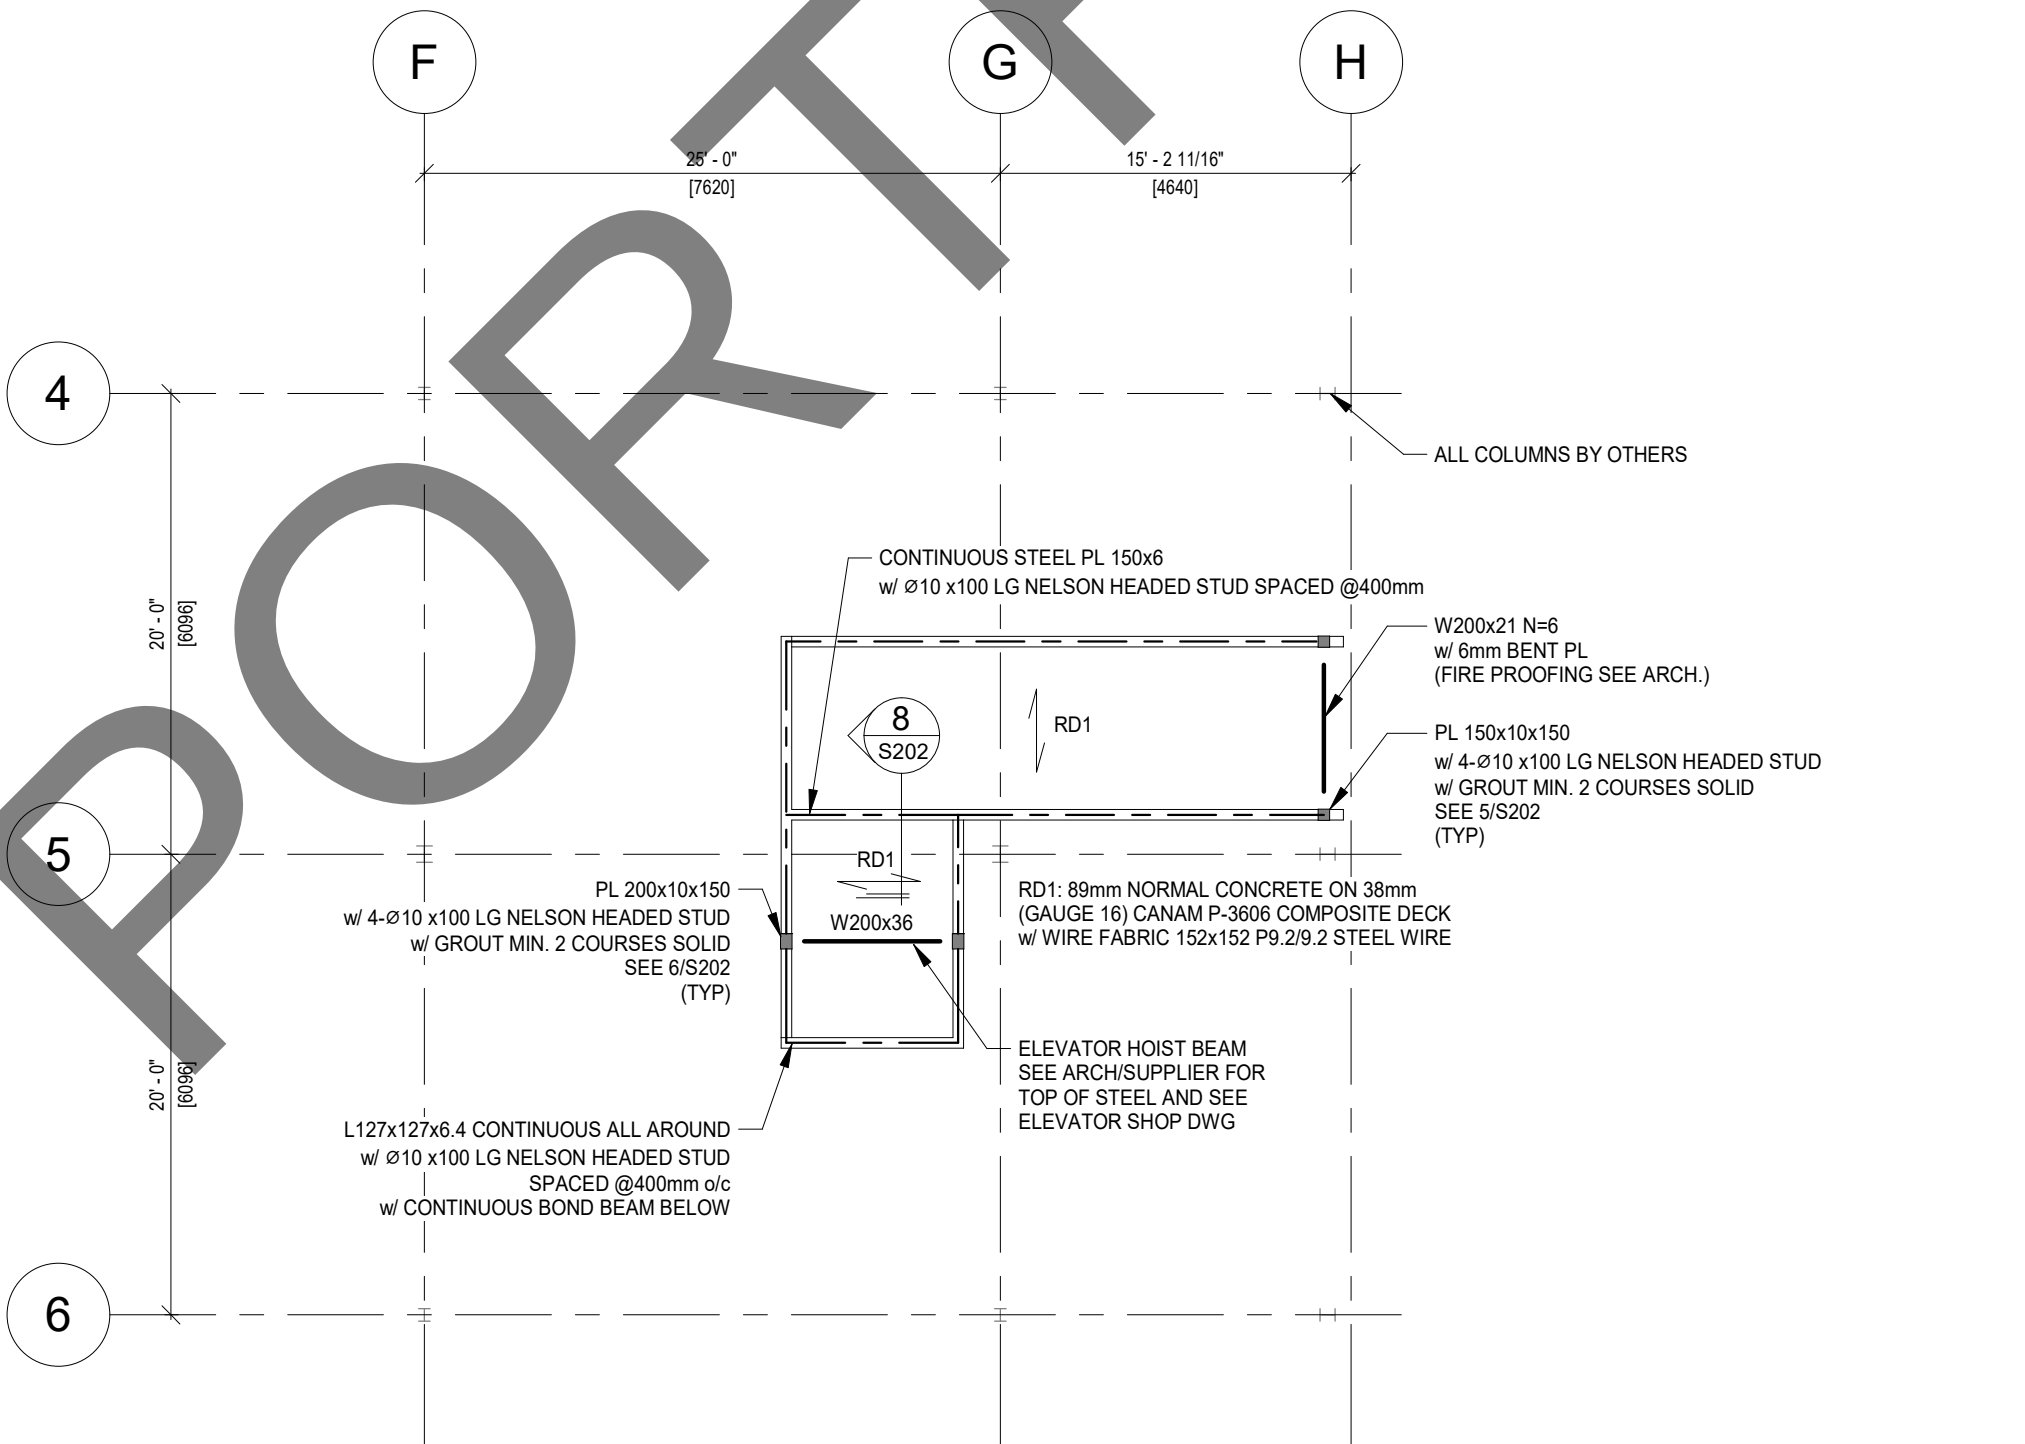

4 ROOF OF STAIRWELL A AND ELEVATOR
S202 1 : 100
NOTE: SEE ARCH. DRAWING FOR TOP ELEVATION

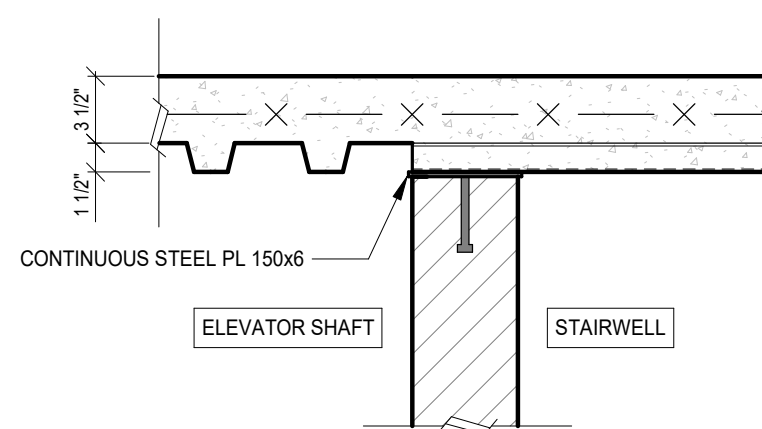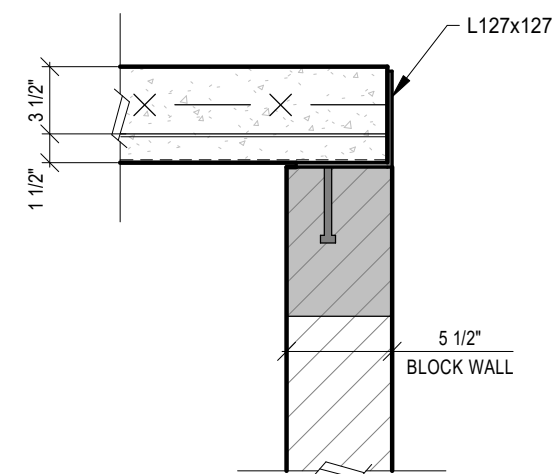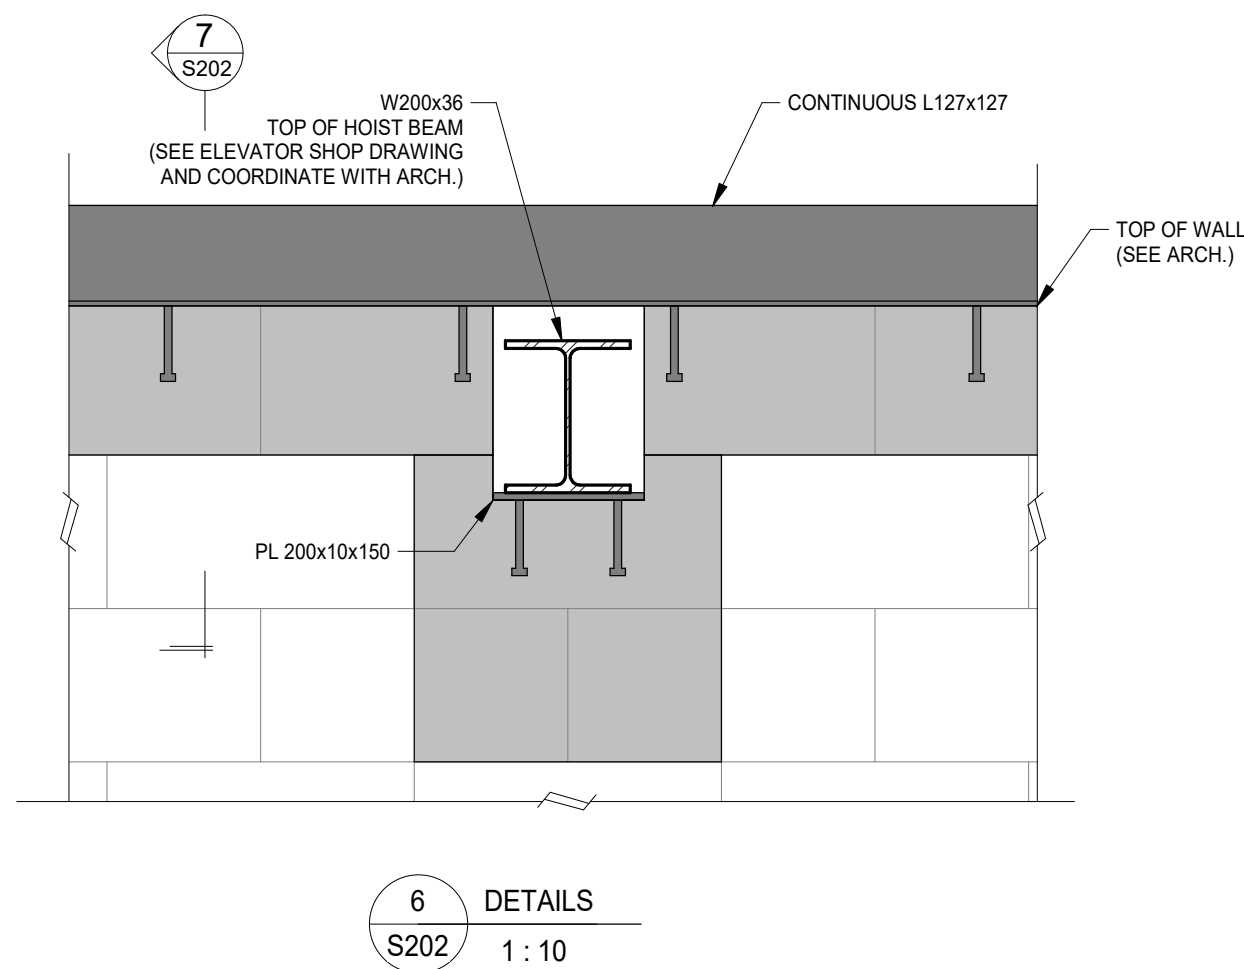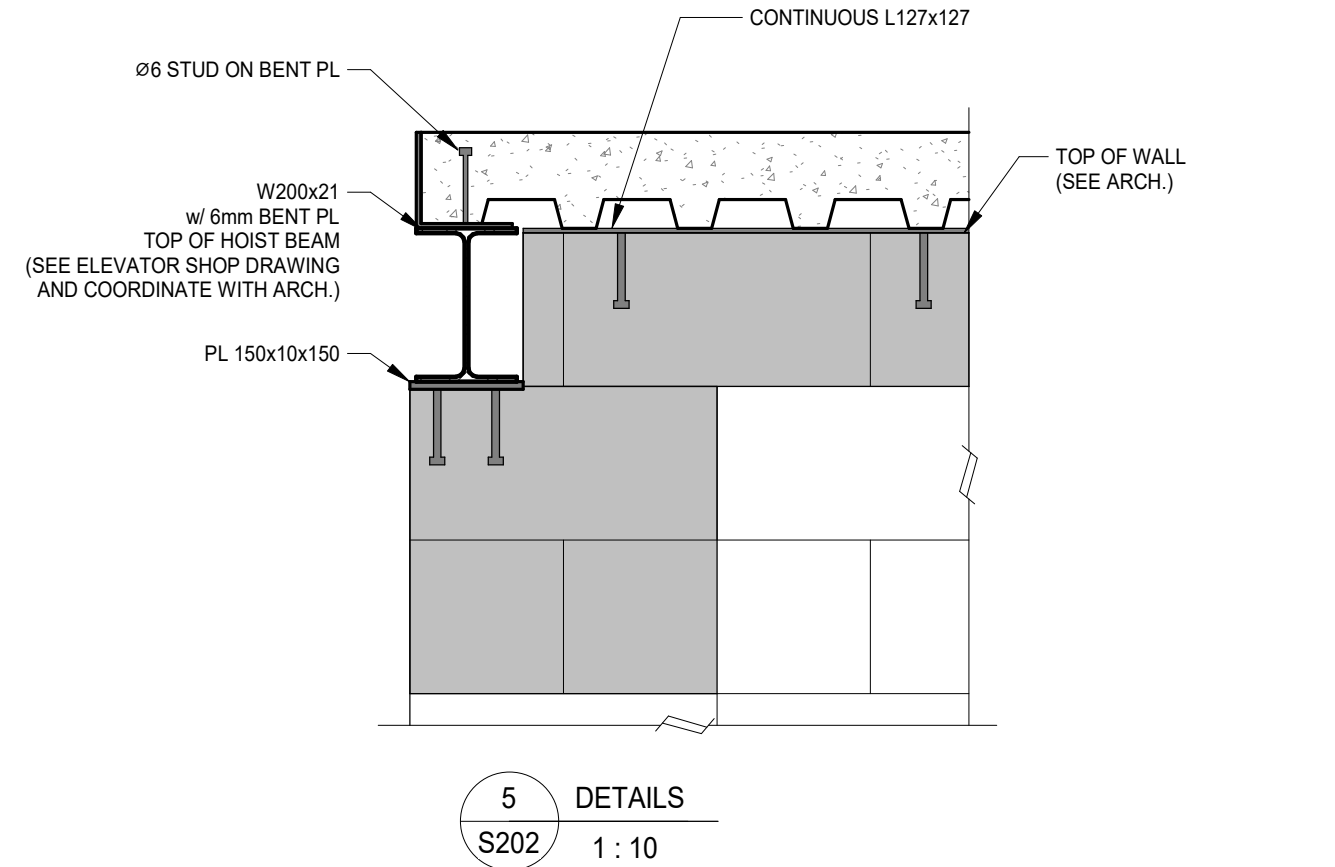

1	Issued for Permit	2024-11-14
2	Issued for Update	2025-01-26
3	Re-Issued for Permit	2025-01-29
4	Issued for Construction	2025-03-21
5	Issued for Update	2025-05-23
6	Issued for Update	2025-06-19
7	Issued for Update	2025-06-26
8	Issued for Update	2025-07-15
9	Issued for Stairwall Remedial Work	2026-01-07
NO.	REVISIONS	DATE



4687 Queen Street Suite 2,
Niagara Falls, ON, L2E 2L9
T | 905-357-4441
F | 905-357-9203
W | www.raidondoarchitects.com
E | mail@raidondoarchitects.com

CLIENT NAME
1000115729 Ontario Limited
PROJECT NAME
Stanley Self Storage

PROJECT ADDRESS
228 Dunkirk Rd, St. Catharines, ON L2R 7K6
SHEET NAME
PART PLANS FOR STAIR A
& B AND ELEVATOR -
BUILDING 'A'

DRAWN BY: LS
DATE: 2026-01-07 11:03:56 AM
SCALE: As Indicated
PROJECT NO.: 23-229
CHECKED: RY


DRAWINGS ARE NOT VALID FOR CONSTRUCTION UNTIL SEALED AND
SIGNED BY THE ARCHITECT.
DO NOT SCALE DRAWINGS. REPORT ALL DISCREPANCIES TO THE
ARCHITECT BEFORE PROCEEDING. ALL DRAWINGS AND DESIGNS
REMAIN THE PROPERTY OF THE ARCHITECT, AND ARE PROTECTED
UNDER COPYRIGHT.
THESE DESIGN DOCUMENTS ARE PREPARED SOLELY FOR THE USE
BY THE PARTY WITH WHOM THE DESIGN PROFESSIONAL HAS
ENTERED INTO A CONTRACT AND THERE ARE NO REPRESENTATIONS
OF ANY KIND MADE BY THE DESIGN PROFESSIONAL TO ANY PARTY
WITH WHOM THE DESIGN PROFESSIONAL HAS NOT ENTERED INTO A
CONTRACT.

SHEET #

S202

REV. #

G:\shand drives\Project Drafting\04-49450 ODA Drafting 23-229 Dunkirk Self Storage\Working File\Bldg A\23-229 Dunkirk Self Storage R23_Structure bldg A 2026\04 JC23-229 Dunkirk Self Storage R25_Building A.rvt

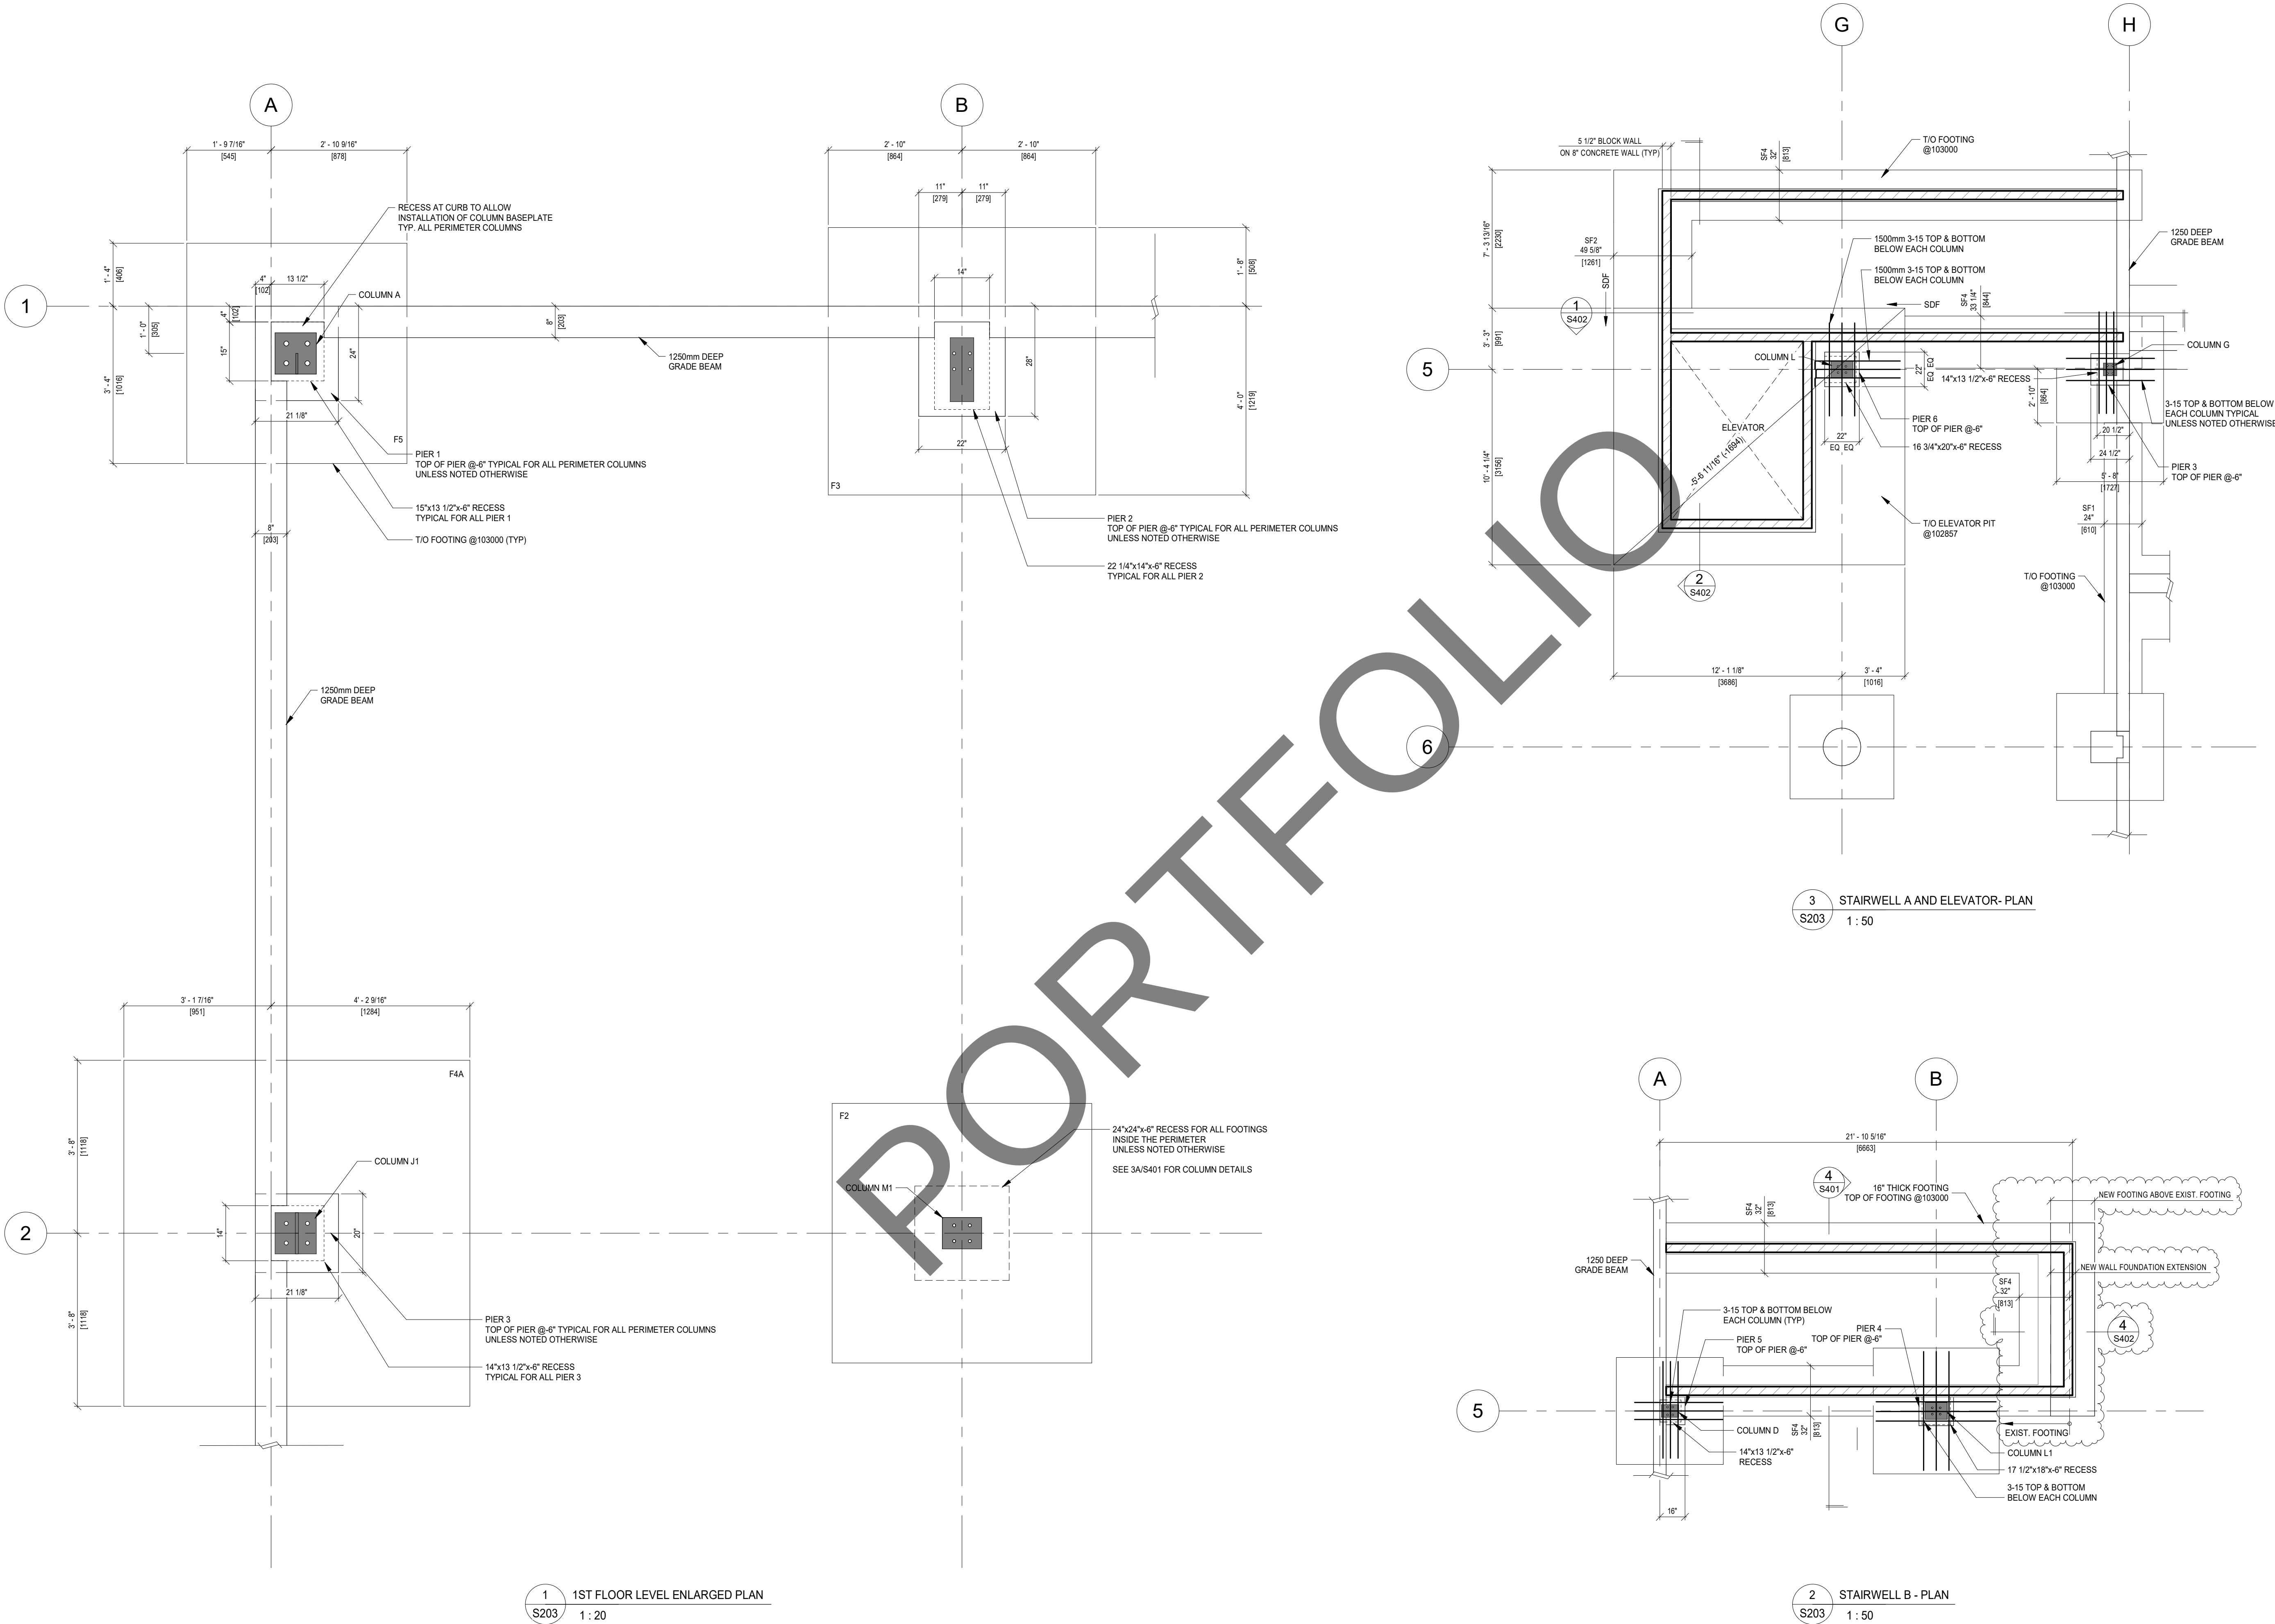

1	Issued for Permit	2024-11-14
2	Issued for Update	2025-01-26
3	Re-issued for Permit	2025-01-26
4	Issued for Construction	2025-03-21
5	Issued for Update	2025-05-23
6	Issued for Update	2025-06-11
7	Issued for Update	2025-06-26
8	Issued for Stairwell Remedial Work	2026-01-07
NO.	REVISIONS	DATE



CLIENT NAME
1000115729 Ontario Limited
PROJECT NAME
Stanley Self Storage

PROJECT ADDRESS
228 Dunkirk Rd, St. Catharines, ON L2R 7K6
SHEET NAME
ENLARGED FLOOR
PLANS - BUILDING 'A'

DRAWN BY: LS
DATE: 2026-01-07 11:03:56 AM
SCALE: As Indicated
PROJECT NO.: 23-229
CHECKED: RY

DRAWINGS ARE NOT VALID FOR CONSTRUCTION UNTIL SEALED AND SIGNED BY THE ARCHITECT.
DO NOT SCALE DRAWINGS. REPORT ALL DISCREPANCIES TO THE ARCHITECT BEFORE PROCEEDING. ALL DRAWINGS AND DESIGNS REMAIN THE PROPERTY OF THE ARCHITECT, AND ARE PROTECTED UNDER COPYRIGHT.


THESE DESIGN DOCUMENTS ARE PREPARED SOLELY FOR THE USE BY THE PARTY WITH WHOM THE DESIGN PROFESSIONAL HAS ENTERED INTO A CONTRACT AND THERE ARE NO REPRESENTATIONS OF ANY KIND MADE BY THE DESIGN PROFESSIONAL TO ANY PARTY WITH WHOM THE DESIGN PROFESSIONAL HAS NOT ENTERED INTO A CONTRACT.

SHEET #

S203

REV. #

G:\shand drives\Project Drafting\24-4945D ODA Drafting 23-229 Dunkirk Self Storage\Working File\Bldg A\23-229 Dunkirk Self Storage R23_Structure bldg A 2026\105 JC23-229 Dunkirk Self Storage R25_Building A.rvt

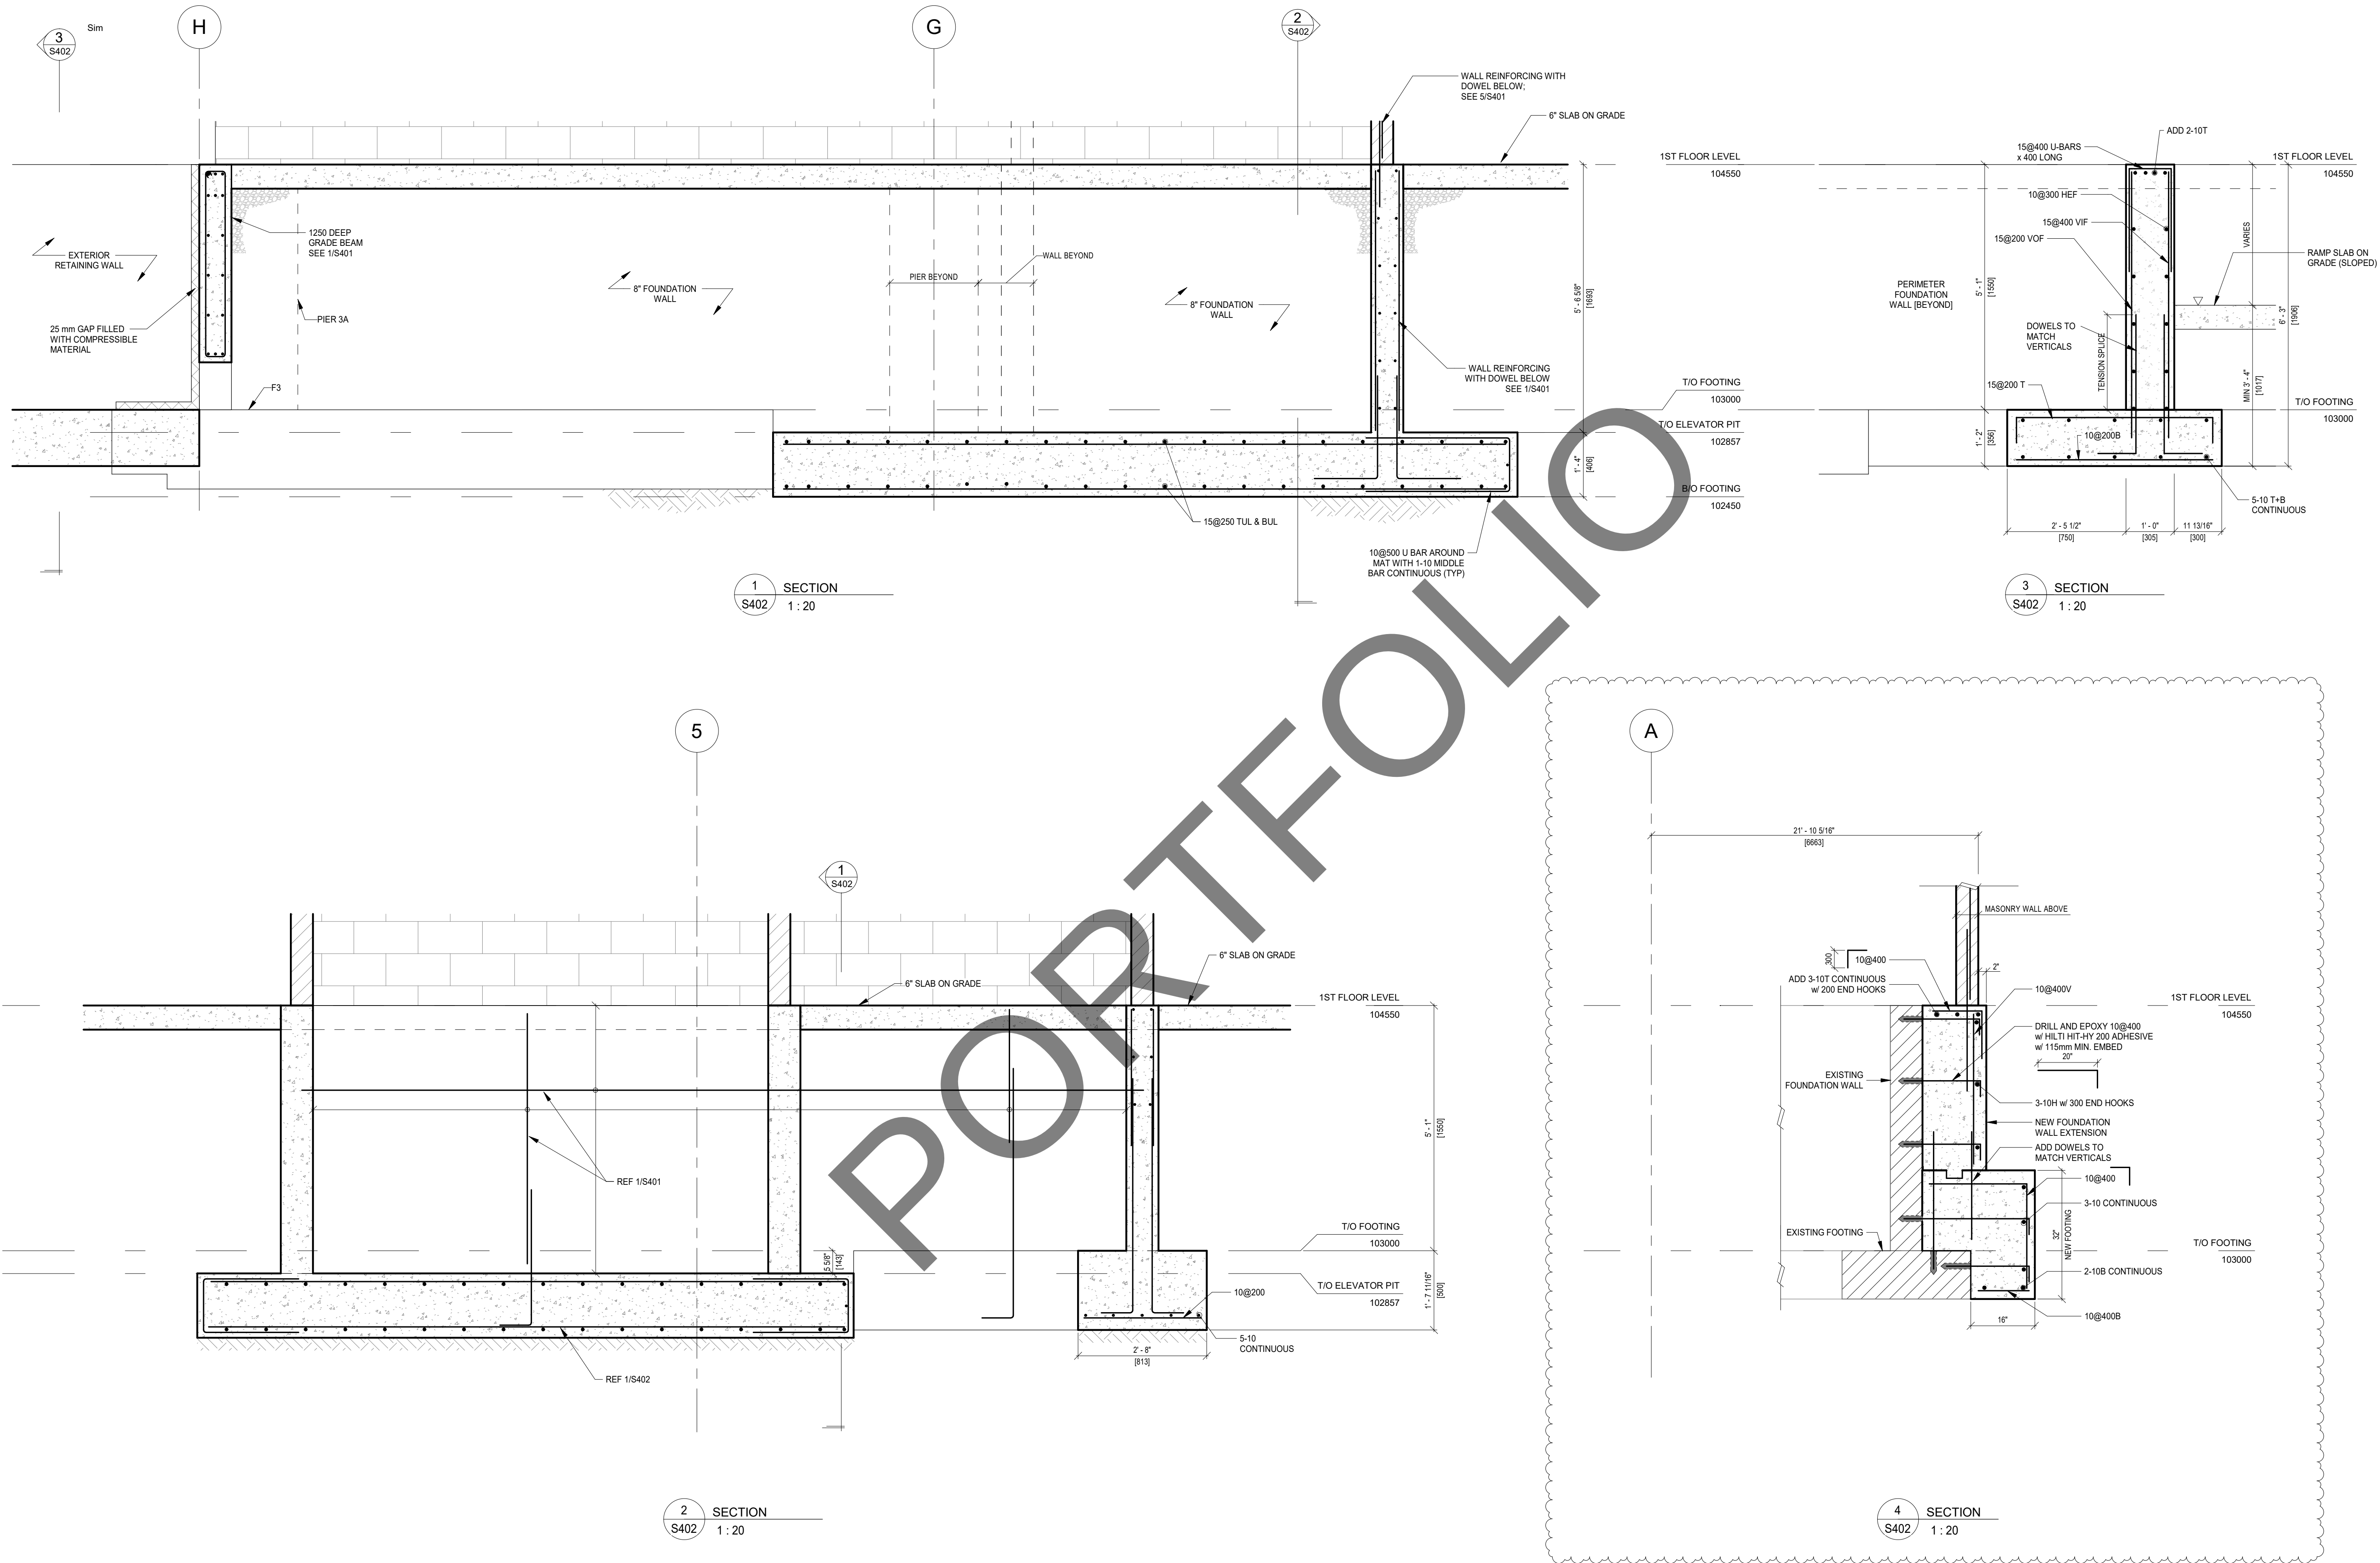

1	Issued for Permit	2024-11-14
2	Issued for Update	2025-01-26
3	Re-issued for Permit	2025-01-26
4	Issued for Construction	2025-03-21
5	Issued for Update	2025-05-23
6	Issued for Update	2025-06-11
7	Issued for Update	2025-06-26
8	Issued for Stairwell Remedial Work	2026-01-07
NO.	REVISIONS	DATE



CLIENT NAME
1000115729 Ontario Limited
PROJECT NAME
Stanley Self Storage

PROJECT ADDRESS
228 Dunkirk Rd, St. Catharines, ON L2R 7K6
SHEET NAME
SECTIONS - BUILDING 'A'

DRAWN BY: LS
DATE: 2026-01-07 11:03:57 AM
SCALE: 1:20
PROJECT NO.: 23-229
CHECKED: RY

DRAWINGS ARE NOT VALID FOR CONSTRUCTION UNTIL SEALED AND SIGNED BY THE ARCHITECT.
DO NOT SCALE DRAWINGS. REPORT ALL DISCREPANCIES TO THE ARCHITECT BEFORE PROCEEDING. ALL DRAWINGS AND DESIGNS REMAIN THE PROPERTY OF THE ARCHITECT, AND ARE PROTECTED UNDER COPYRIGHT.
THESE DESIGN DOCUMENTS ARE PREPARED SOLELY FOR THE USE BY THE PARTY WITH WHOM THE DESIGN PROFESSIONAL HAS ENTERED INTO A CONTRACT AND THERE ARE NO REPRESENTATIONS OF ANY KIND MADE BY THE DESIGN PROFESSIONAL TO ANY PARTY WITH WHOM THE DESIGN PROFESSIONAL HAS NOT ENTERED INTO A CONTRACT.

SHEET #

S402

REV. #