
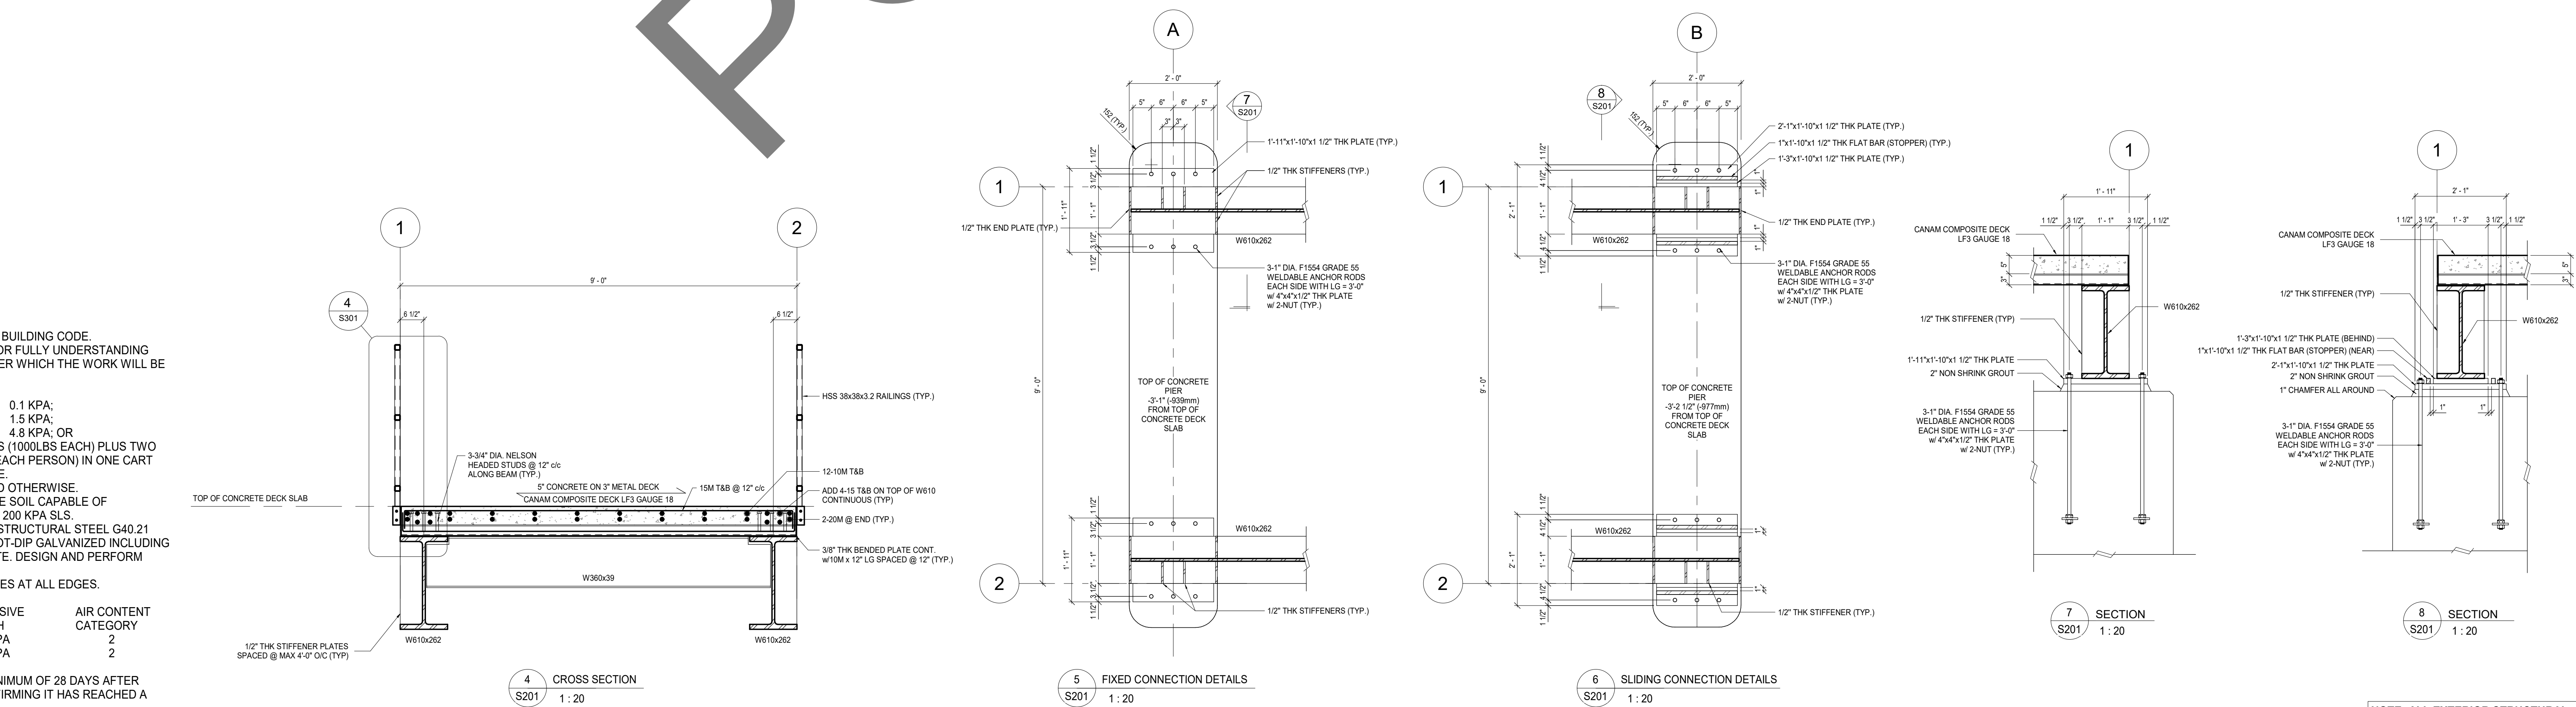
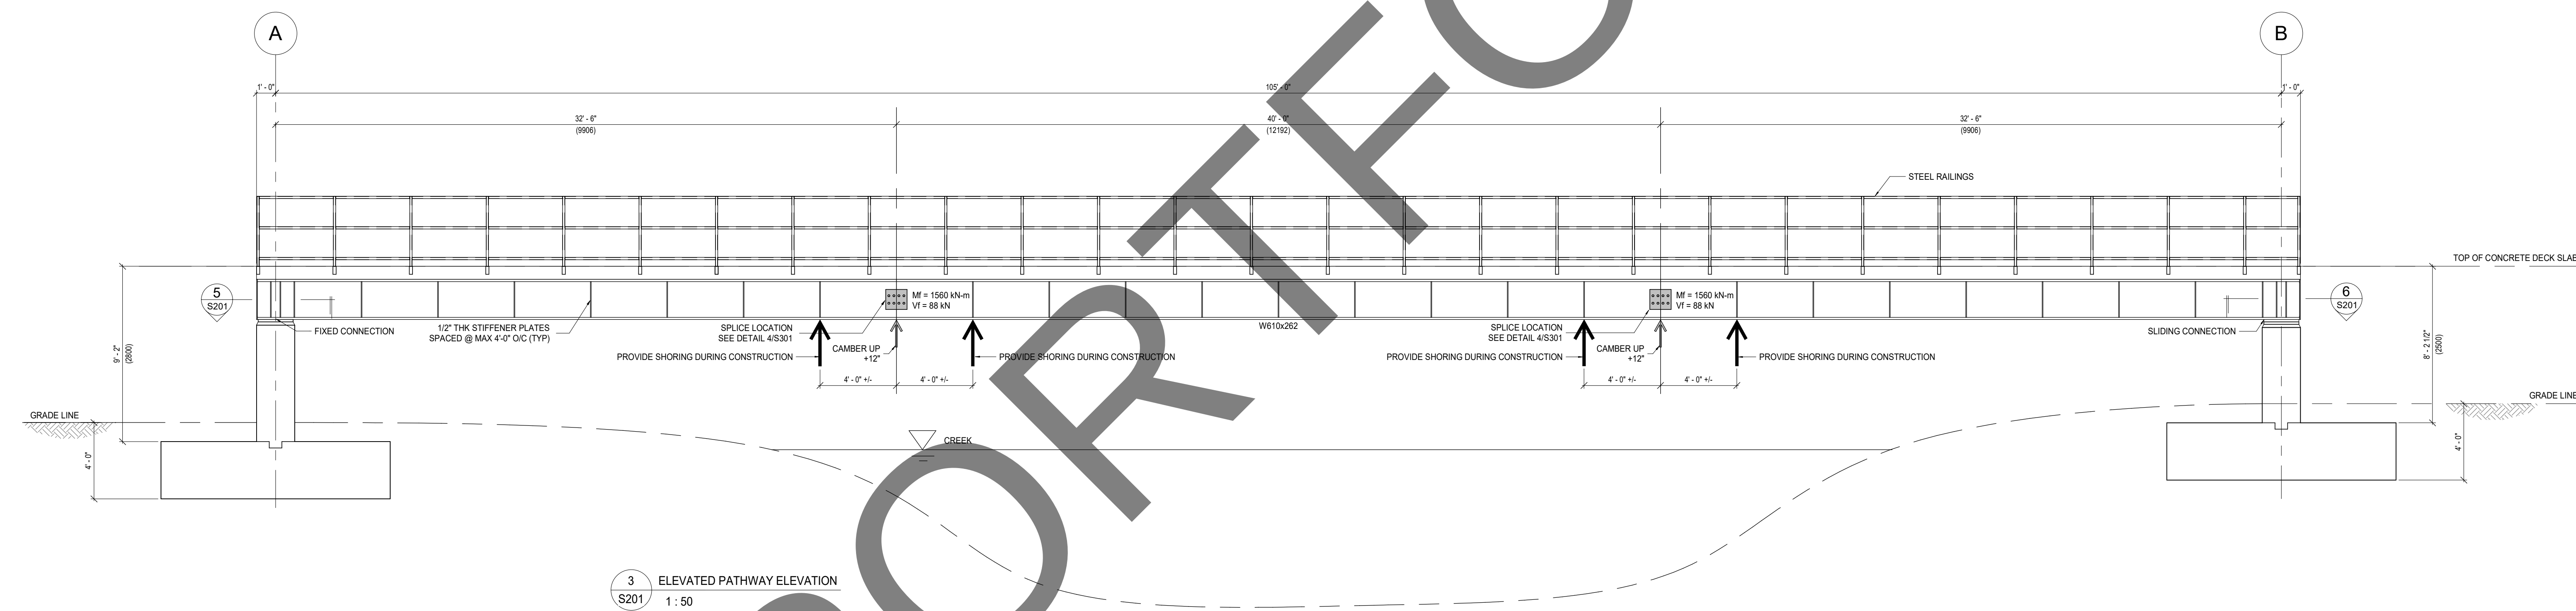
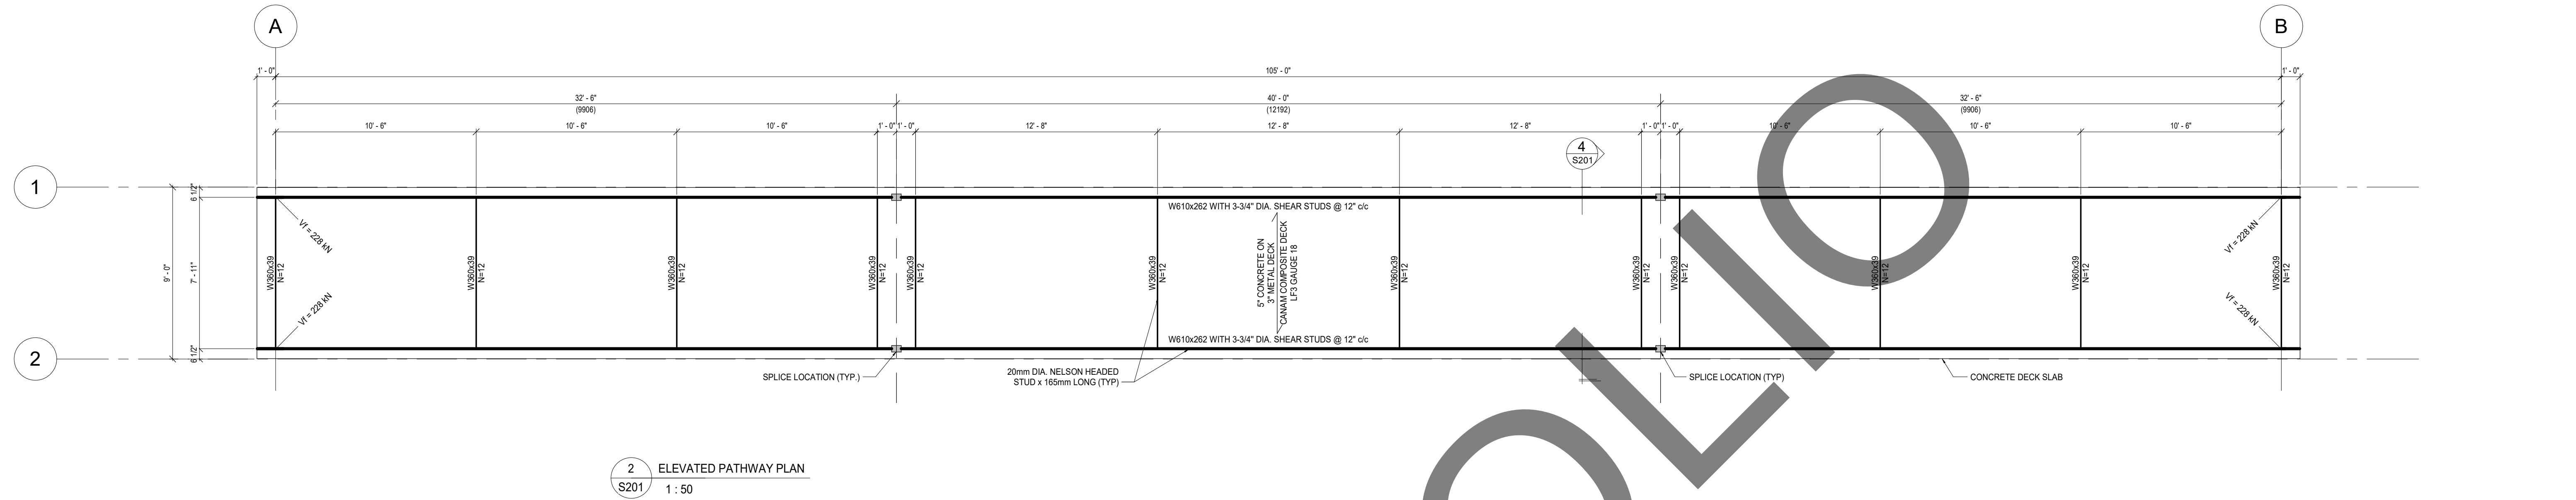


1. STRUCTURAL STEEL SHALL BE NEW CARBON STRUCTURAL STEEL CSA G40.21 GRADE 300W.
2. STRUCTURAL STEEL SHALL BE GALVANIZED INCLUDING ANCHOR ROD, WASHER, AND NUT.
3. USE NELSON HEADED FOR SHEAR STUDS AND F1554 GRADE 55 FOR ANCHOR RODS.
4. DESIGN AND PERFORM WELDING IN ACCORDANCE WITH CSA W59.1.
5. PROVIDE DECK CLOSURE PLATES AT ALL EDGES.

DRAWING NUMBER

6200

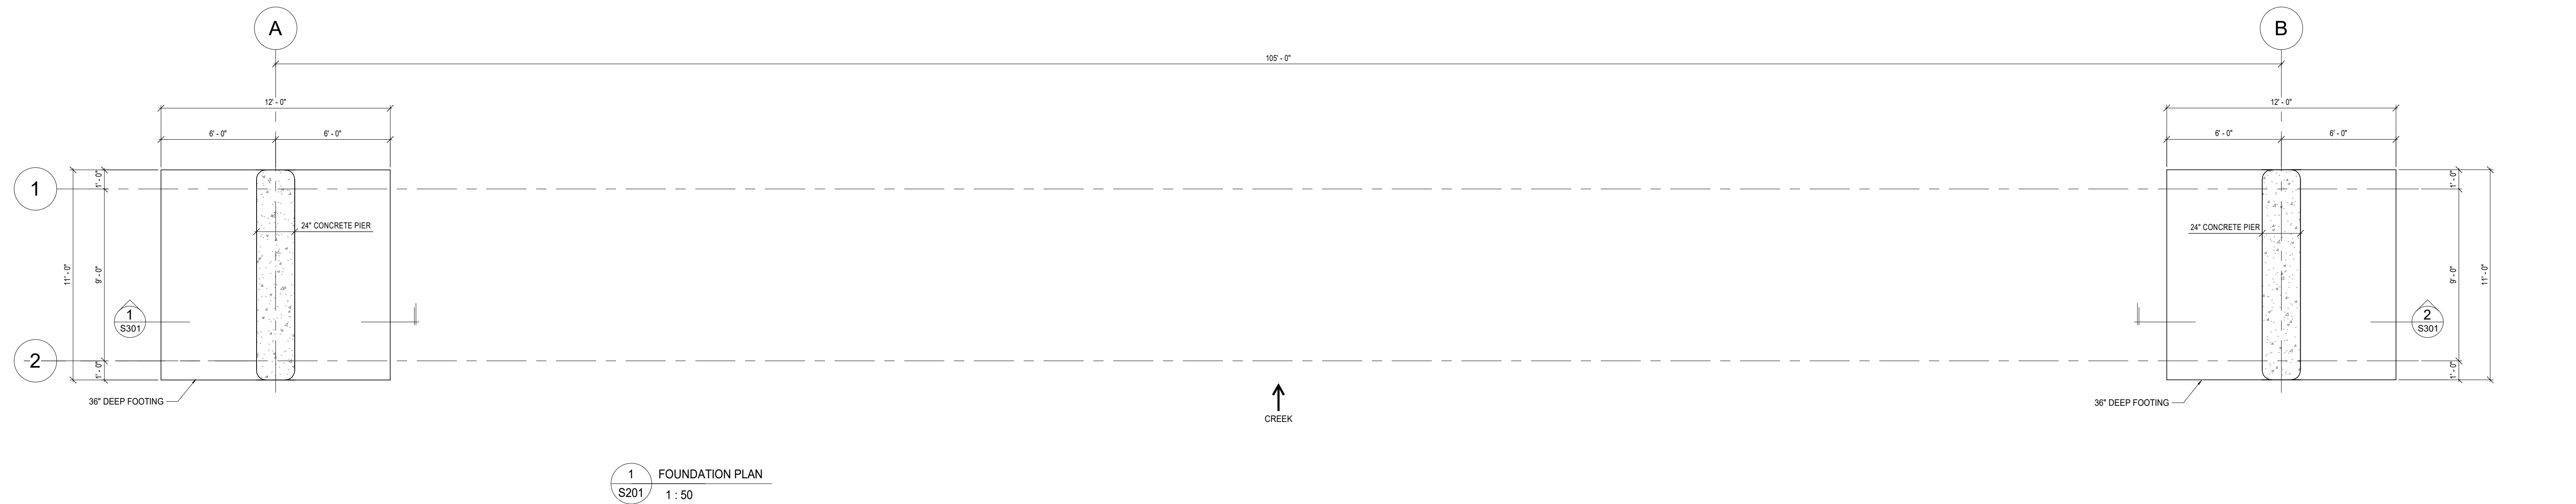

- NOTES:
- THIS PROJECT SHALL COMPLY WITH ONTARIO BUILDING CODE.
 - THE CONTRACTOR SHALL BE RESPONSIBLE FOR FULLY UNDERSTANDING THE NATURE OF WORK AND CONDITIONS UNDER WHICH THE WORK WILL BE PERFORMED.
 - DESIGN LOADS:
 - SUPERIMPOSED DEAD LOAD: 0.1 KPA;
 - SNOW LOAD (SS+1.1, SR+0.4): 1.5 KPA;
 - LIVE LOAD: 4.8 KPA; OR ALLOW MAX EIGHT (8) GOLF CARTS (1000LBS EACH) PLUS TWO PASSENGERS (ASSUMED 250LBS EACH PERSON) IN ONE CART ON THE BRIDGE AT THE SAME TIME.
 - TOP OF STEEL SEE ELEVATION UNLESS NOTED OTHERWISE.
 - FOUND ALL FOOTING ON UNDISTURBED NATIVE SOIL CAPABLE OF PROVIDING A MINIMUM BEARING CAPACITY OF 200 KPA SLS.
 - STRUCTURAL STEEL SHALL BE NEW CARBON STRUCTURAL STEEL G40.21 GRADE 350. STRUCTURAL STEEL SHALL BE HOT-DIP GALVANIZED INCLUDING ANCHOR ROD, WASHER, NUTS AND BASE PLATE. DESIGN AND PERFORM WELDING IN ACCORDANCE WITH CSA W59.24.
 - PROVIDE 1/2\" (6mm) BENT DECK CLOSURE PLATES AT ALL EDGES.
 - CONCRETE:

EXPOSURE CLASS	COMPRESSIVE STRENGTH	AIR CONTENT CATEGORY
F-2	F _c = 35 MPA	2
C-1	F _c = 35 MPA	2
 - DO NOT REMOVE SHORING POSTS UNTIL A MINIMUM OF 28 DAYS AFTER POURING CONCRETE ON THE DECK AND CONFIRMING IT HAS REACHED A COMPRESSIVE STRENGTH OF F_c = 35 MPA.
 - REFER TO DRAWING S302 FOR PATHWAY GIRDER W610x262 BEAM CUTTING AND SPLICING DETAILS.

NOTE: ALL EXTERIOR STRUCTURAL STEEL INCLUDING ANCHOR ROD, WASHER AND NUT SHALL BE GALVANIZED.

RESERVED FOR AUTHORITY STAMP

ISSUED FOR RECORD
DATE

Client:



245 Markland Drive, Toronto, Ontario M3C 1R1
marklandwood.com | (416) 621-2255

Structural Consultants:



897 Yonge Street, Suite 300, Toronto, Ontario, Canada M4W 3P4
1-416-961-5256 | 1-416-961-7434
q.dressel@quinn-dressel.com | www.quinn-dressel.com

CONTRACTOR SHALL CHECK ALL DIMENSIONS ON THE WORK AND REPORT ANY DISCREPANCY TO THE CONSULTANT BEFORE PROCEEDING. THIS DRAWING IS NOT TO BE USED FOR CONSTRUCTION UNTIL AUTHORIZED IN WRITING BY CONSULTANT.

NO.	DATE	REVISION
1	2024-02-24	ISSUED FOR CLIENT'S REVIEW
2	2024-02-28	ISSUED FOR UPDATES
3	2024-02-11	ISSUED FOR RECORD

NOT FOR CONSTRUCTION

MARKLAND WOOD GOLF CLUB-ELEVATED PATHWAY






PROJECT ADDRESS:
245 MARKLAND DRIVE, TORONTO, ONTARIO M3C 1R1
PROJECT CLIENT:
MARKLAND WOOD GOLF CLUB

SCALE: As Indicated
DRAWN BY: JC
REVIEWED BY: RT
PROJECT NUMBER: 24-172
PLOT DATE: 2024-02-11 13:27:55 PM

PROPOSED ELEVATED PATHWAY



DRAWING NUMBER

S201

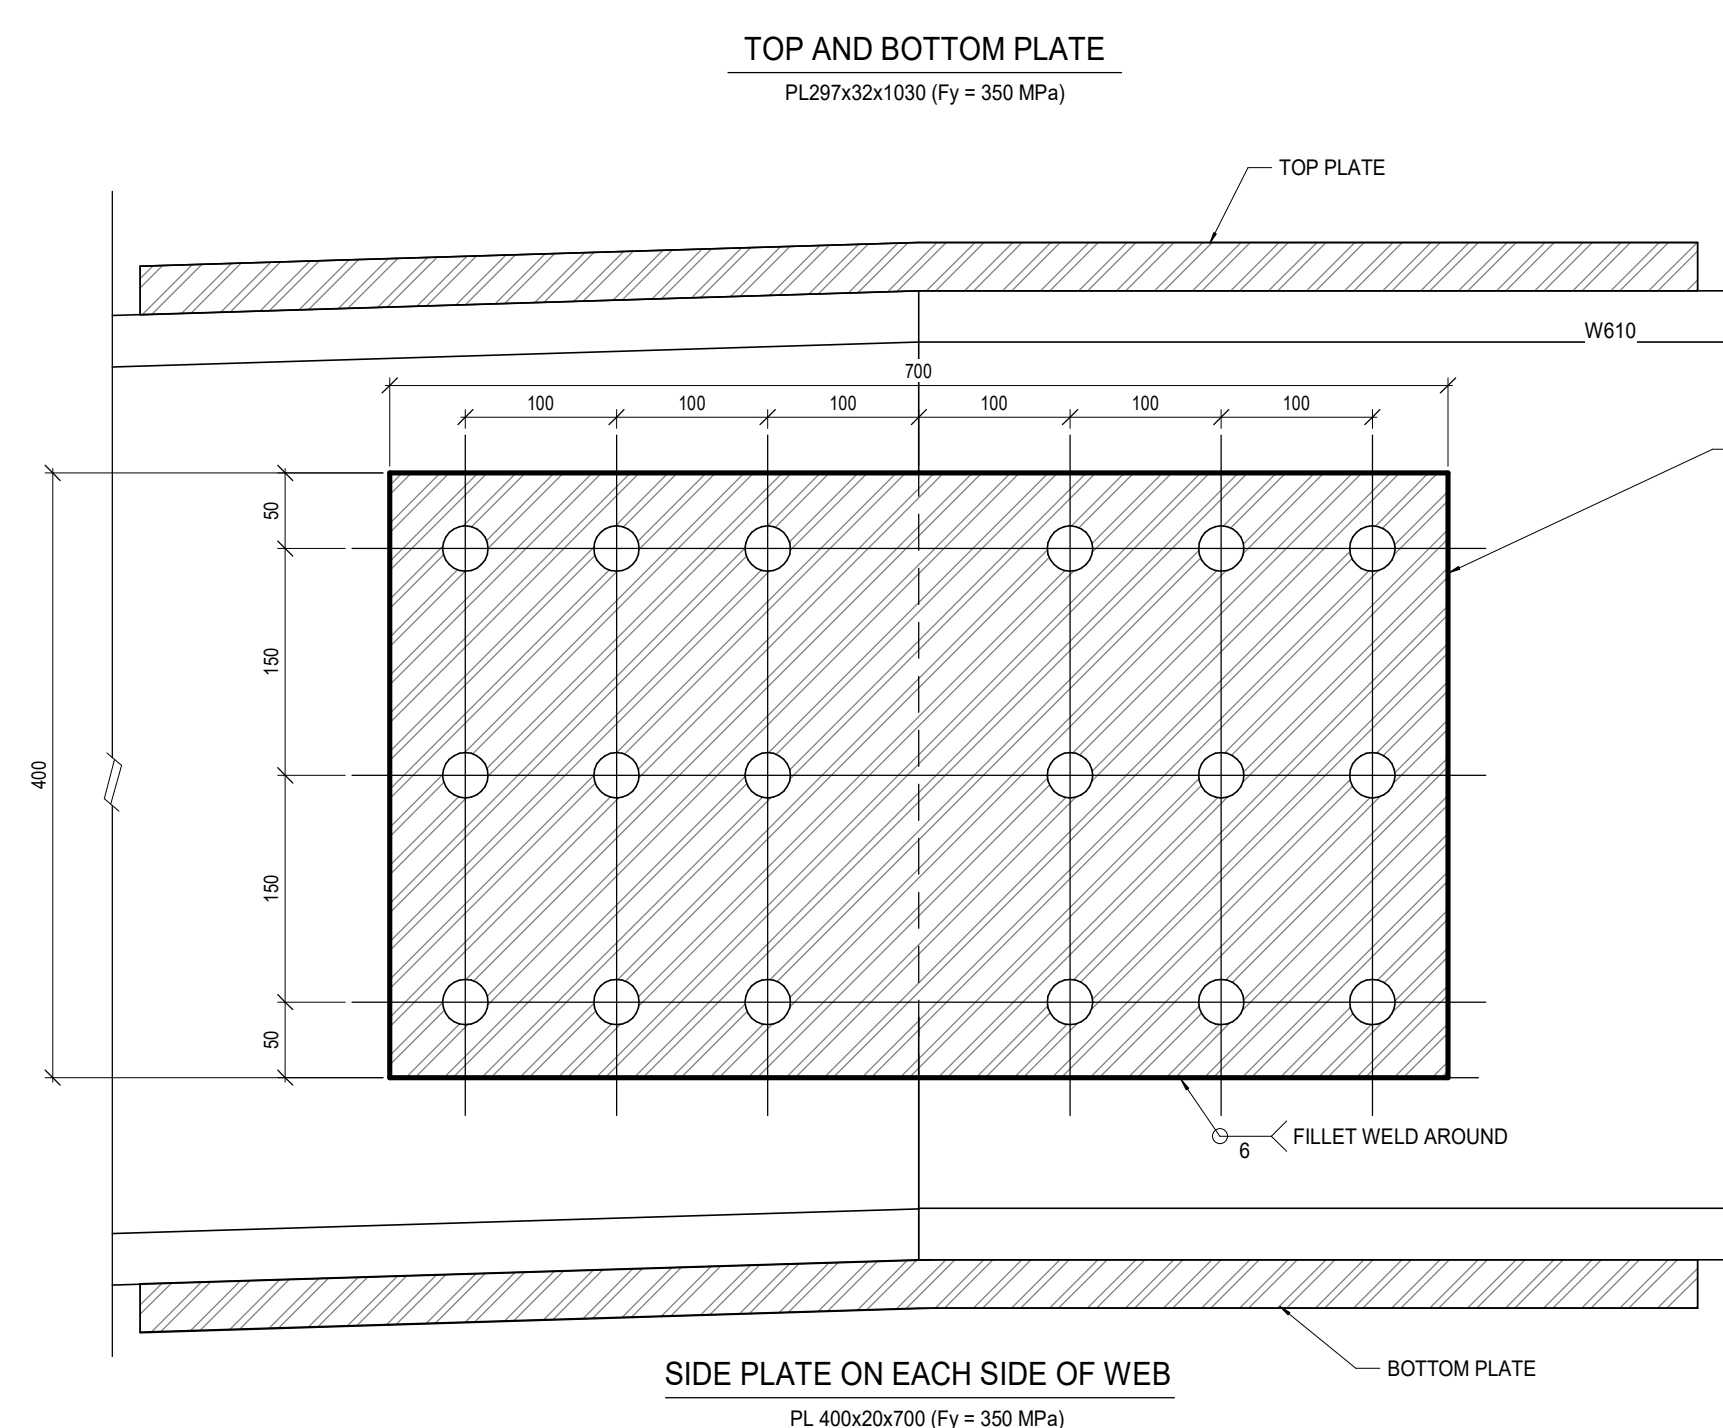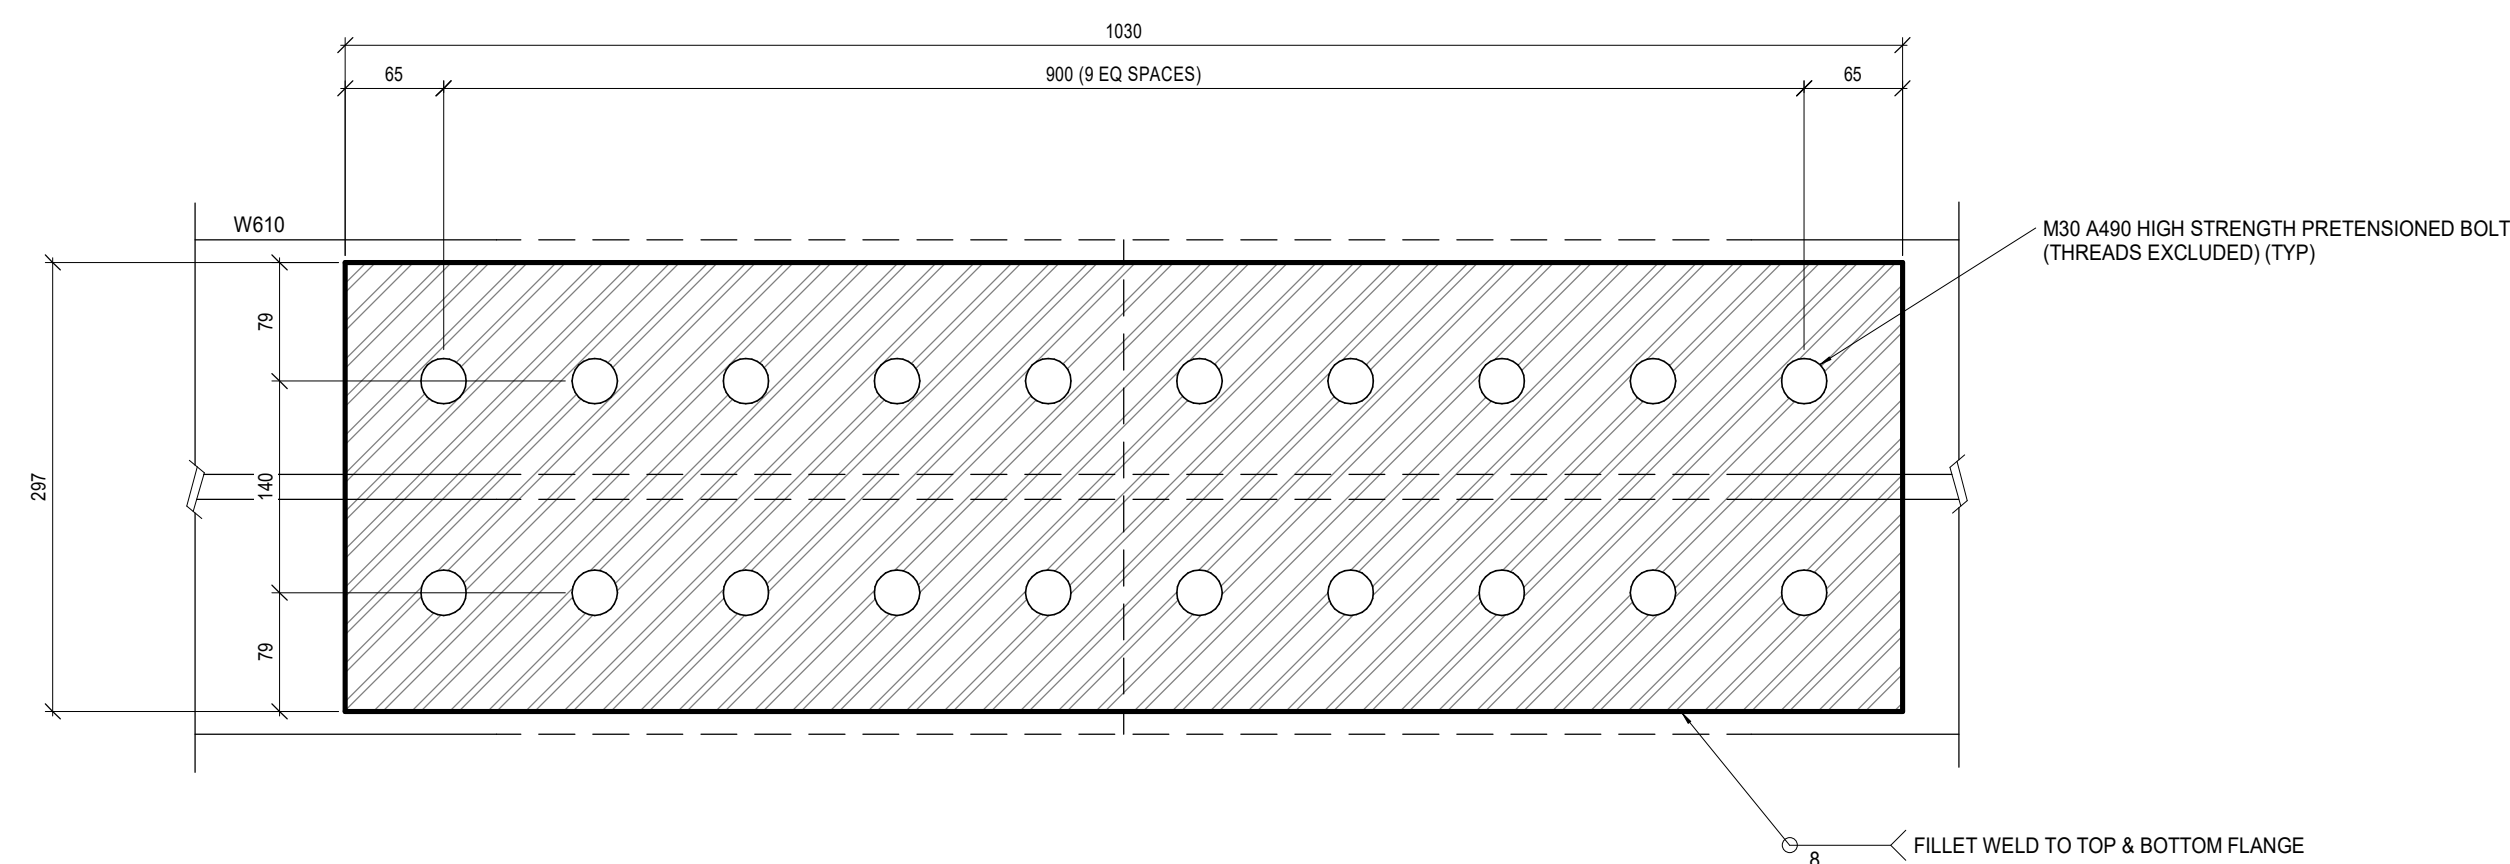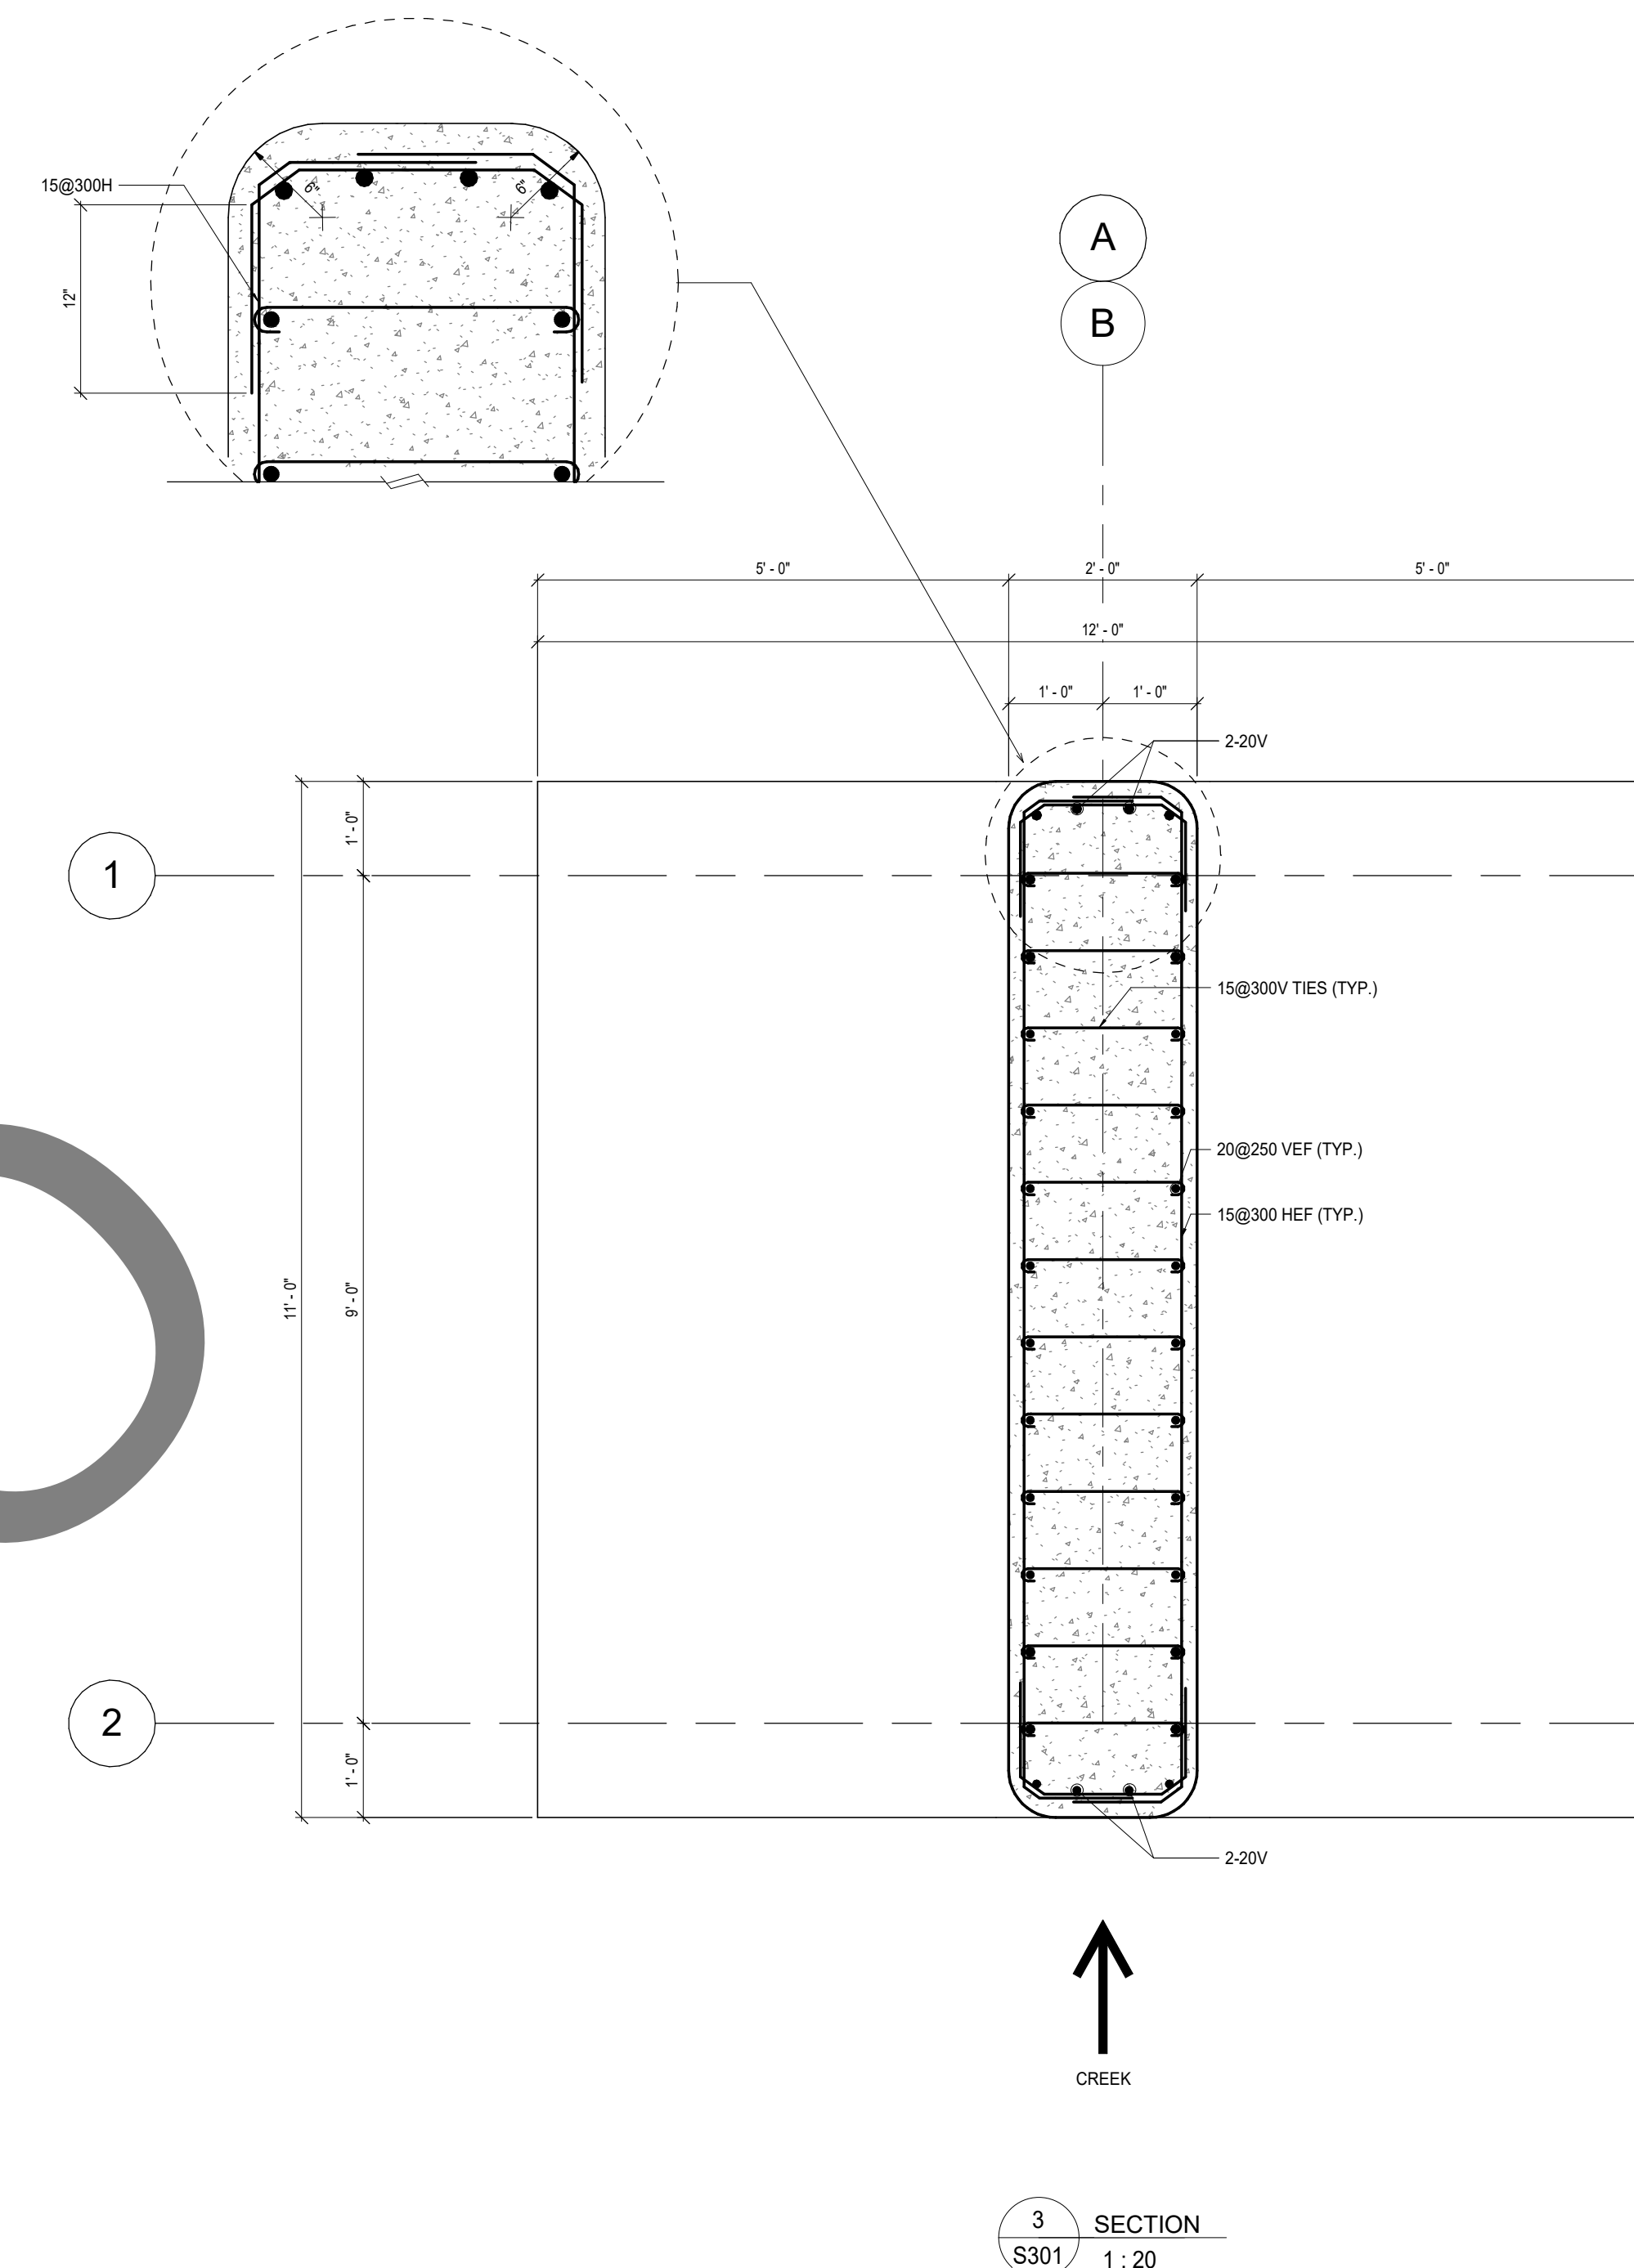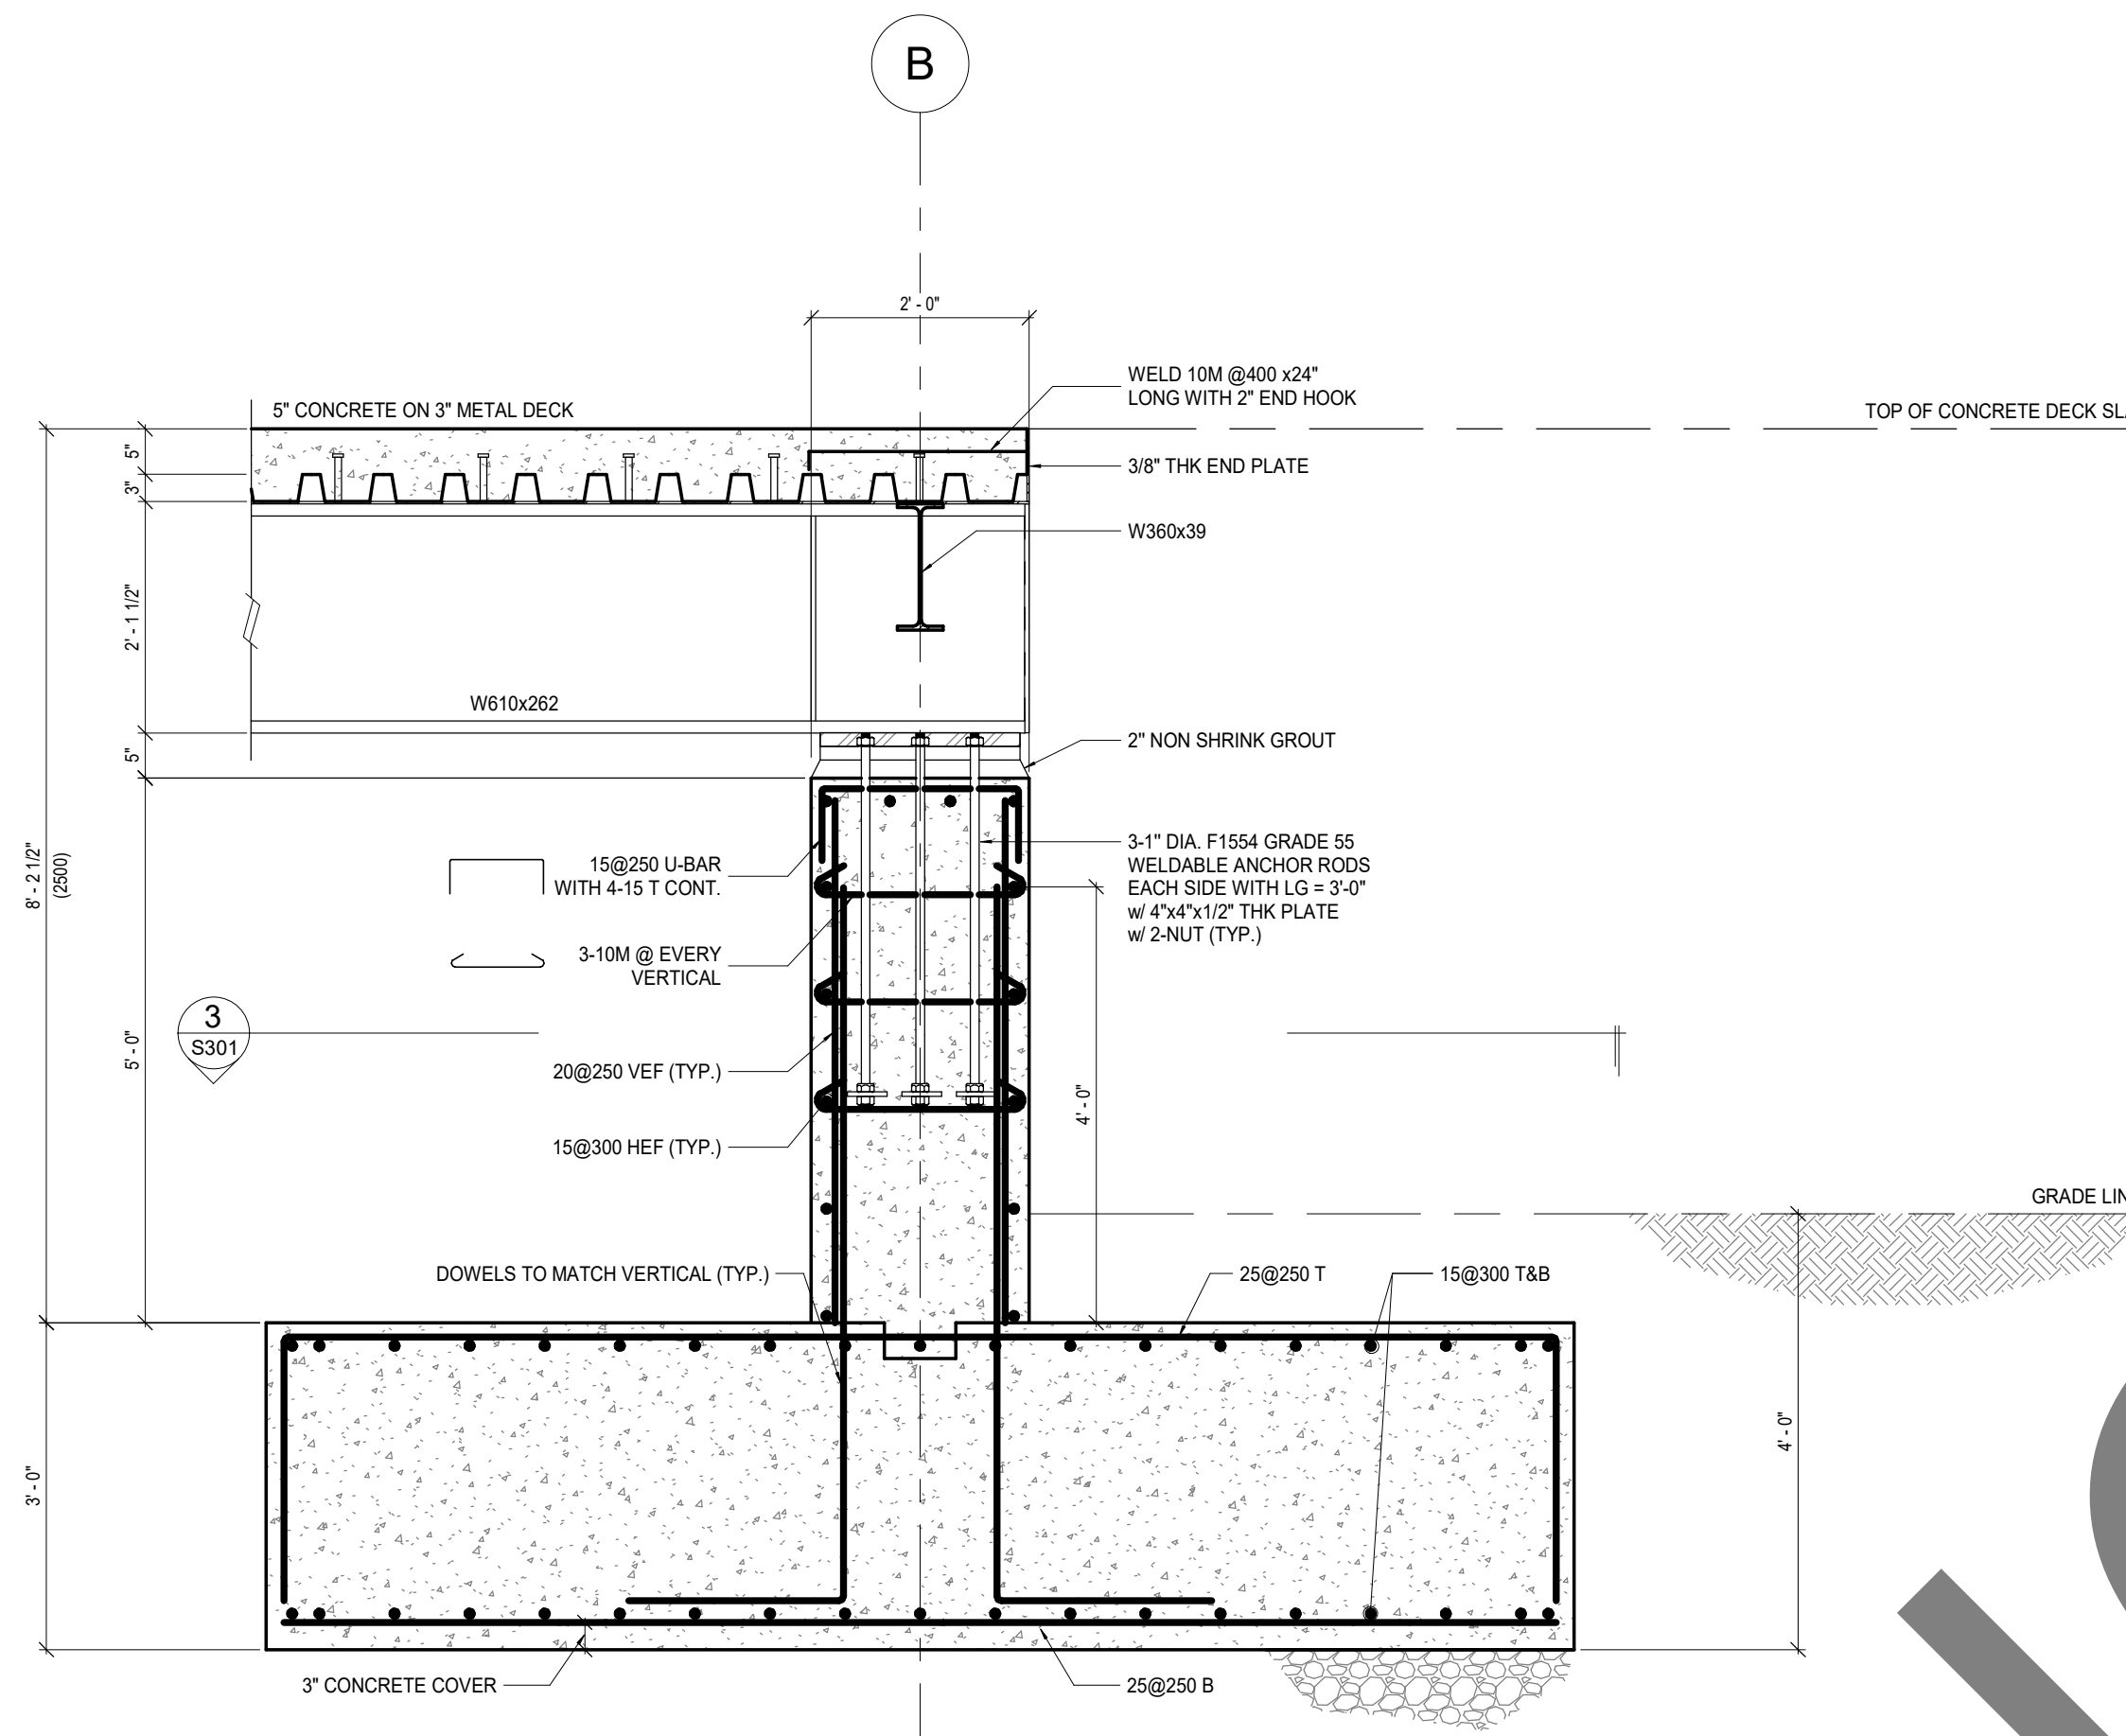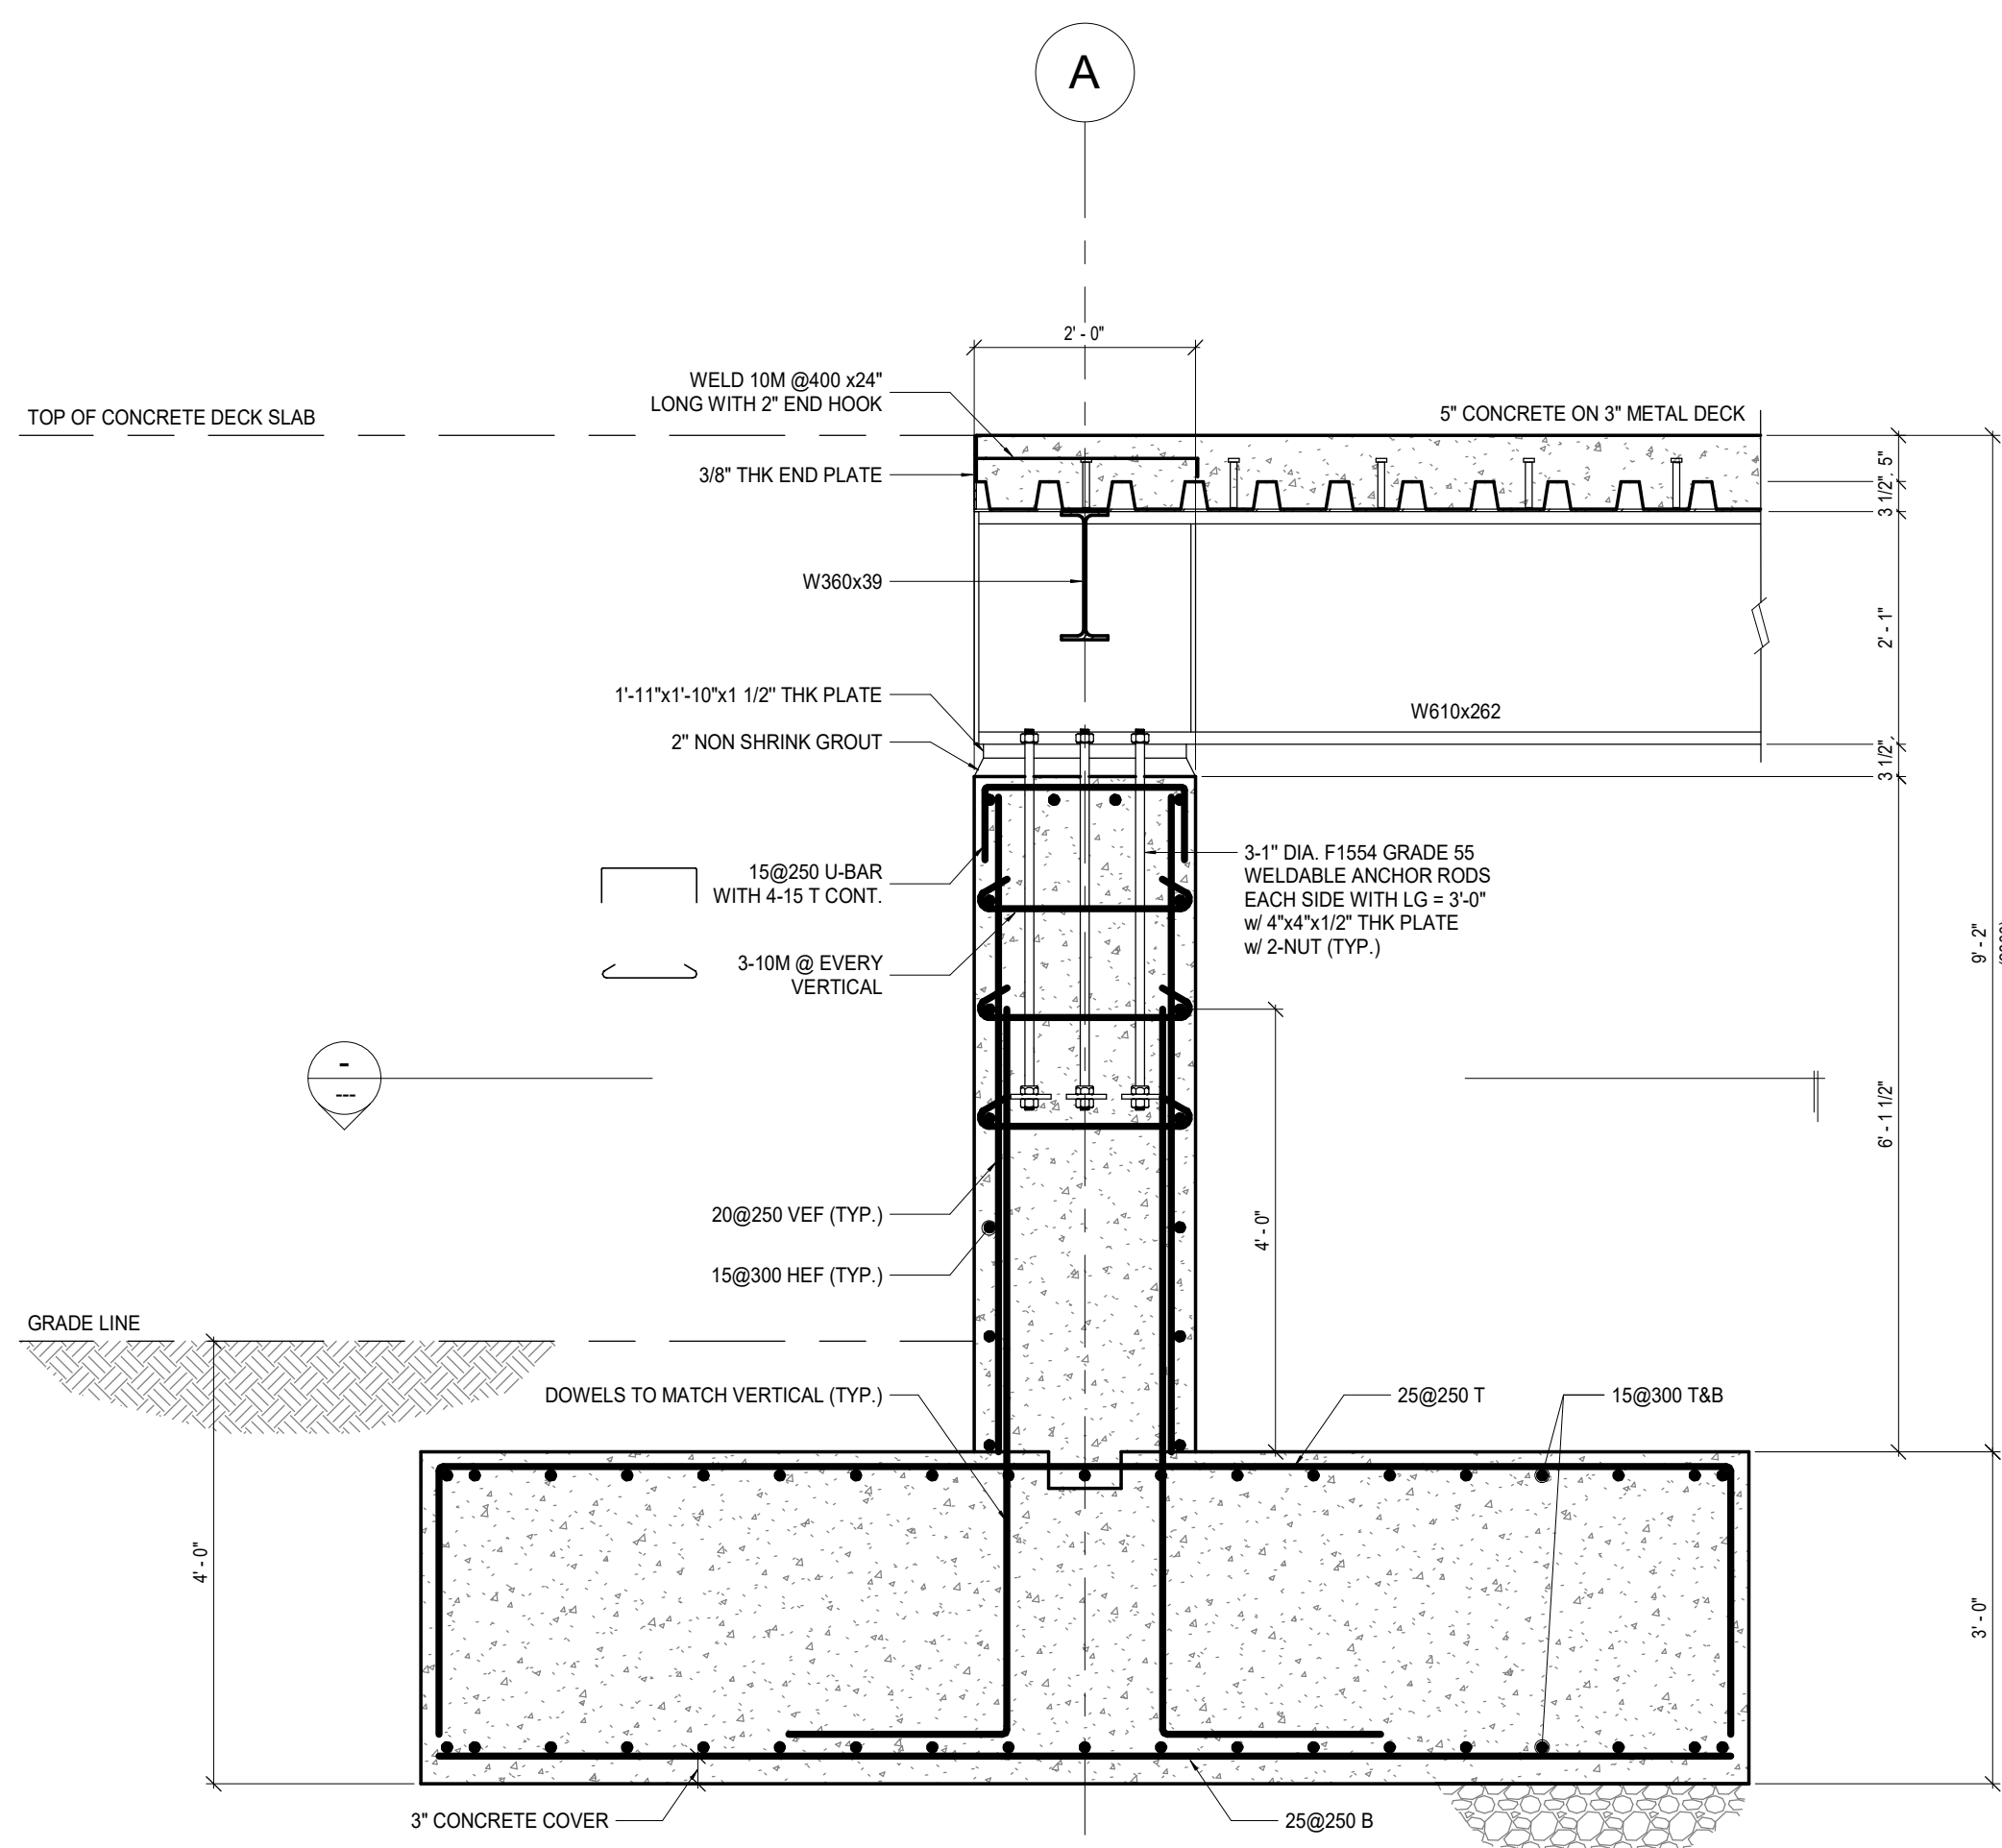

6 SPLICE CONNECTION PLATE DETAILS
S301 1:5

NOTES:
1. A990 BOLTS SHALL BE PROVIDED WITH WEATHERING STEEL FINISH OR COATING.
2. ALL STRUCTURAL STEEL SHALL BE GALVANIZED.

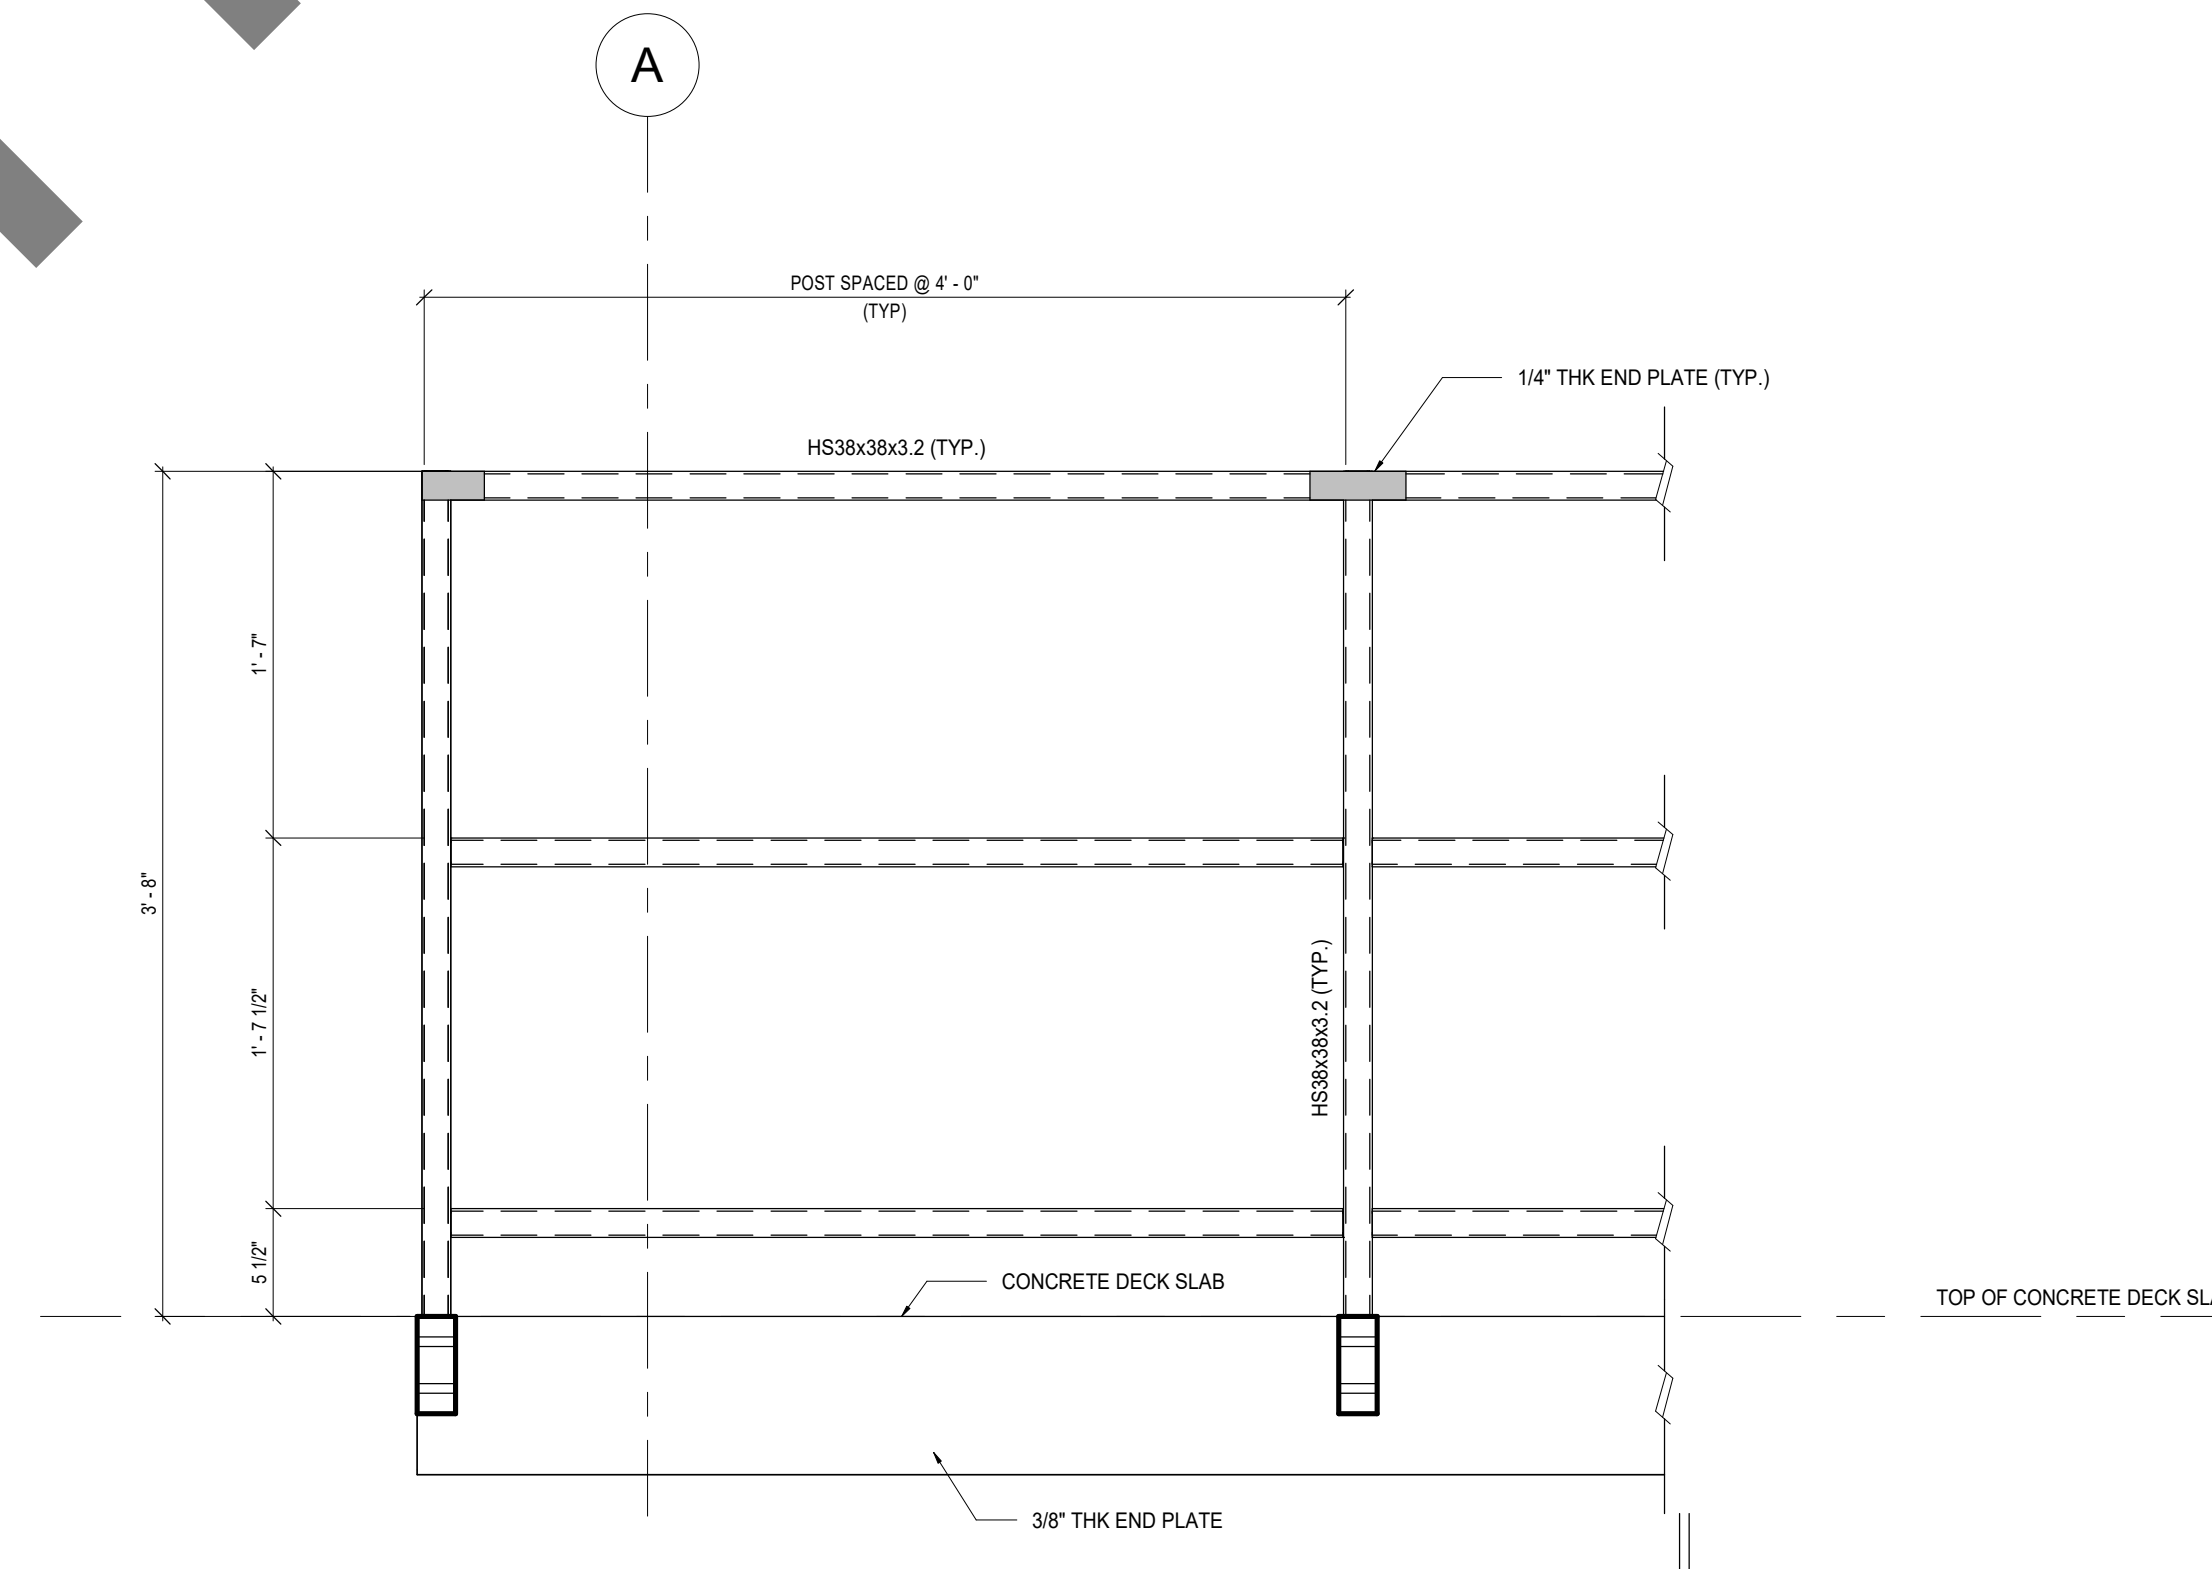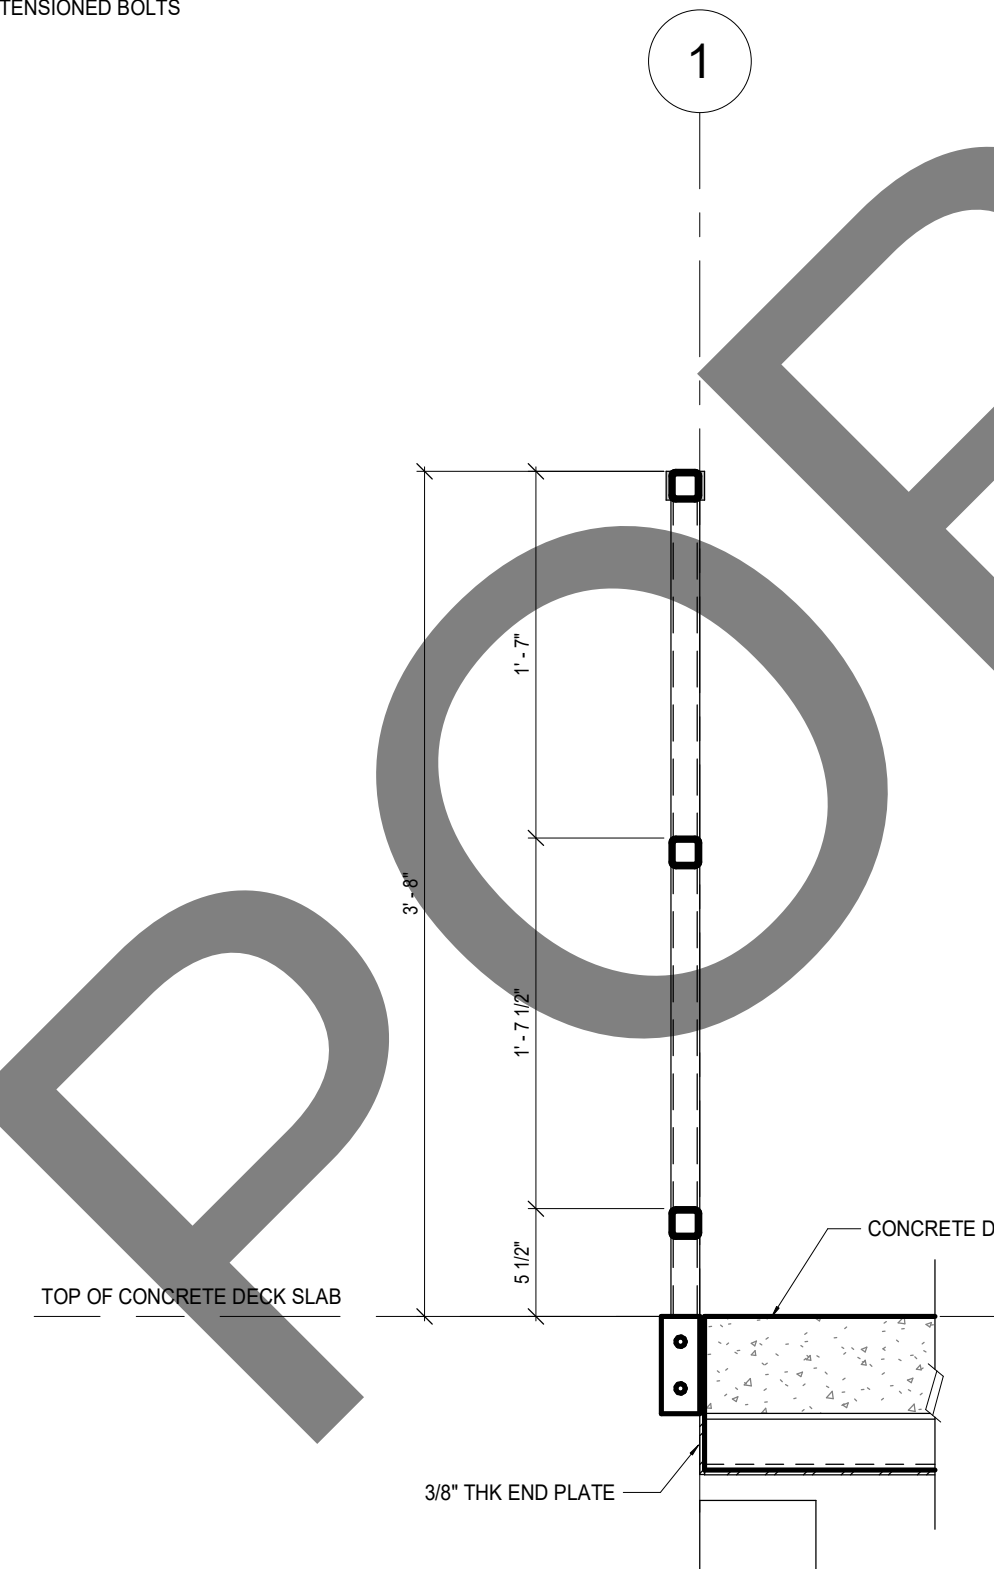

5 STEEL RAILING DETAILS
S301 1:10

NOTES:
1. ALL EXTERIOR STRUCTURAL STEEL INCLUDING ANCHOR ROD, WASHER AND NUT SHALL BE GALVANIZED.
2. THE FOOTING SHALL BE FOUND ON UNDISTURBED SOIL WITH ALLOWABLE BEARING PRESSURE = 75 KPa; SEE THE GEOTECHNICAL INVESTIGATION REPORT PREPARED BY GEOTERRE LIMITED ON APRIL 05, 2016 WITH FILE # TG15-007.

RESERVED FOR AUTHORITY STAMP

ISSUED FOR RECORD
DATE

Client:



245 Markland Drive, Toronto, Ontario M6C 1R1
marklandwood.com | (416) 621-2255

Structural Consultants:



897 Yonge Street, Suite 300, Toronto, Ontario, Canada M4W 3P4
1-416-961-8256 | 1-416-961-7434
q.dressel@quinn-dressel.com | www.quinn-dressel.com

CONTRACTOR SHALL CHECK ALL DIMENSIONS ON THE WORK AND REPORT ANY DISCREPANCIES TO THE CONSULTANT BEFORE PROCEEDING. THIS DRAWING IS NOT TO BE USED FOR CONSTRUCTION UNTIL AUTHORIZED IN WRITING BY CONSULTANT.

NO.	DATE	REVISION
3	2024-02-11	ISSUED FOR RECORD
2	2023-04-26	ISSUED FOR UPDATE
1	2024-02-24	ISSUED FOR CLIENTS REVIEW

NOT FOR
CONSTRUCTION

MARKLAND WOOD GOLF CLUB-ELEVATED PATHWAY

PROJECT ADDRESS:
245 MARKLAND DRIVE, TORONTO, ONTARIO M6C 1R1
PROJECT CLIENT:
MARKLAND WOOD GOLF CLUB

SCALE: As indicated
DRAWN BY: JC
REVIEWED BY: RT
PROJECT NUMBER: 24-172
PLOT DATE: 2024-02-11 3:27:57 PM


PROPOSED ELEVATED PATHWAY

DRAWING NUMBER

S301




1 PATHWAY GIRDER ELEVATION AND PIECE DRAWING
S302 1:50

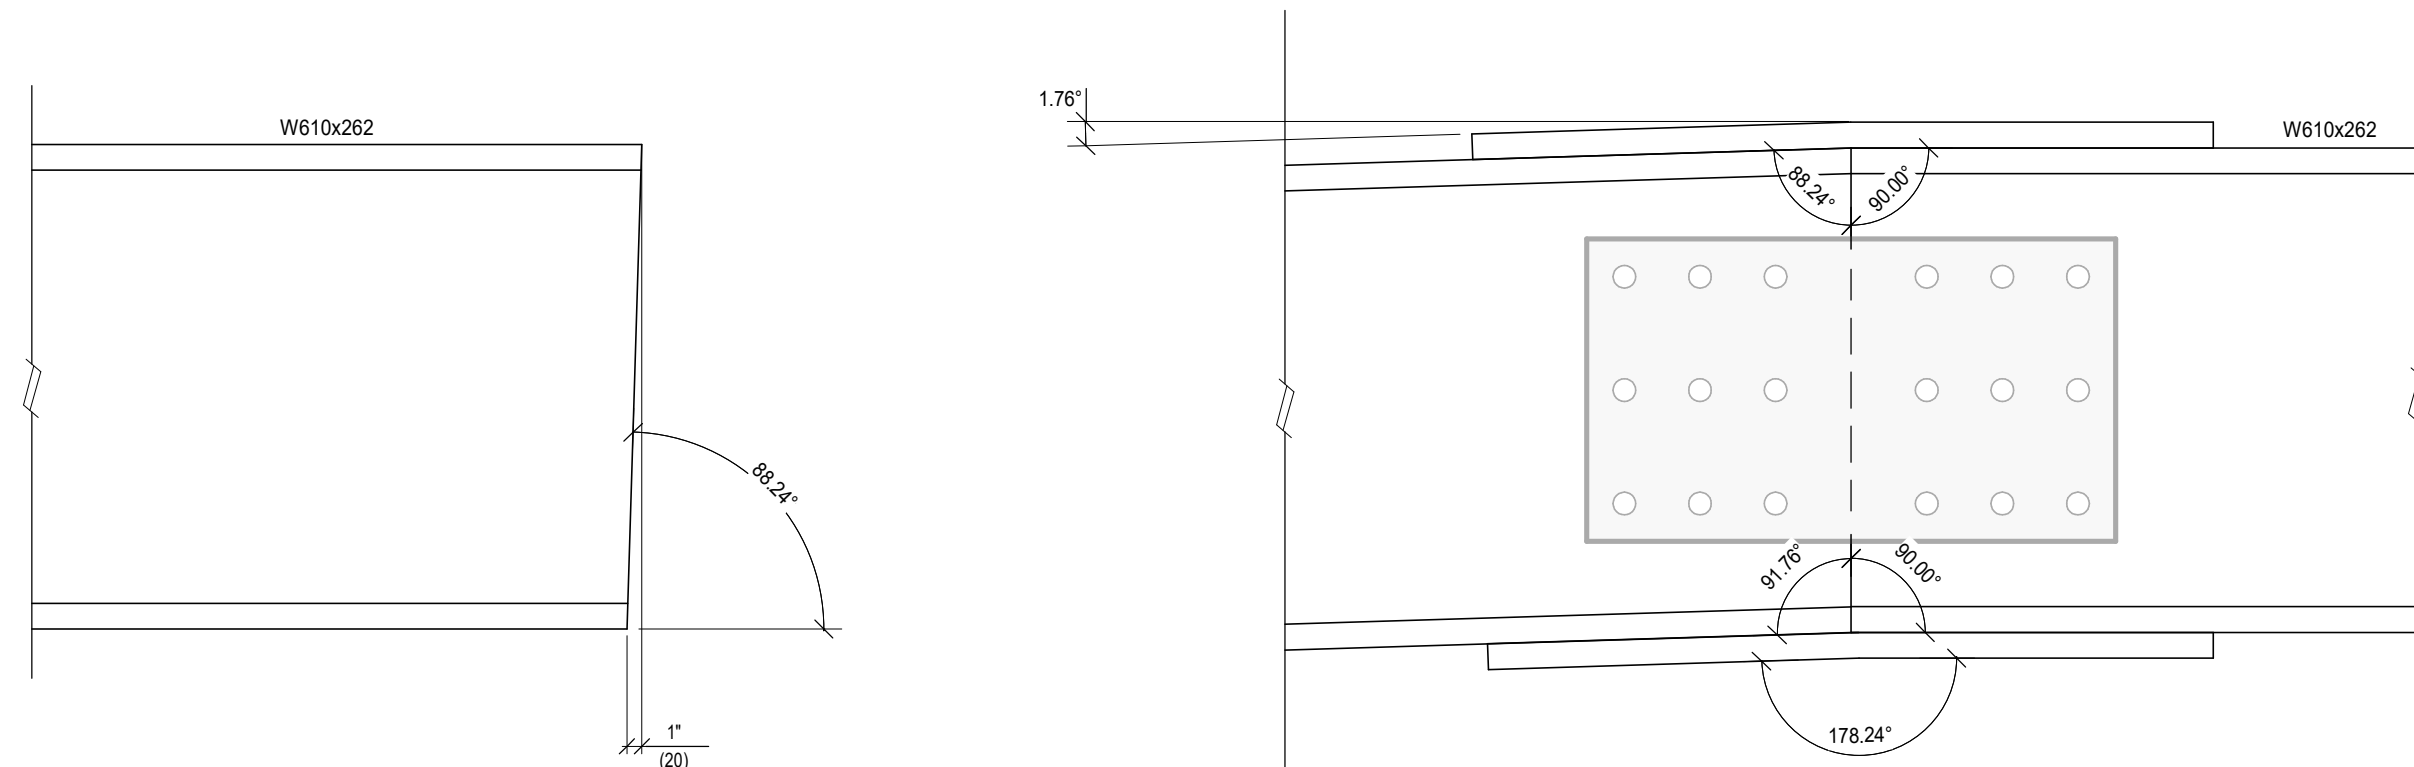

2 CUT DETAIL
S302 1:10

3 SPLICE GEOMETRY
S302 1:10

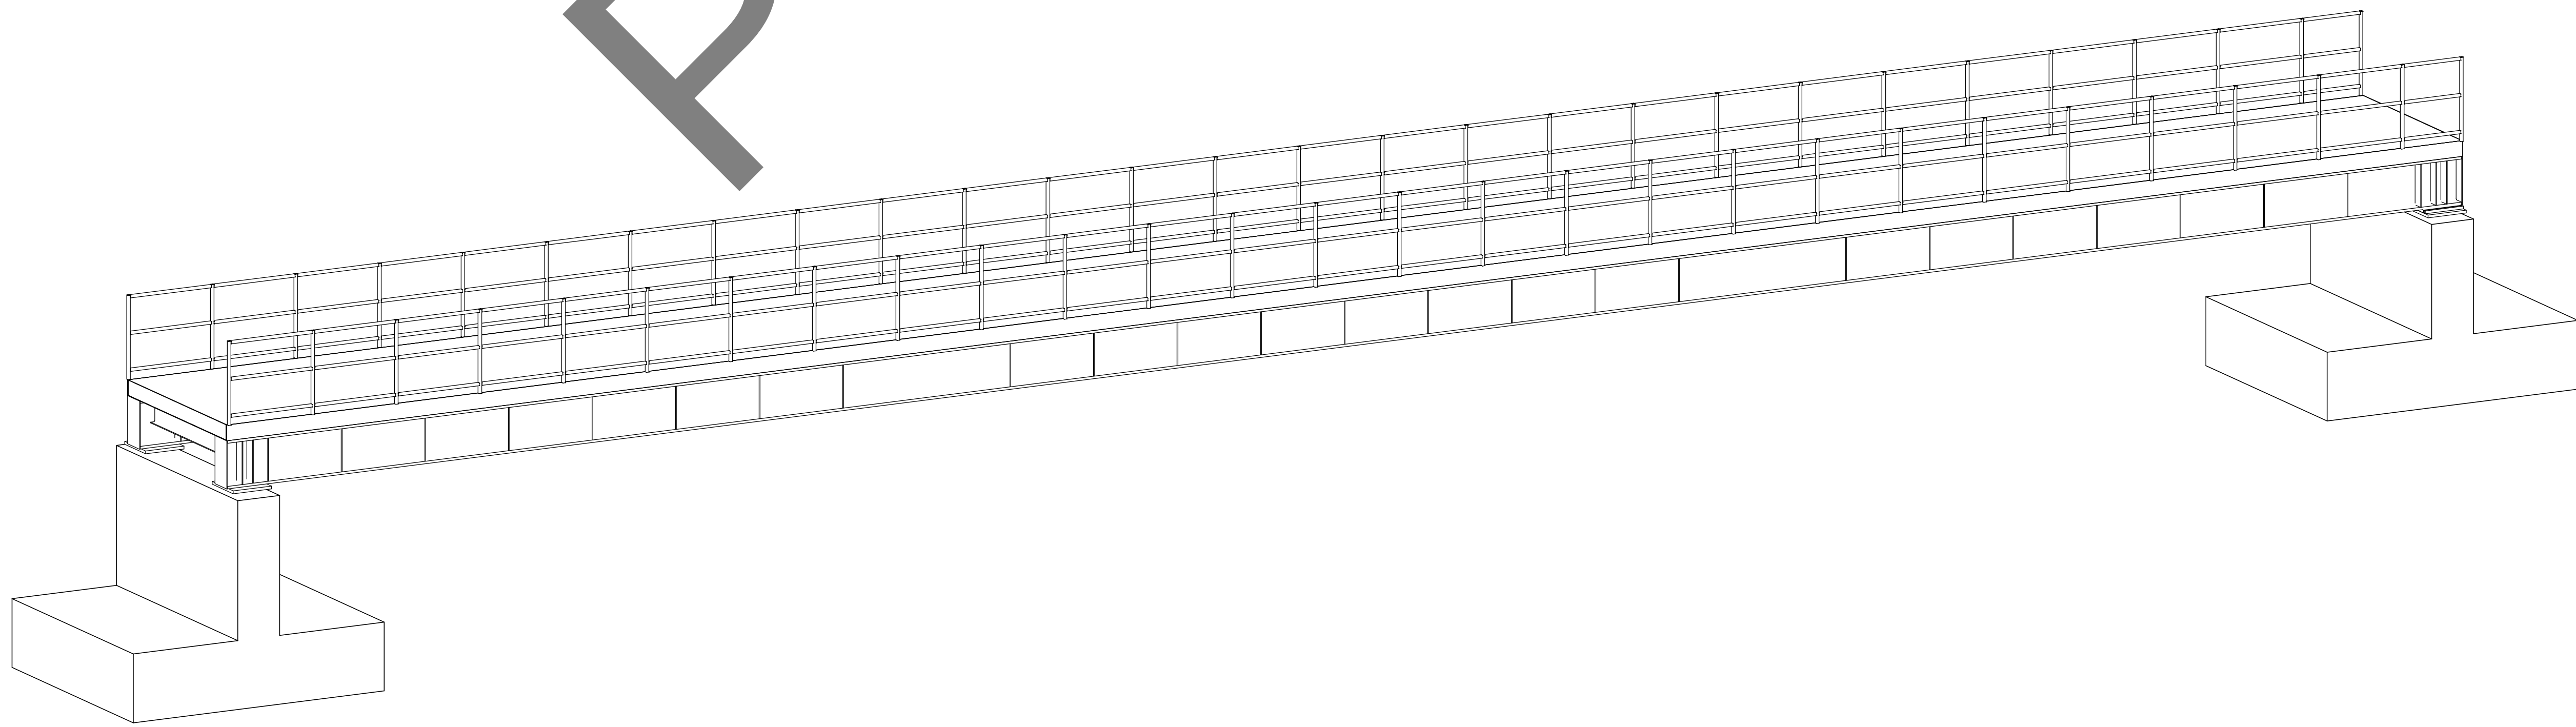

4 Axonometric View
S302

RESERVED FOR AUTHORITY STAMP

ISSUED FOR RECORD 2026-02-11
DATE

Client:



245 Markland Drive, Toronto, Ontario M6C 1R1
marklandwood.com | (416) 621-2255

Structural Consultants:



891 Yonge Street, Suite 300, Toronto, Ontario Canada M4W 3P4
T: 416.961.8256 | F: 416.961.7434
e: qdres@quinn-dressel.com | www.quinn-dressel.com

CONTRACTOR SHALL CHECK ALL DIMENSIONS ON THE WORK AND REPORT ANY DISCREPANCY TO THE CONSULTANT BEFORE PROCEEDING. THIS DRAWING IS NOT TO BE USED FOR CONSTRUCTION UNTIL AUTHORIZED IN WRITING BY CONSULTANT.

#	DATE	REVISION
3	2026-02-11	ISSUED FOR RECORD
2	2025-04-28	ISSUED FOR UPDATE
1	2025-02-24	ISSUED FOR CLIENT'S REVIEW

NOT FOR
CONSTRUCTION

MARKLAND WOOD GOLF CLUB-ELEVATED PATHWAY
PROJECT ADDRESS:
245 MARKLAND DRIVE, TORONTO, ONTARIO M6C 1R1
PROJECT CLIENT:
MARKLAND WOOD GOLF CLUB

SCALE: As Indicated
DRAWN BY: JC
REVIEWED BY: RT
PROJECT NUMBER: 24-172
PLOT DATE: 2026-02-11 3:27:29 PM

PROPOSED ELEVATED PATHWAY

DRAWING NUMBER

S302