

KEY PLAN

REVISIONS / ISSUED TO

NO.	DATE	BY
-----	------	----

ARCHITECT / CONSULTANTS

CONTRACTOR SHALL CHECK ALL DIMENSIONS ON THE WORK AND REPORT ANY DISCREPANCY TO THE CONSULTANT BEFORE PROCEEDING. THIS DRAWING IS NOT TO BE USED FOR CONSTRUCTION UNTIL AUTHORIZED IN WRITING BY CONSULTANT.

SEAL / SIGNATURE

ISSUED FOR CONSTRUCTION DATE

CLIENT NAME

HILTON NIAGARA

6381 FALLSVIEW BLVD., NIAGARA FALLS, ON.

DRAWING TITLE

HILTON NIAGARA
SPYCE REDESIGN

CEILING PLAN
AND SECTIONS

DESIGNED BY / DRAWN BY

RY/JC

SCALE





As indicated

DRAWING NUMBER

S201

PROJECT NUMBER

24-123

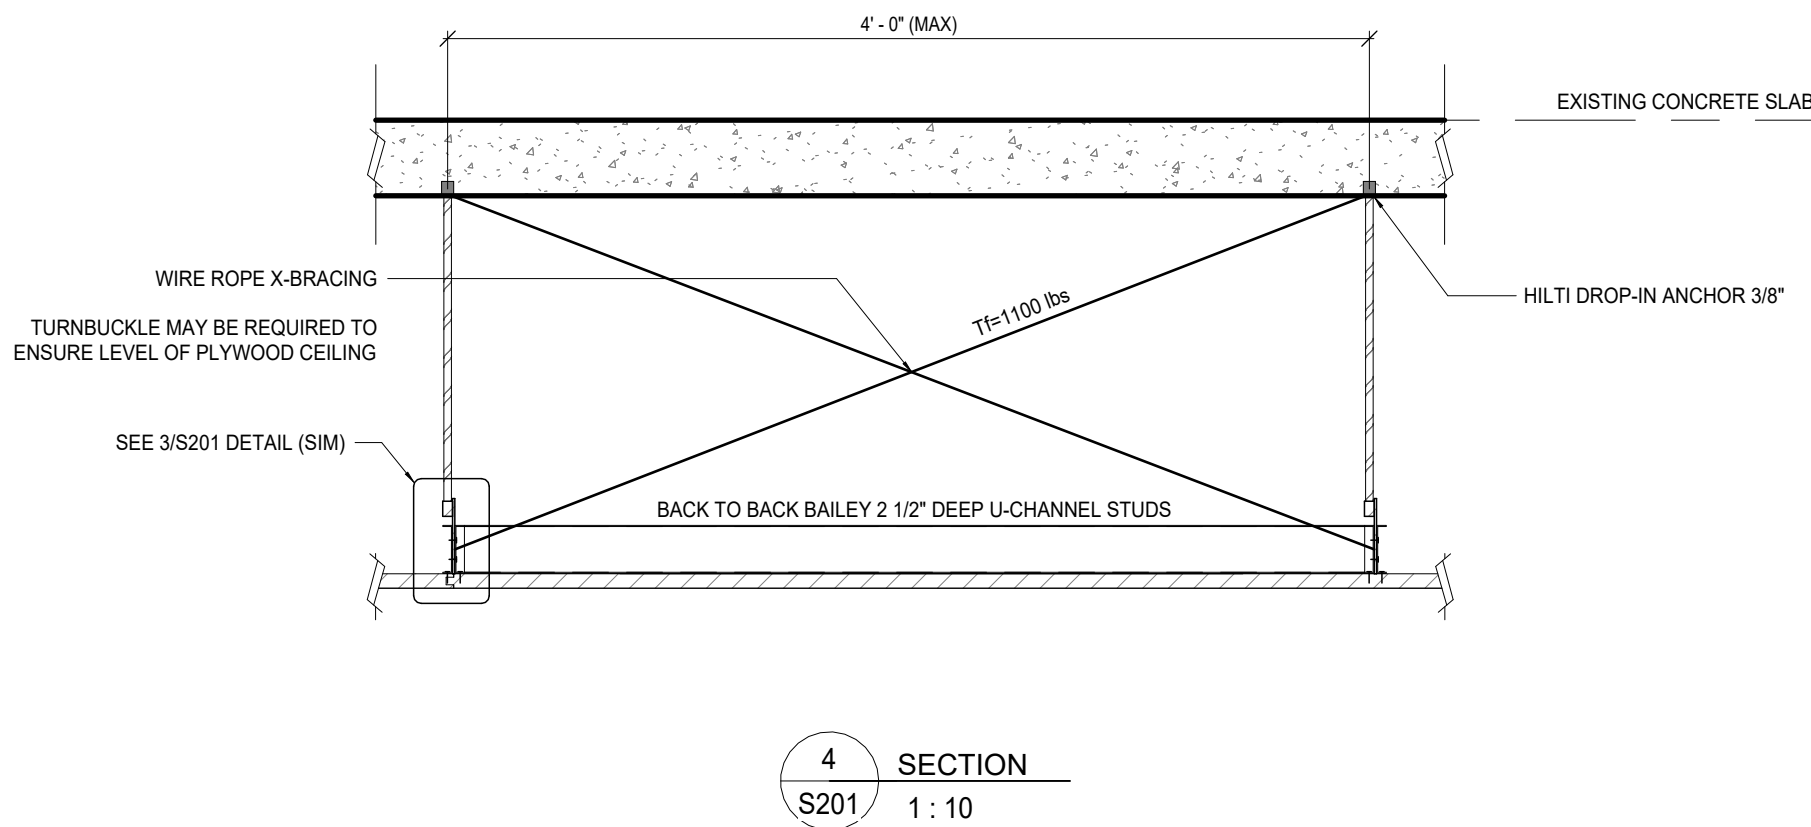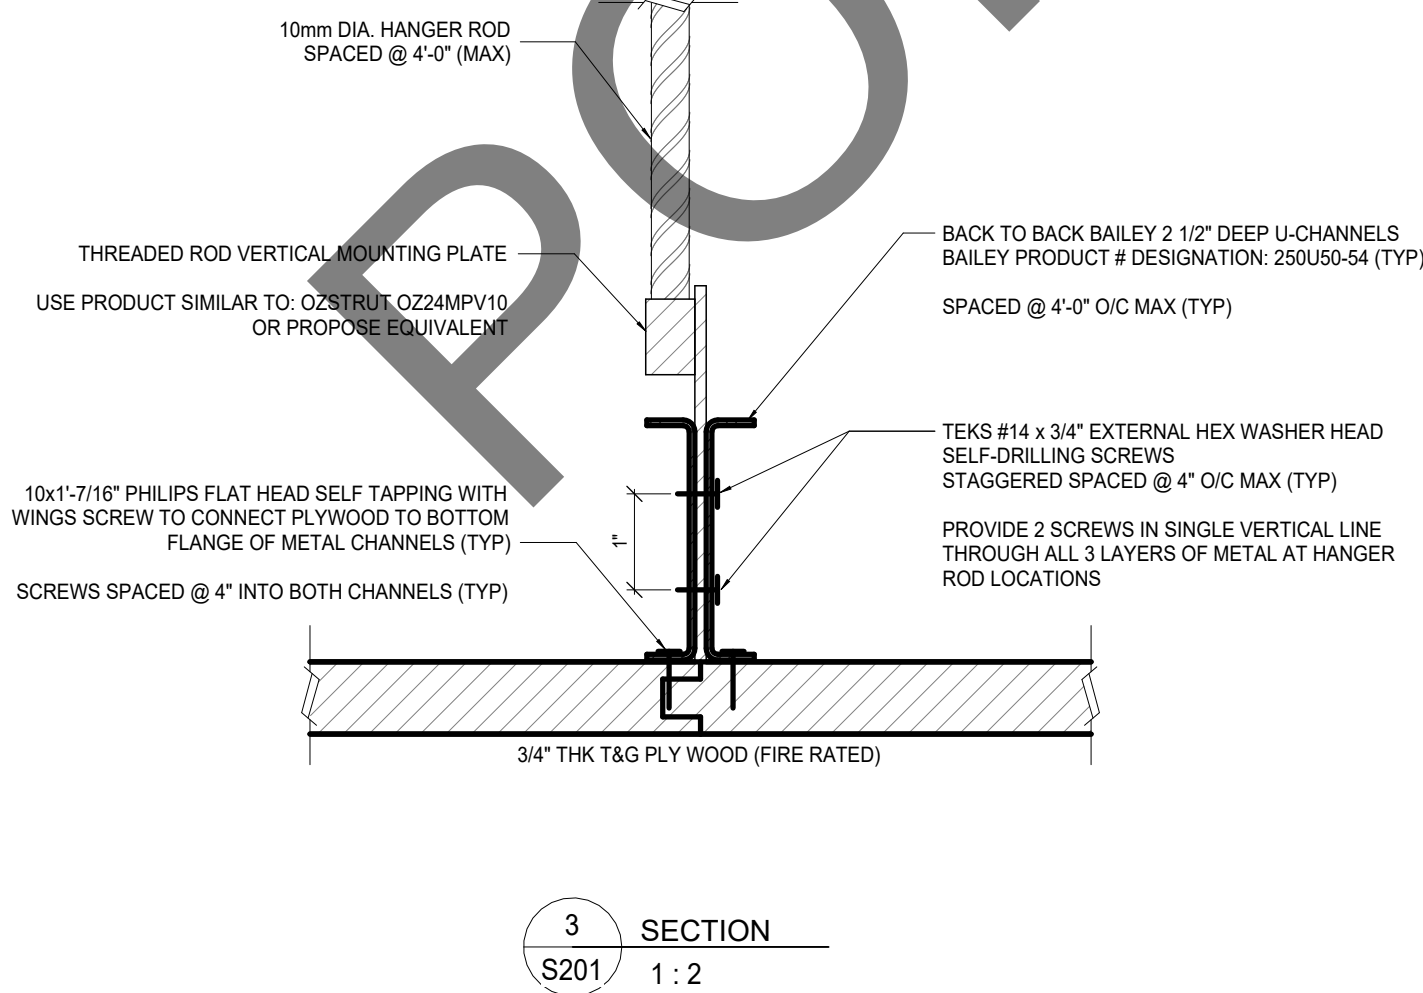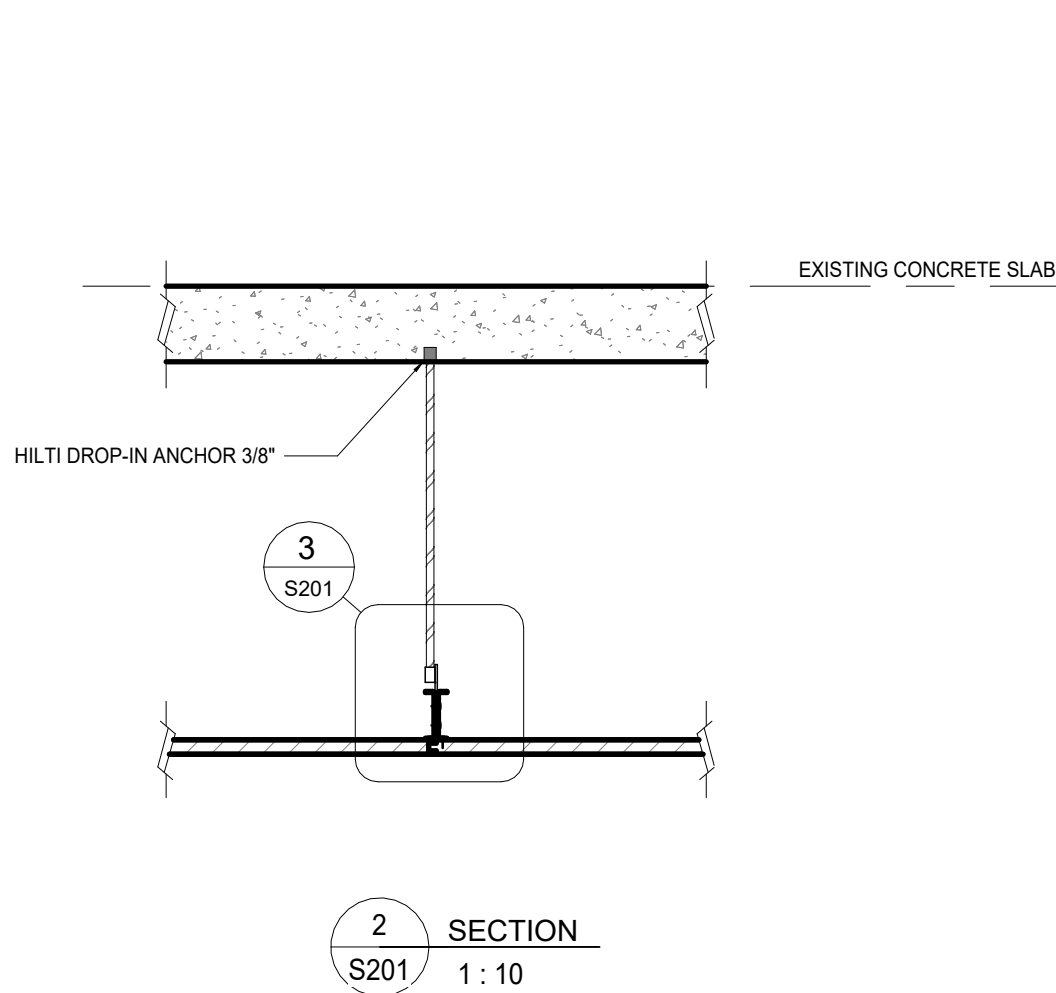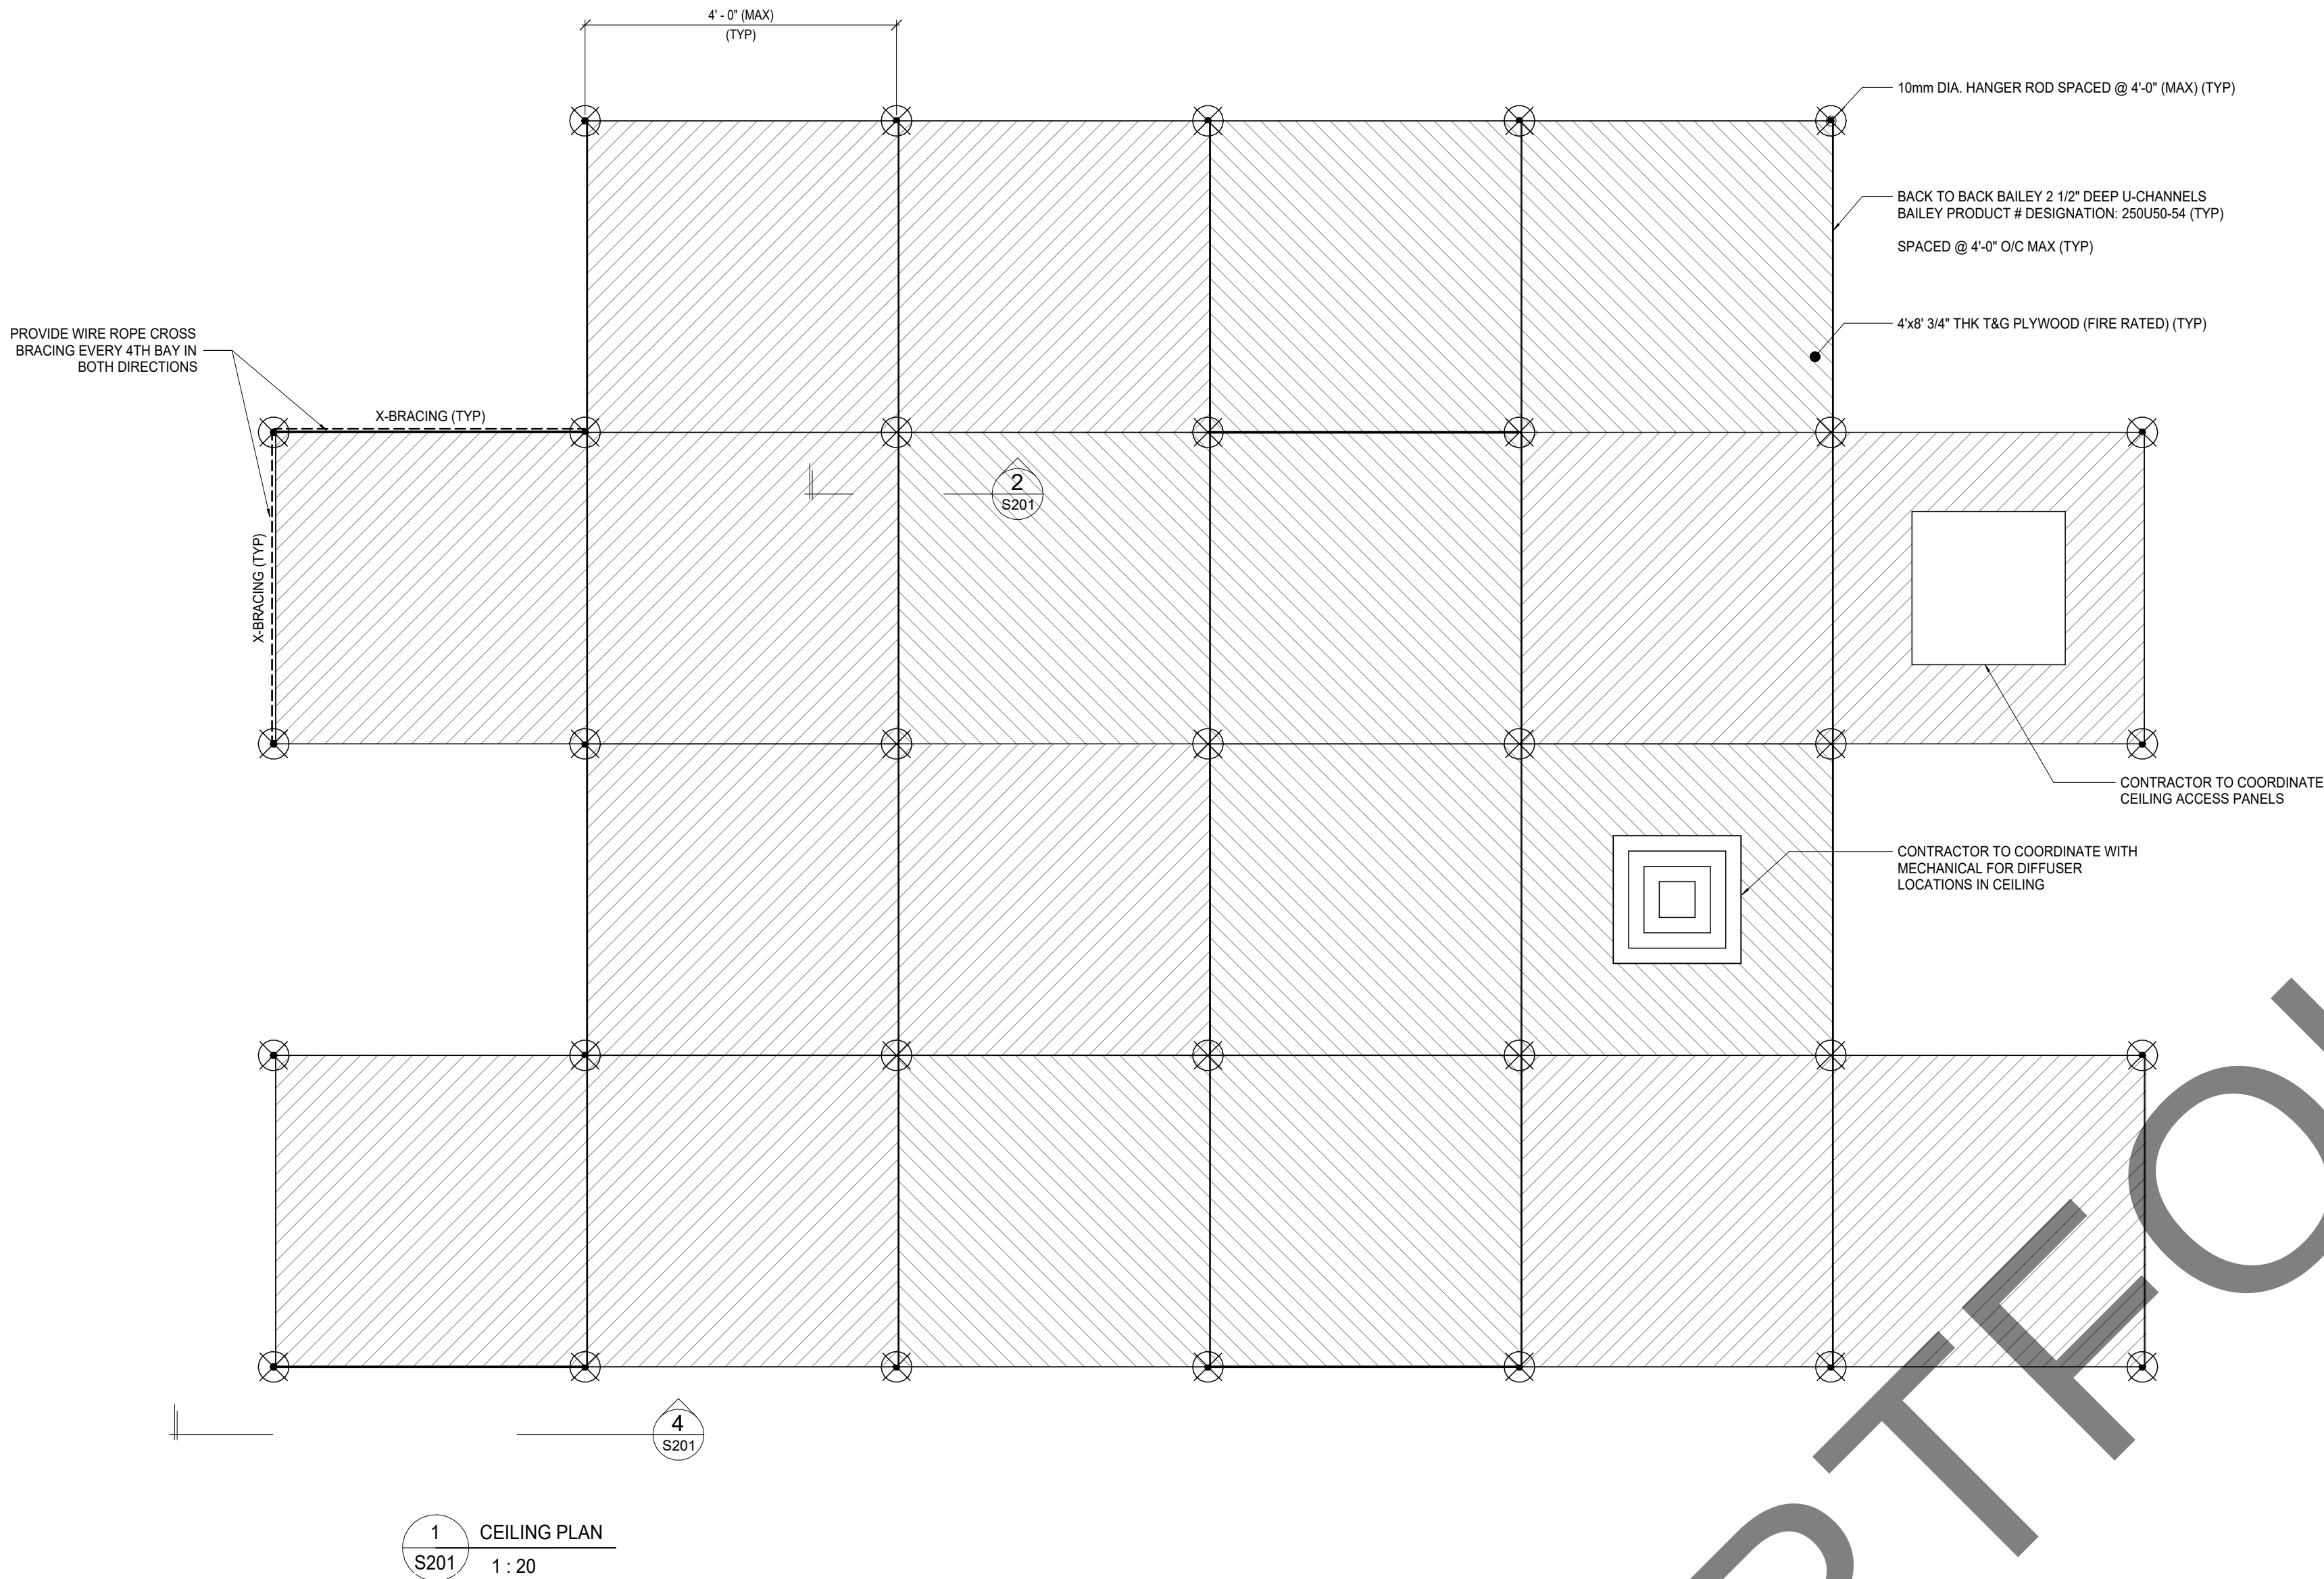

NOTES:

- THIS PROJECT SHALL COMPLY WITH THE ONTARIO BUILDING CODE.
- ANCHORS DESIGNED FOR 400LB POINT LOAD IN TENSION.
- COLD ROLLED CHANNELS DESIGN LOADS:
 - DEAD LOAD: 27 psf
- PLYWOOD DESIGN LOADS:
 - DEAD LOAD: 25psf
- REFER TO VISO LIGHTING SHOP DRAWINGS DATED 2024-12-09 FOR LIGHT FIXTURE DESIGN AND LAYOUT.
- 3/4" PLYWOOD 4'x8' TONGUE AND GROOVE PANELS. FIRE RETARDANT TREATED.

NOTE:

X-RAY OR REBAR SCAN EXISTING CONCRETE SLABS, BEAMS, AND COLUMNS TO LOCATE EXISTING REINFORCING STEEL, STIRRUPS, TIES, AND CONDUITS. DO NOT DRILL THROUGH ANY EXISTING REINFORCEMENT AND DO NOT CUT ANY EXISTING CONDUITS.

ALL EXISTING INFORMATION SHOWN ON DRAWINGS IS TRANSFERRED FROM EXISTING BASE BUILDING DRAWINGS. CONTRACTOR SHALL BE RESPONSIBLE TO SITE VERIFY THE ACCURACY OF THESE DOCUMENTS WITH AS-BUILT CONDITIONS. ALL DETERMINATION OF EXISTING CONDITIONS MUST BE MADE PRIOR TO ANY STRUCTURAL DEMOLITION.